

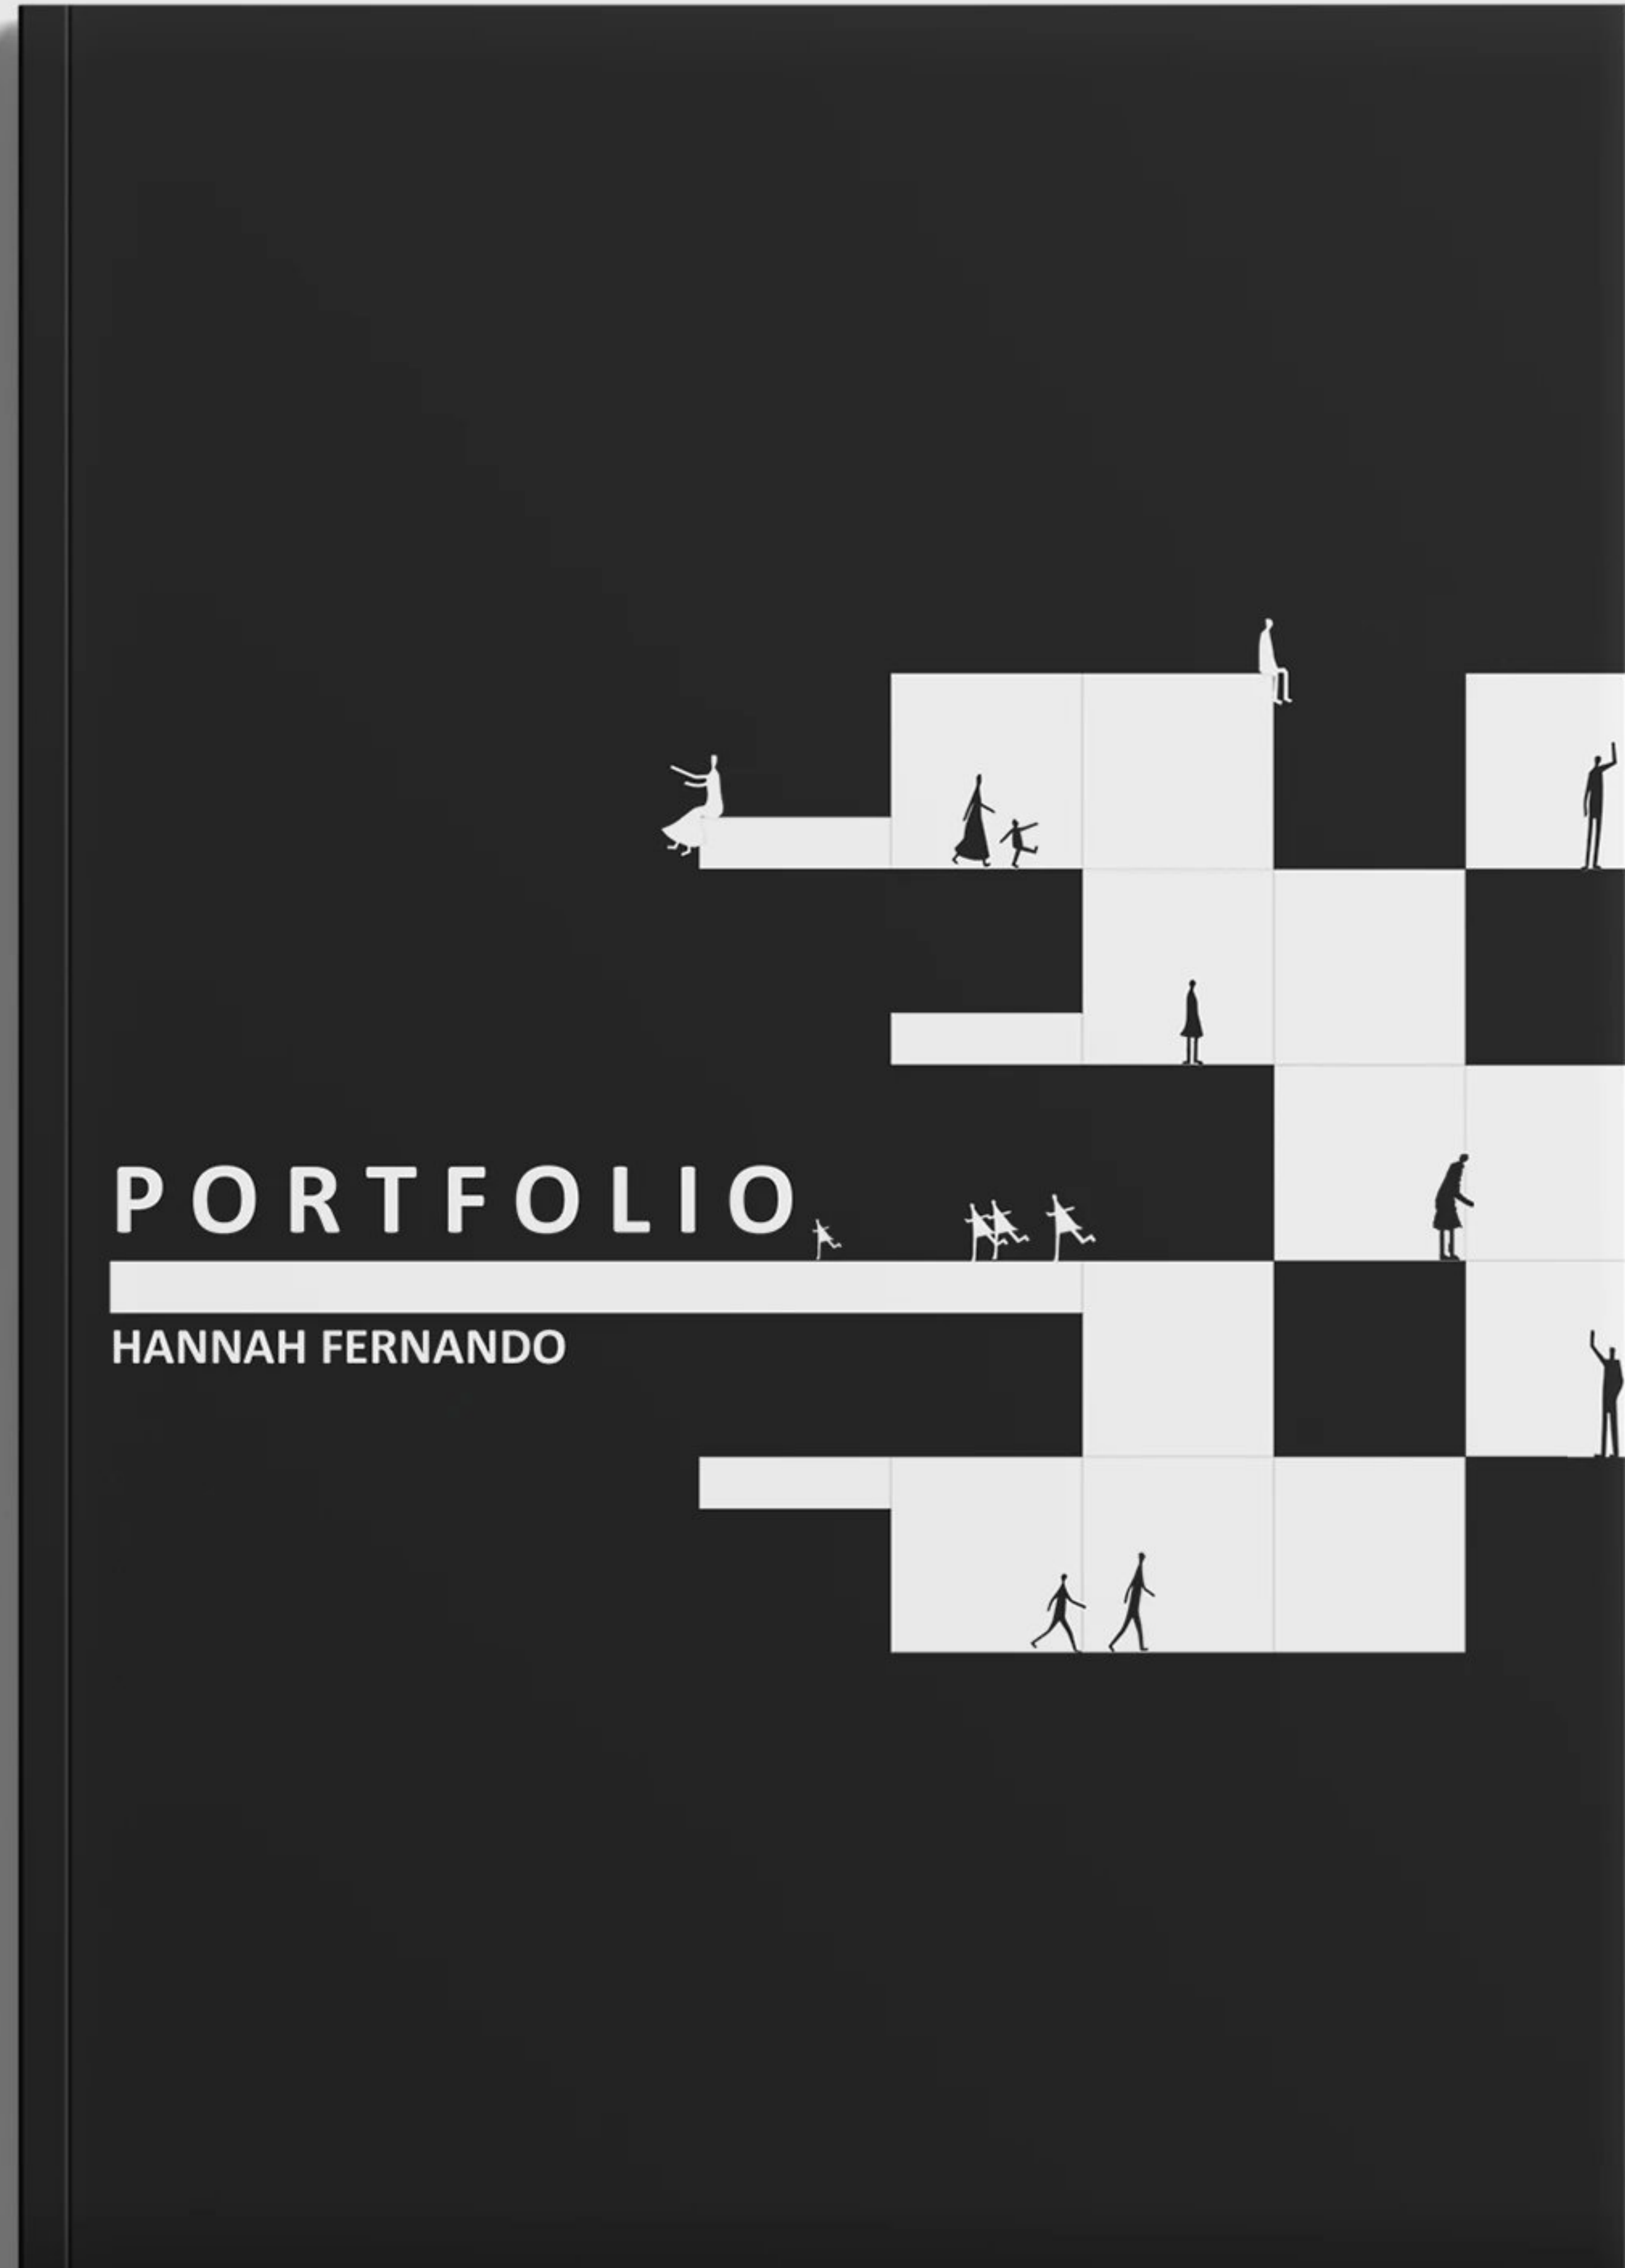


Table of CONTENTS

University *Year 2*
Agritech Project: Mound Park 4

Diagrams and Technical Drawings 6


Artistic Renders 8

University *Year 3*
School of Architecture 10

Diagrams and Technical Drawings 12

Artistic Renders 14

University Project - Year 2

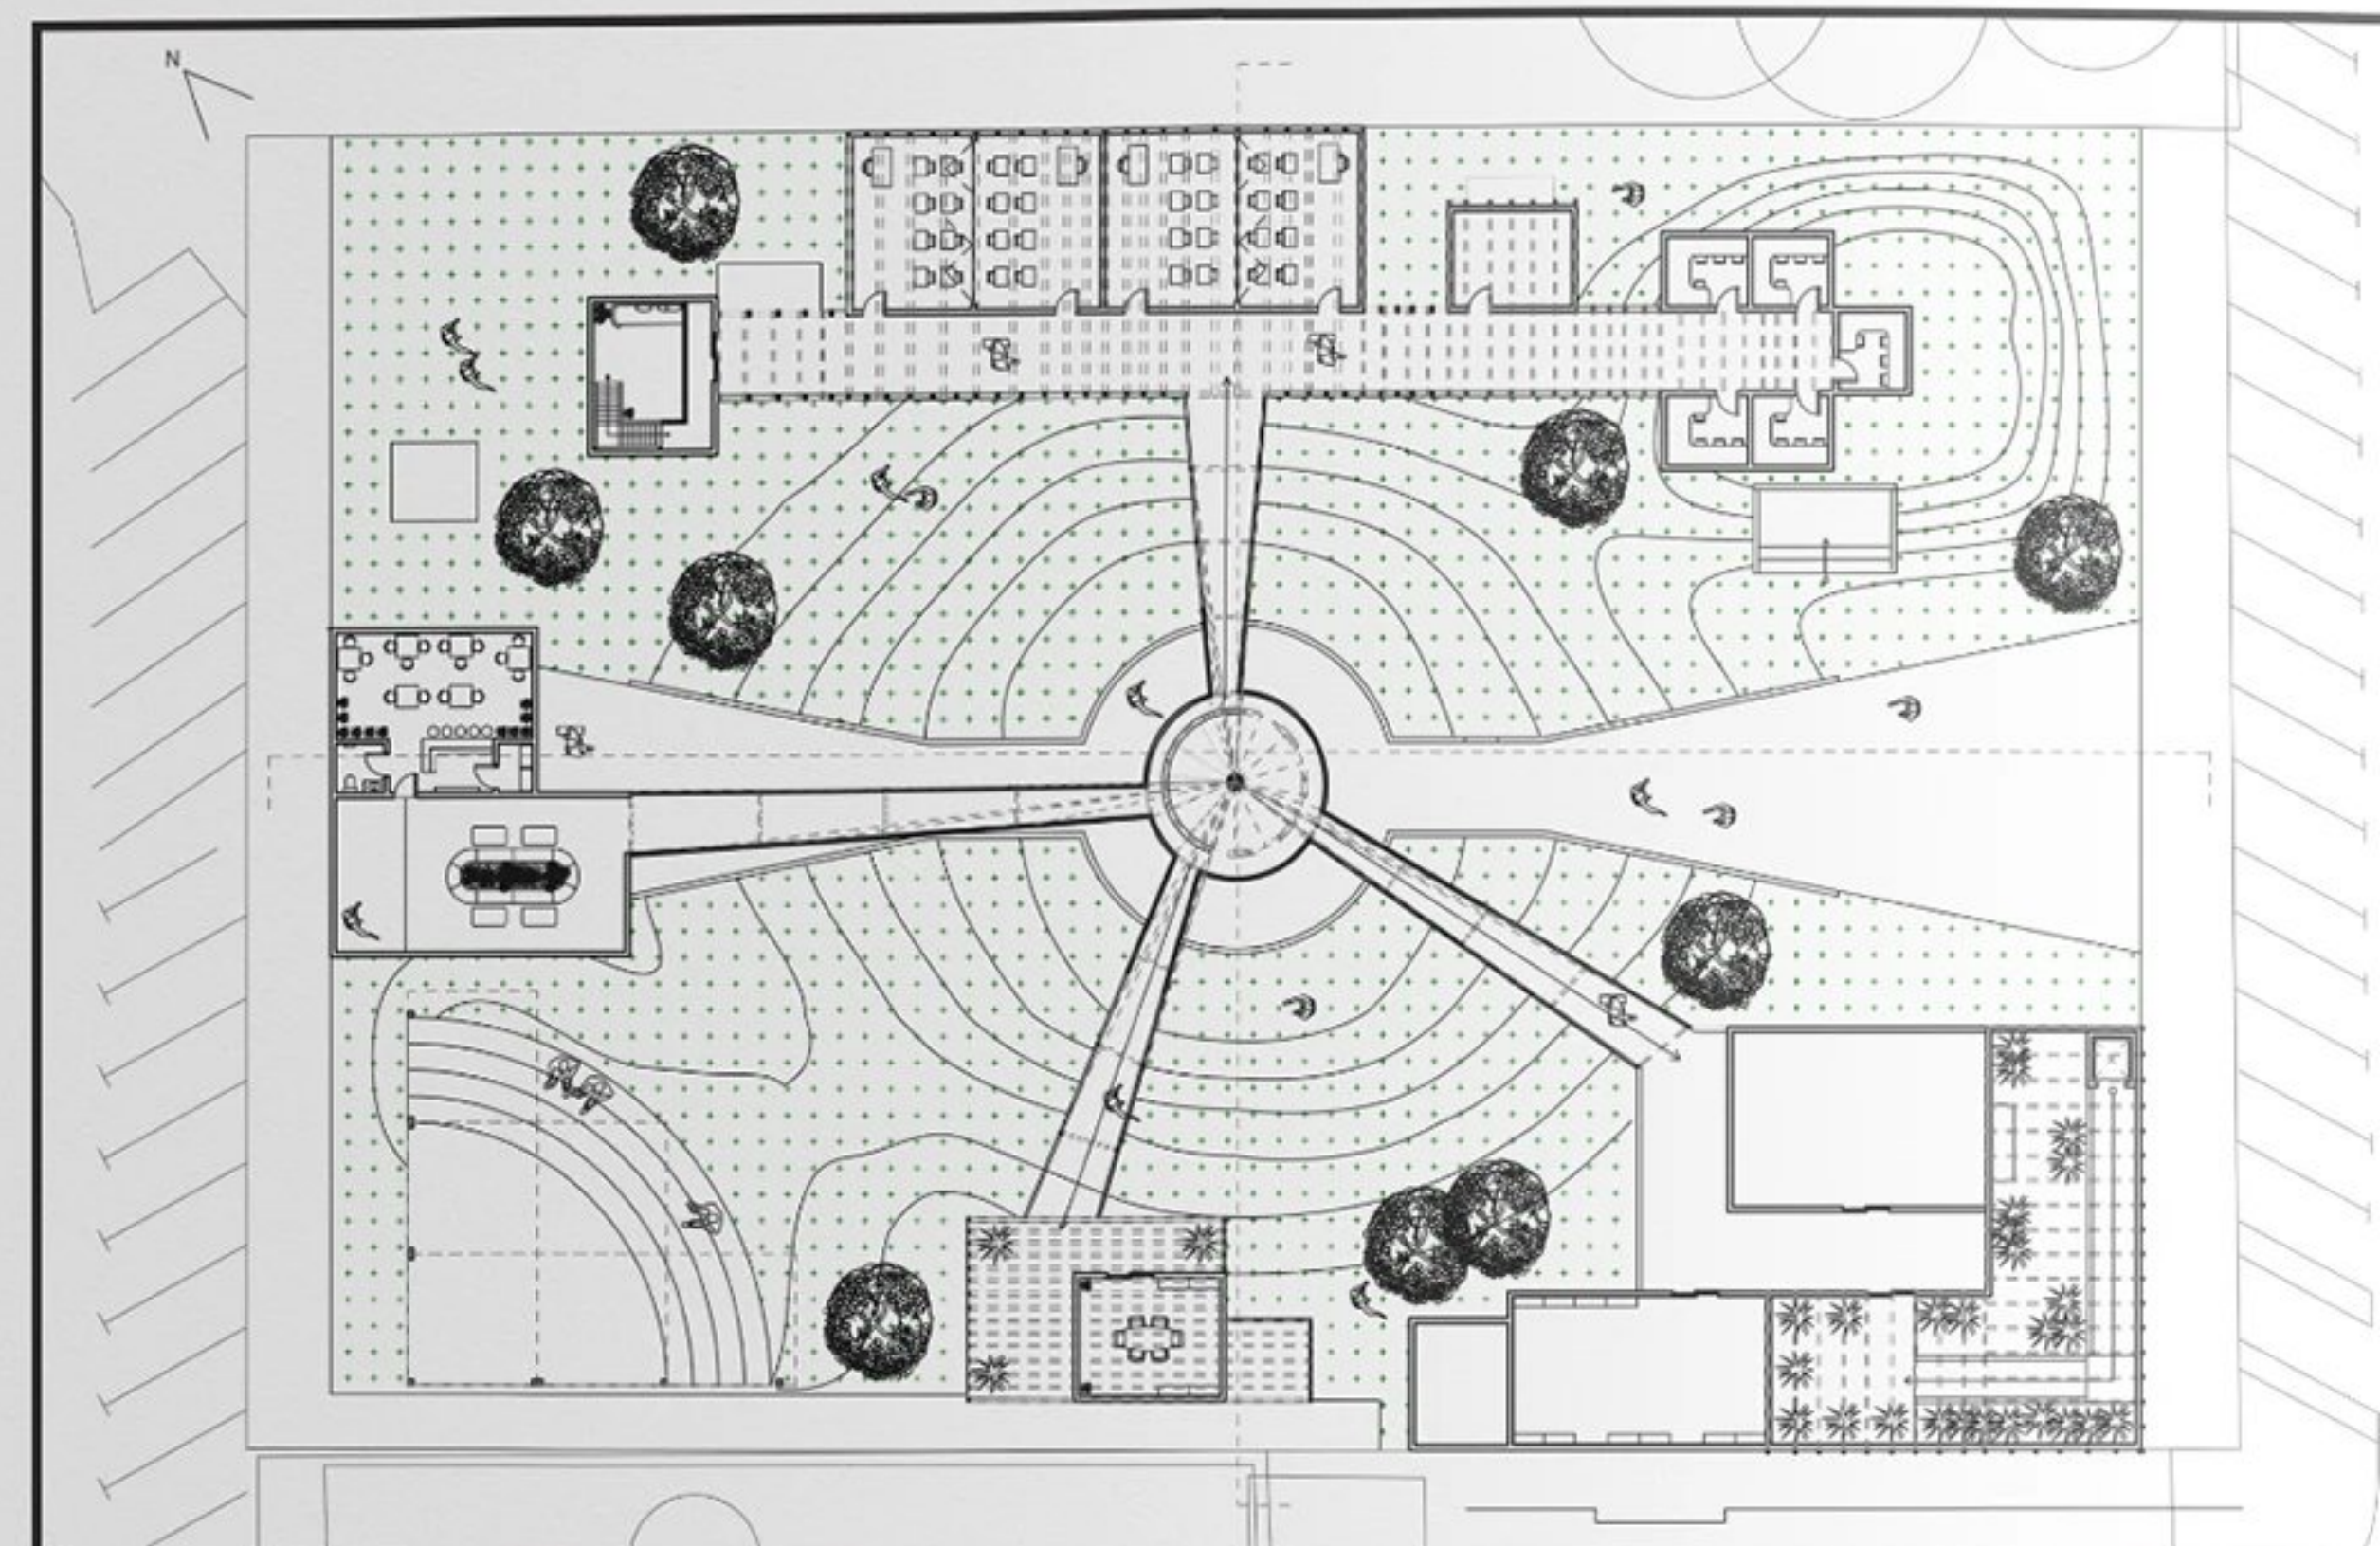


AgriTech Park Project “Mound Park”

Site Location: Al Twar, Dubai, UAE


The School of Life project, launched by Dubai Culture and Arts Authority, is a pioneering initiative designed to enrich the cultural, artistic, and practical skills of Dubai's diverse population. The Agri-Tech Park “Mound Park” is a project that aims to transform the Al Twar Urban Centre into a dynamic hub for education and community engagement, guided by the philosophy of serving as a living laboratory for innovation. The project centers on three key elements: an educational zone, a community marketplace, and a climate-responsive design, all aimed at creating a sustainable and inclusive space for learning, leisure, and cultural exchange, while leveraging Dubai's climate and natural environment.




Abstract Diagrams

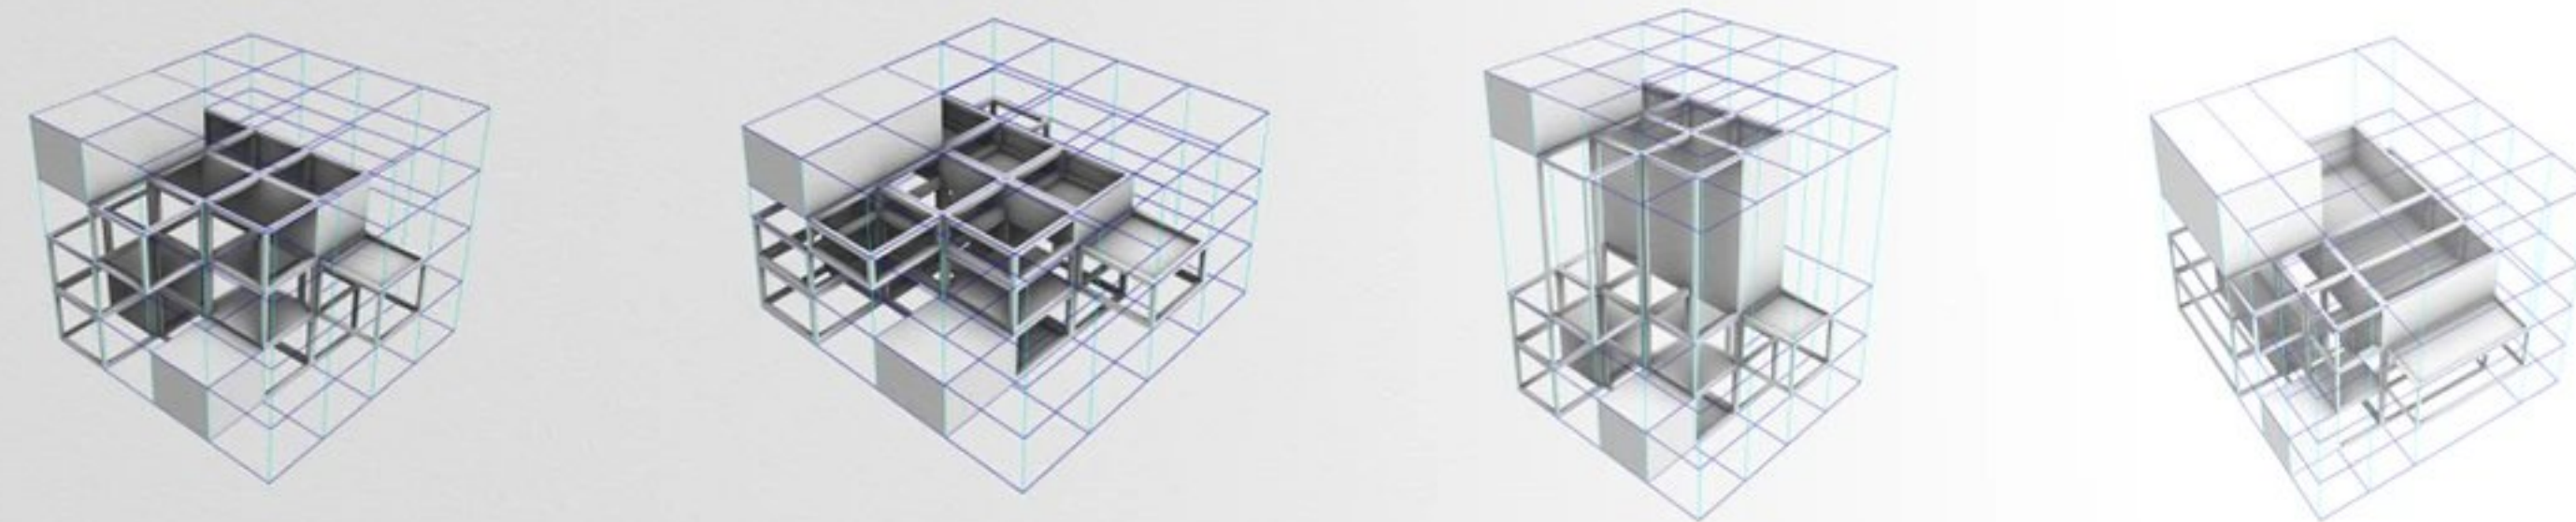

Concept Diagrams

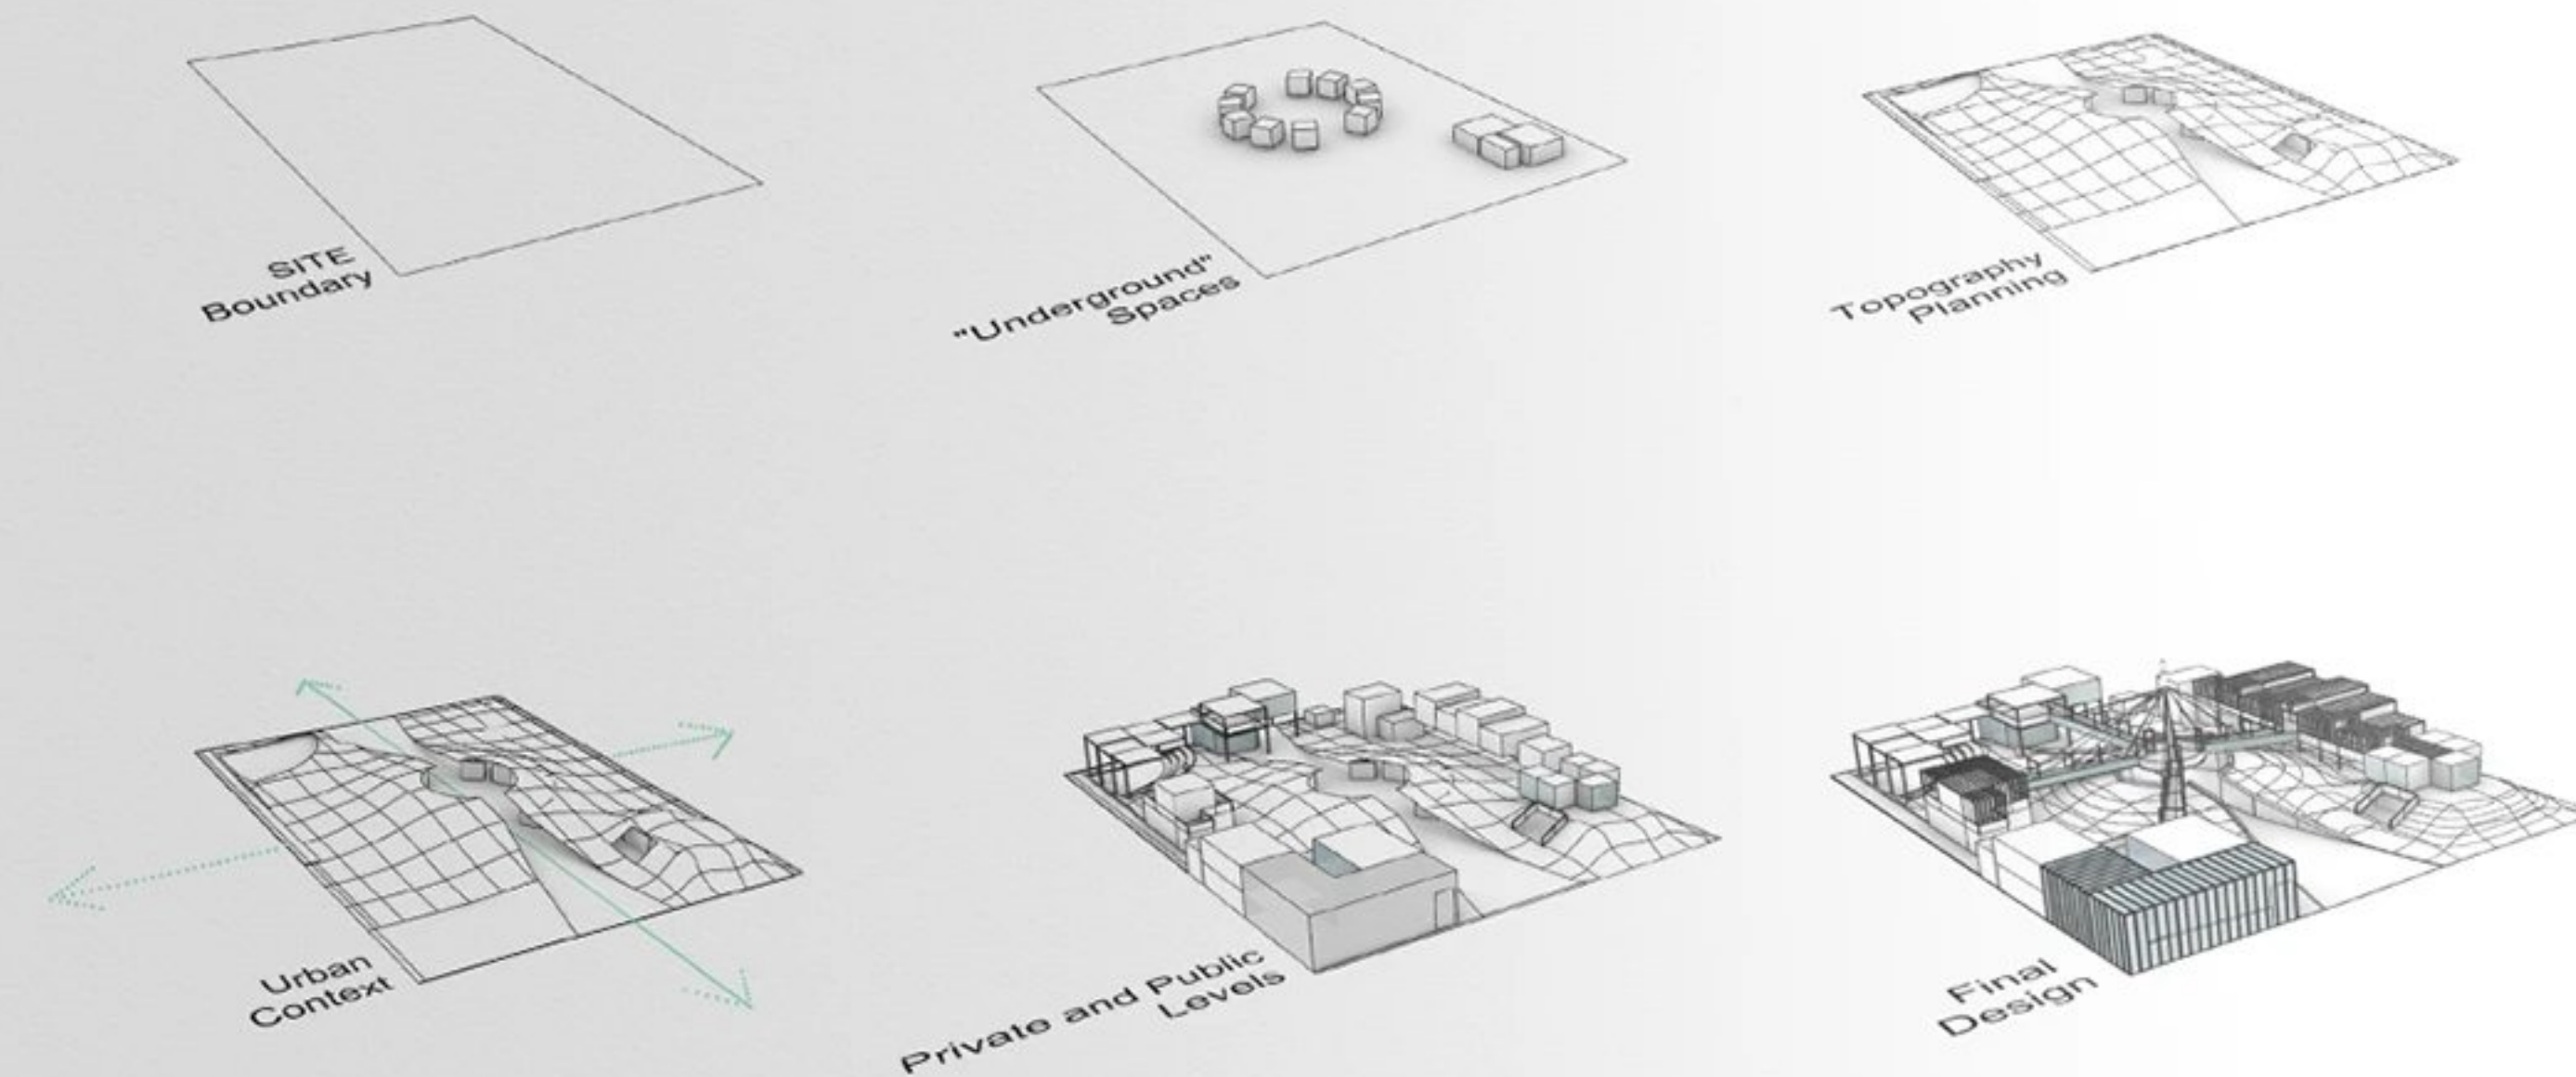


SECTION AA
Scale 1:200

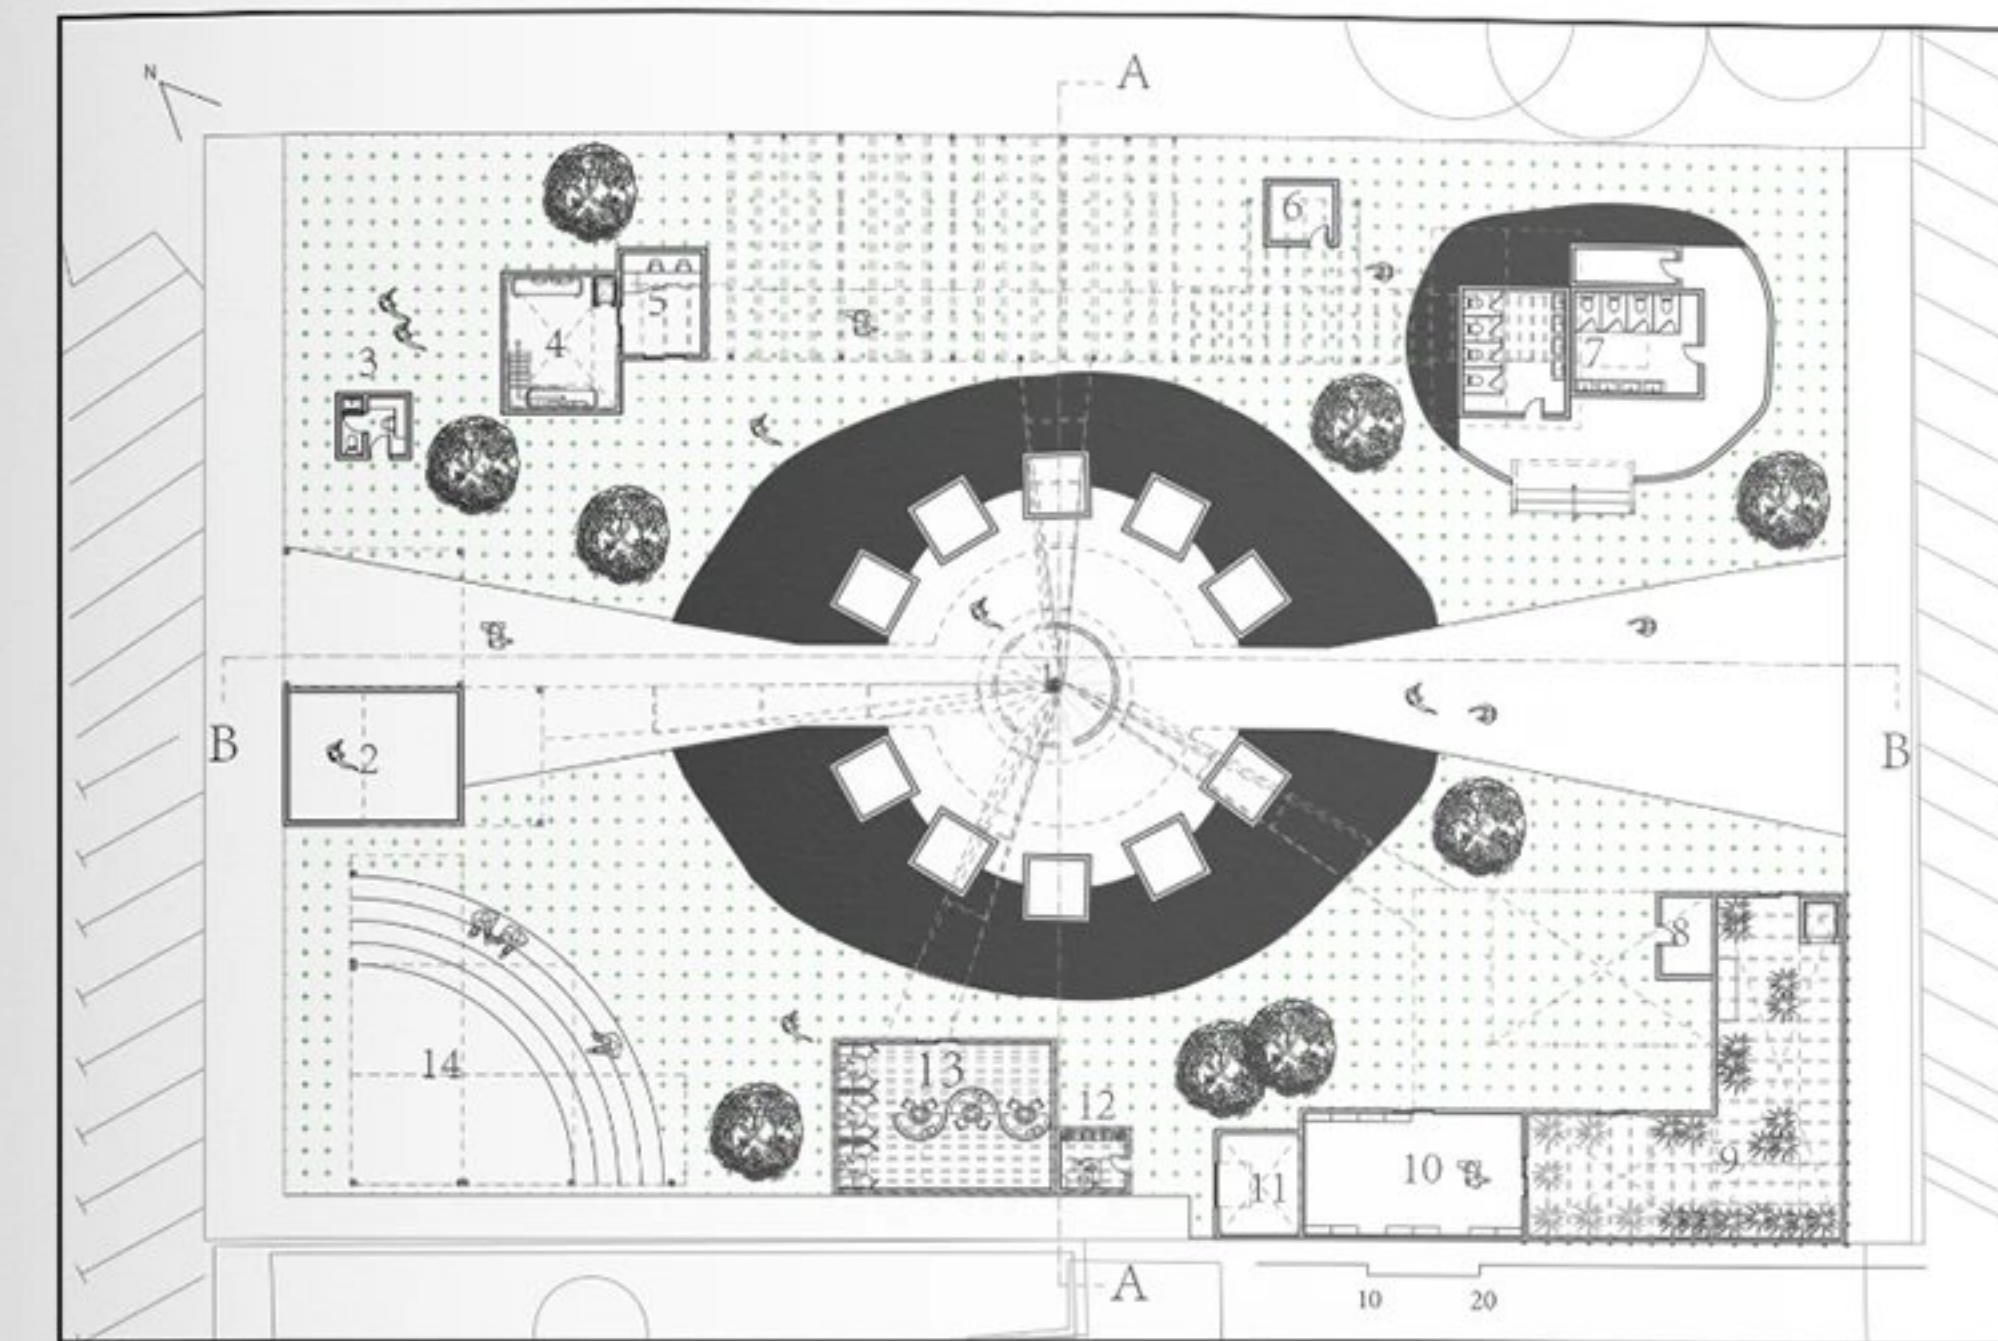

MOUND PARK - GROUND FLOOR PLAN
Scale 1:200


Legend:
1. Marketplace 2. Cafe 3. Security 4. Lounge
5. Reception 6. Electromechanical Room
7. Toilets/Janitor Room 8. Packaging Zone
9. Greenhouse 10. Wet Lab 11. Storage 12. Admin
13. Casual Meeting Space 14. Pecha Kucha Zone

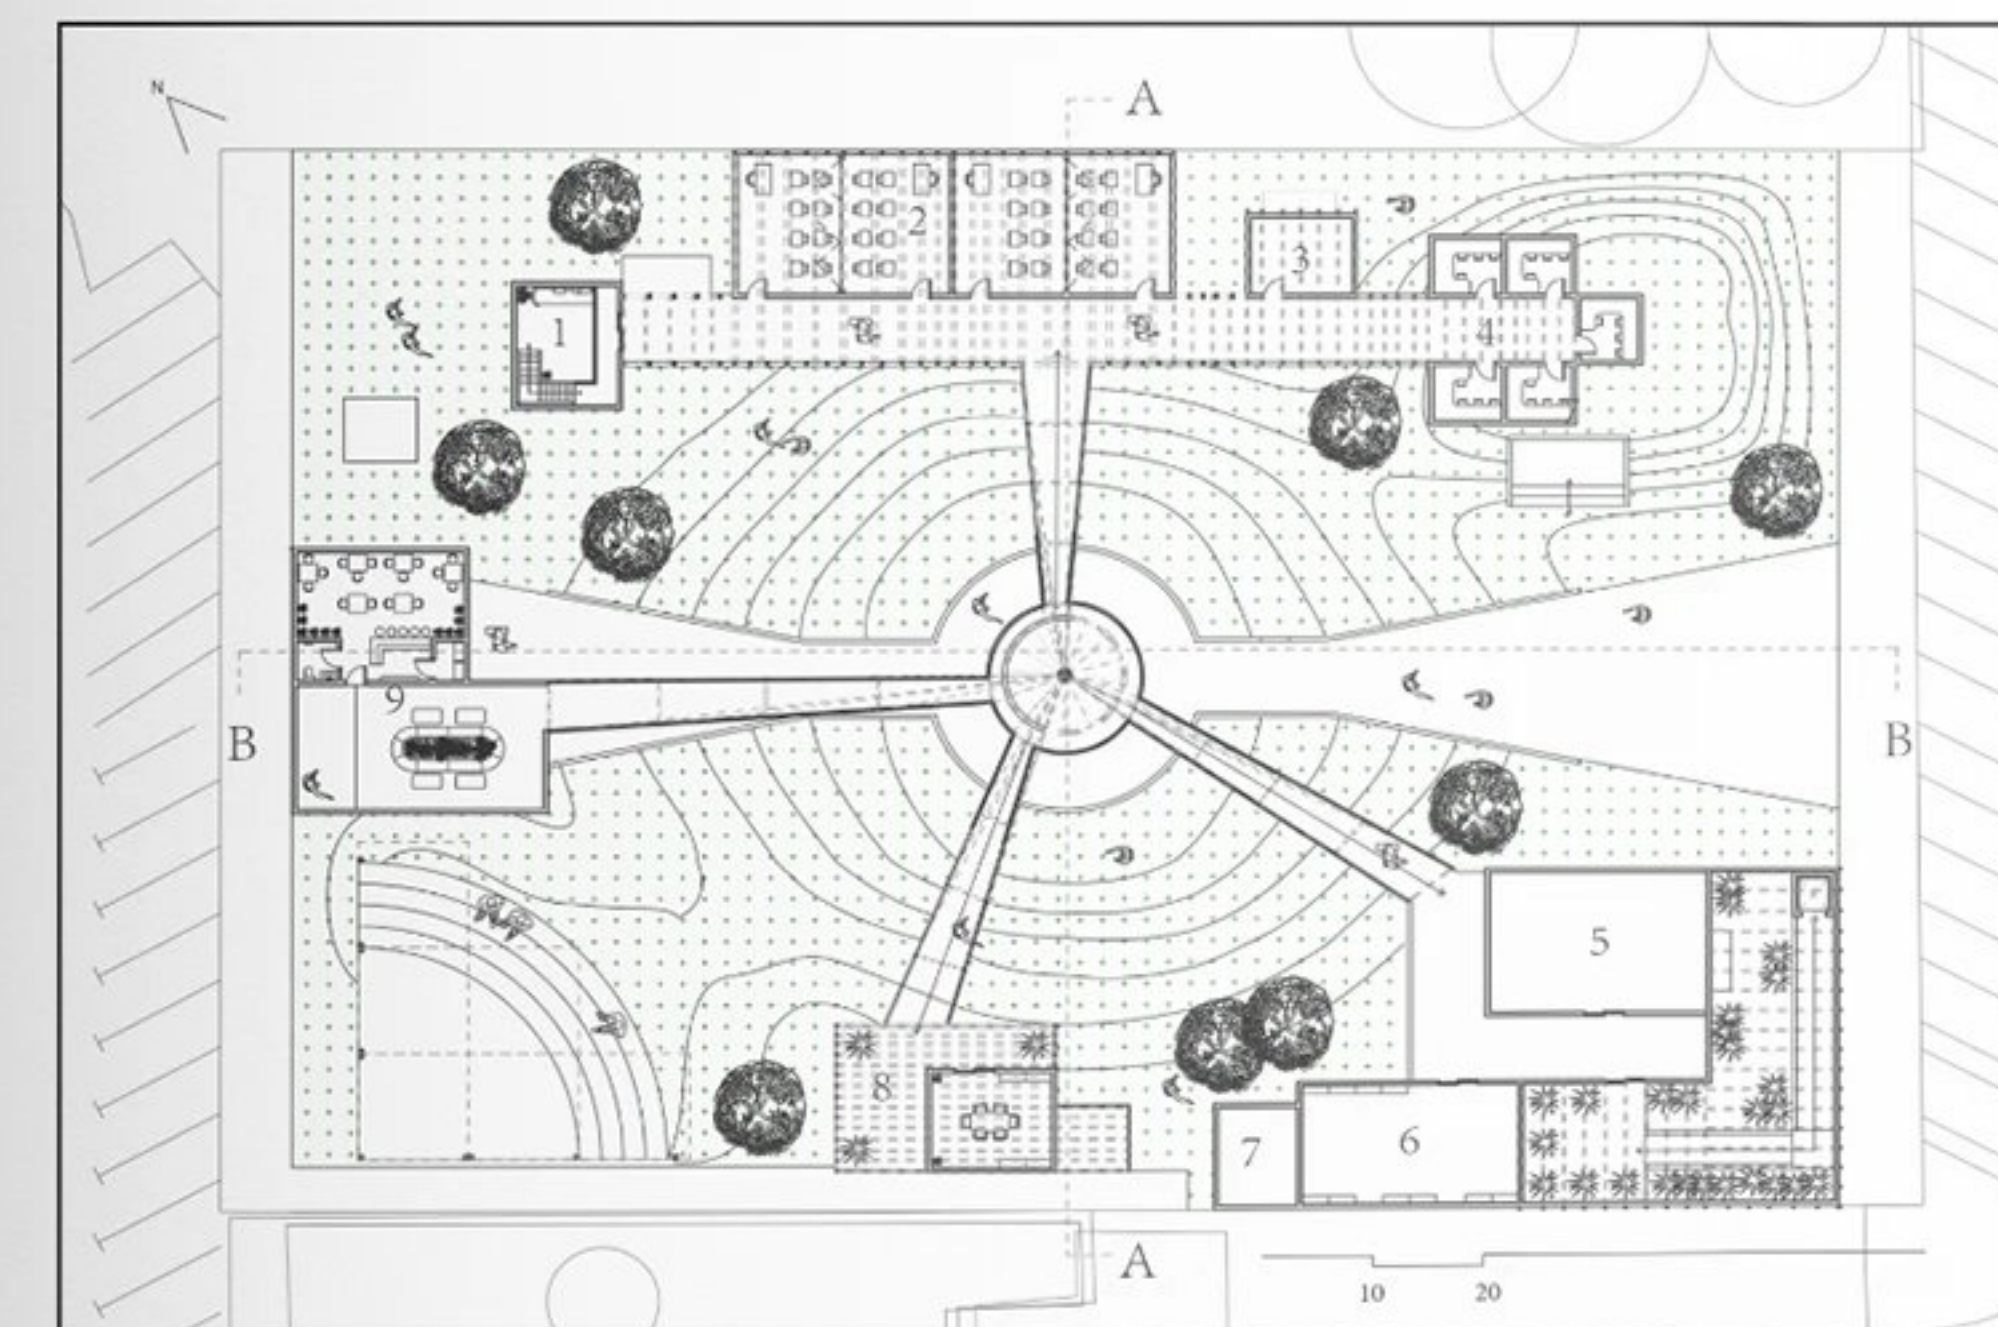

MOUND PARK - FIRST FLOOR PLAN
Scale 1:200

Legend:
1. Lounge 2. Classrooms 3. Storage
4. Co-Working Zone
5. Drone Testing Zone 6. Dry Lab
7. Storage 8. Formal Meeting Space 9. Cafe


SECTION BB
Scale 1:200

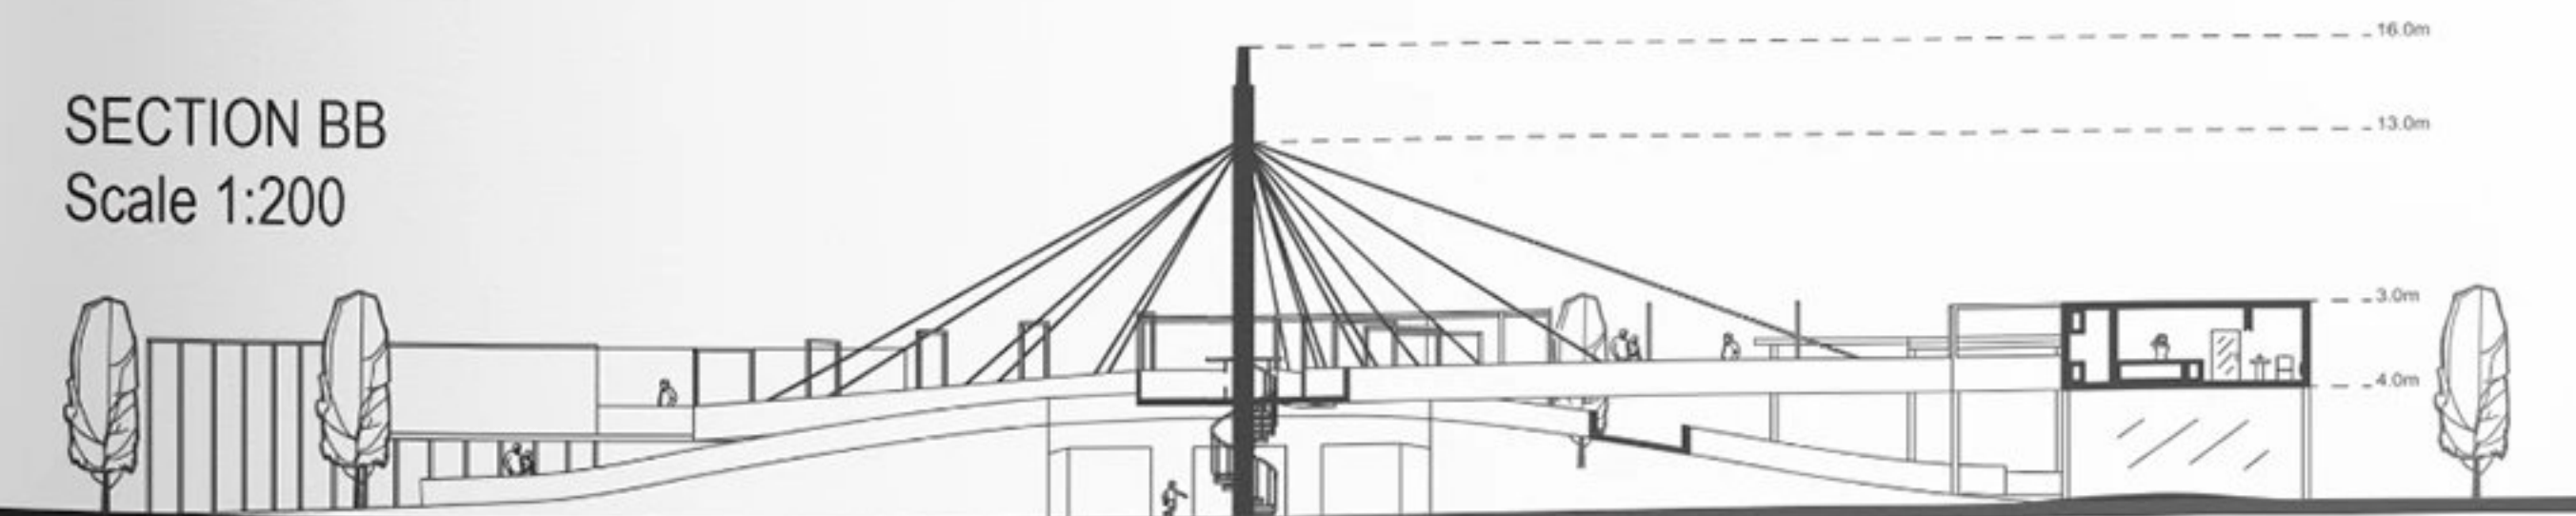

Artistic Renders



University Project - Year 3

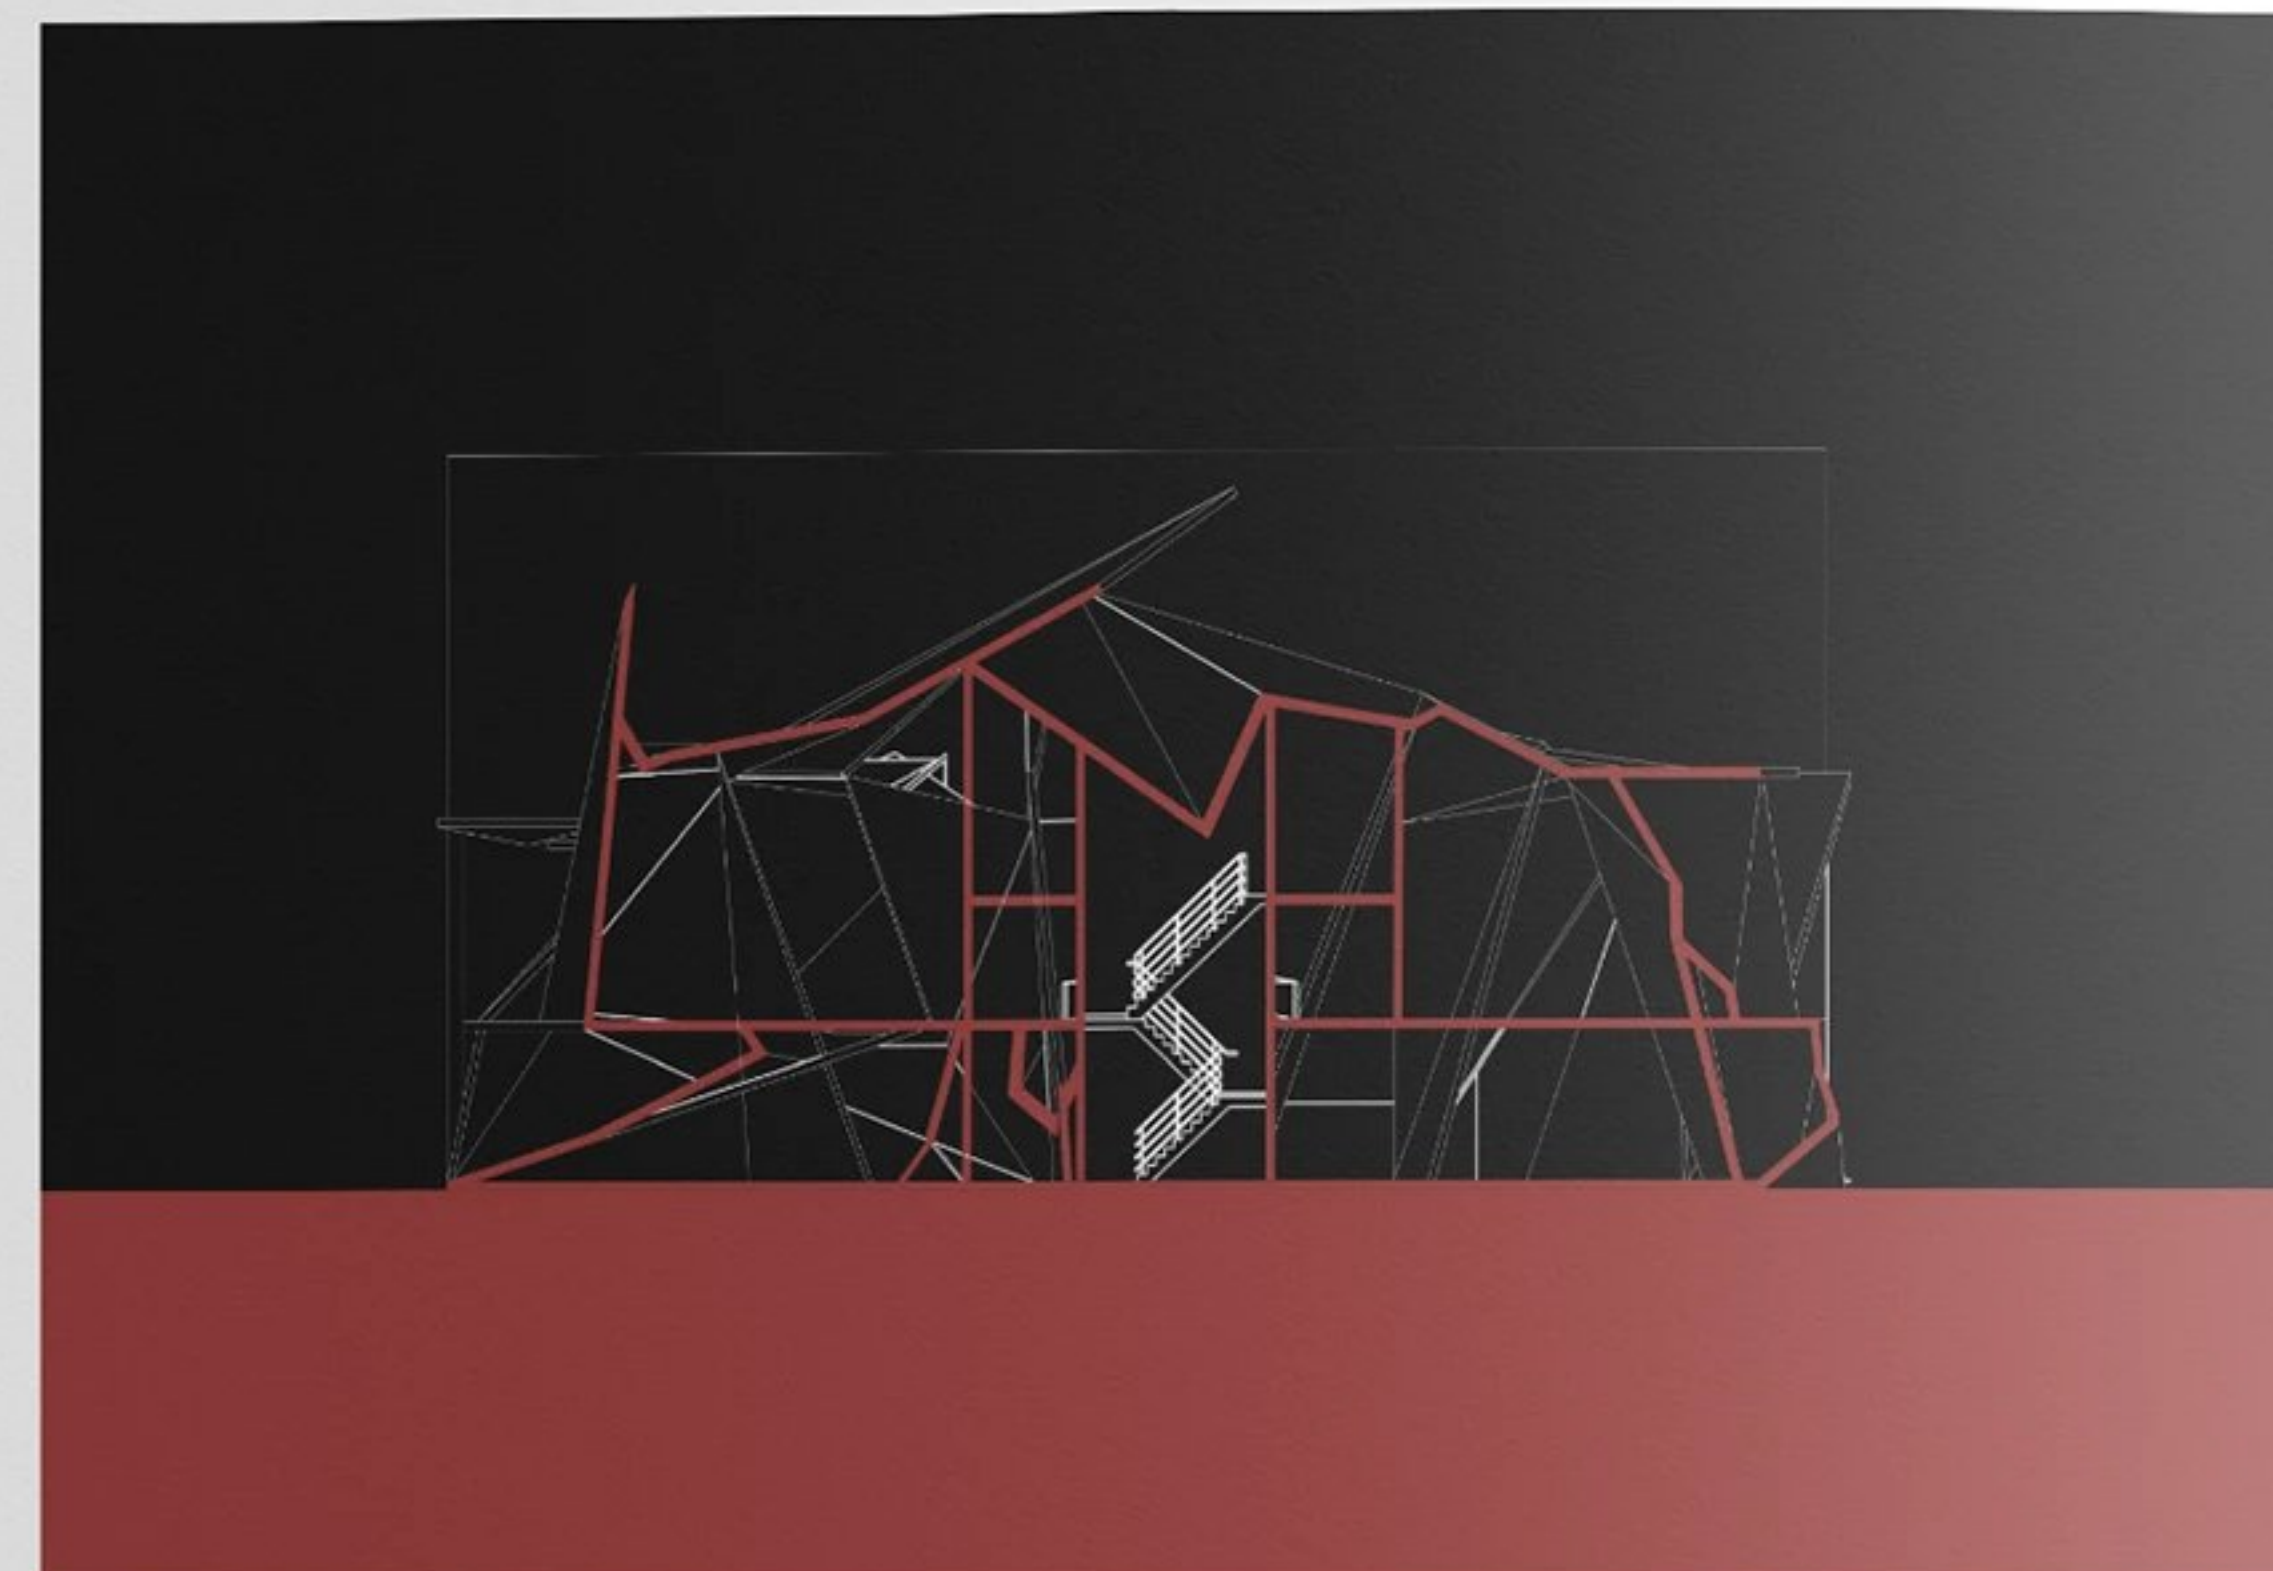


School of Architecture

Site Location: Knowledge Village, Dubai, UAE



A new architecture school in Dubai has the potential to shape the future of the built environment by embracing innovative educational philosophies, technological advancements, and evolving social values. The school should prioritize experiential learning, integrate cutting-edge technologies like 3D printing and AI, and foster a user-centered design approach that considers the relationship between buildings, occupants, and the environment. This includes emphasizing climate-responsive design, community engagement, and the ethical implications of architectural choices, ultimately producing graduates equipped to address the complex challenges of the 21st century and contribute to the evolution of architecture in the Middle East.

"True architectural innovation emerges from the process of active iteration, breaking traditional norms and connecting with communities to create spaces that celebrate vibrancy and diversification."


Hannah Fernando

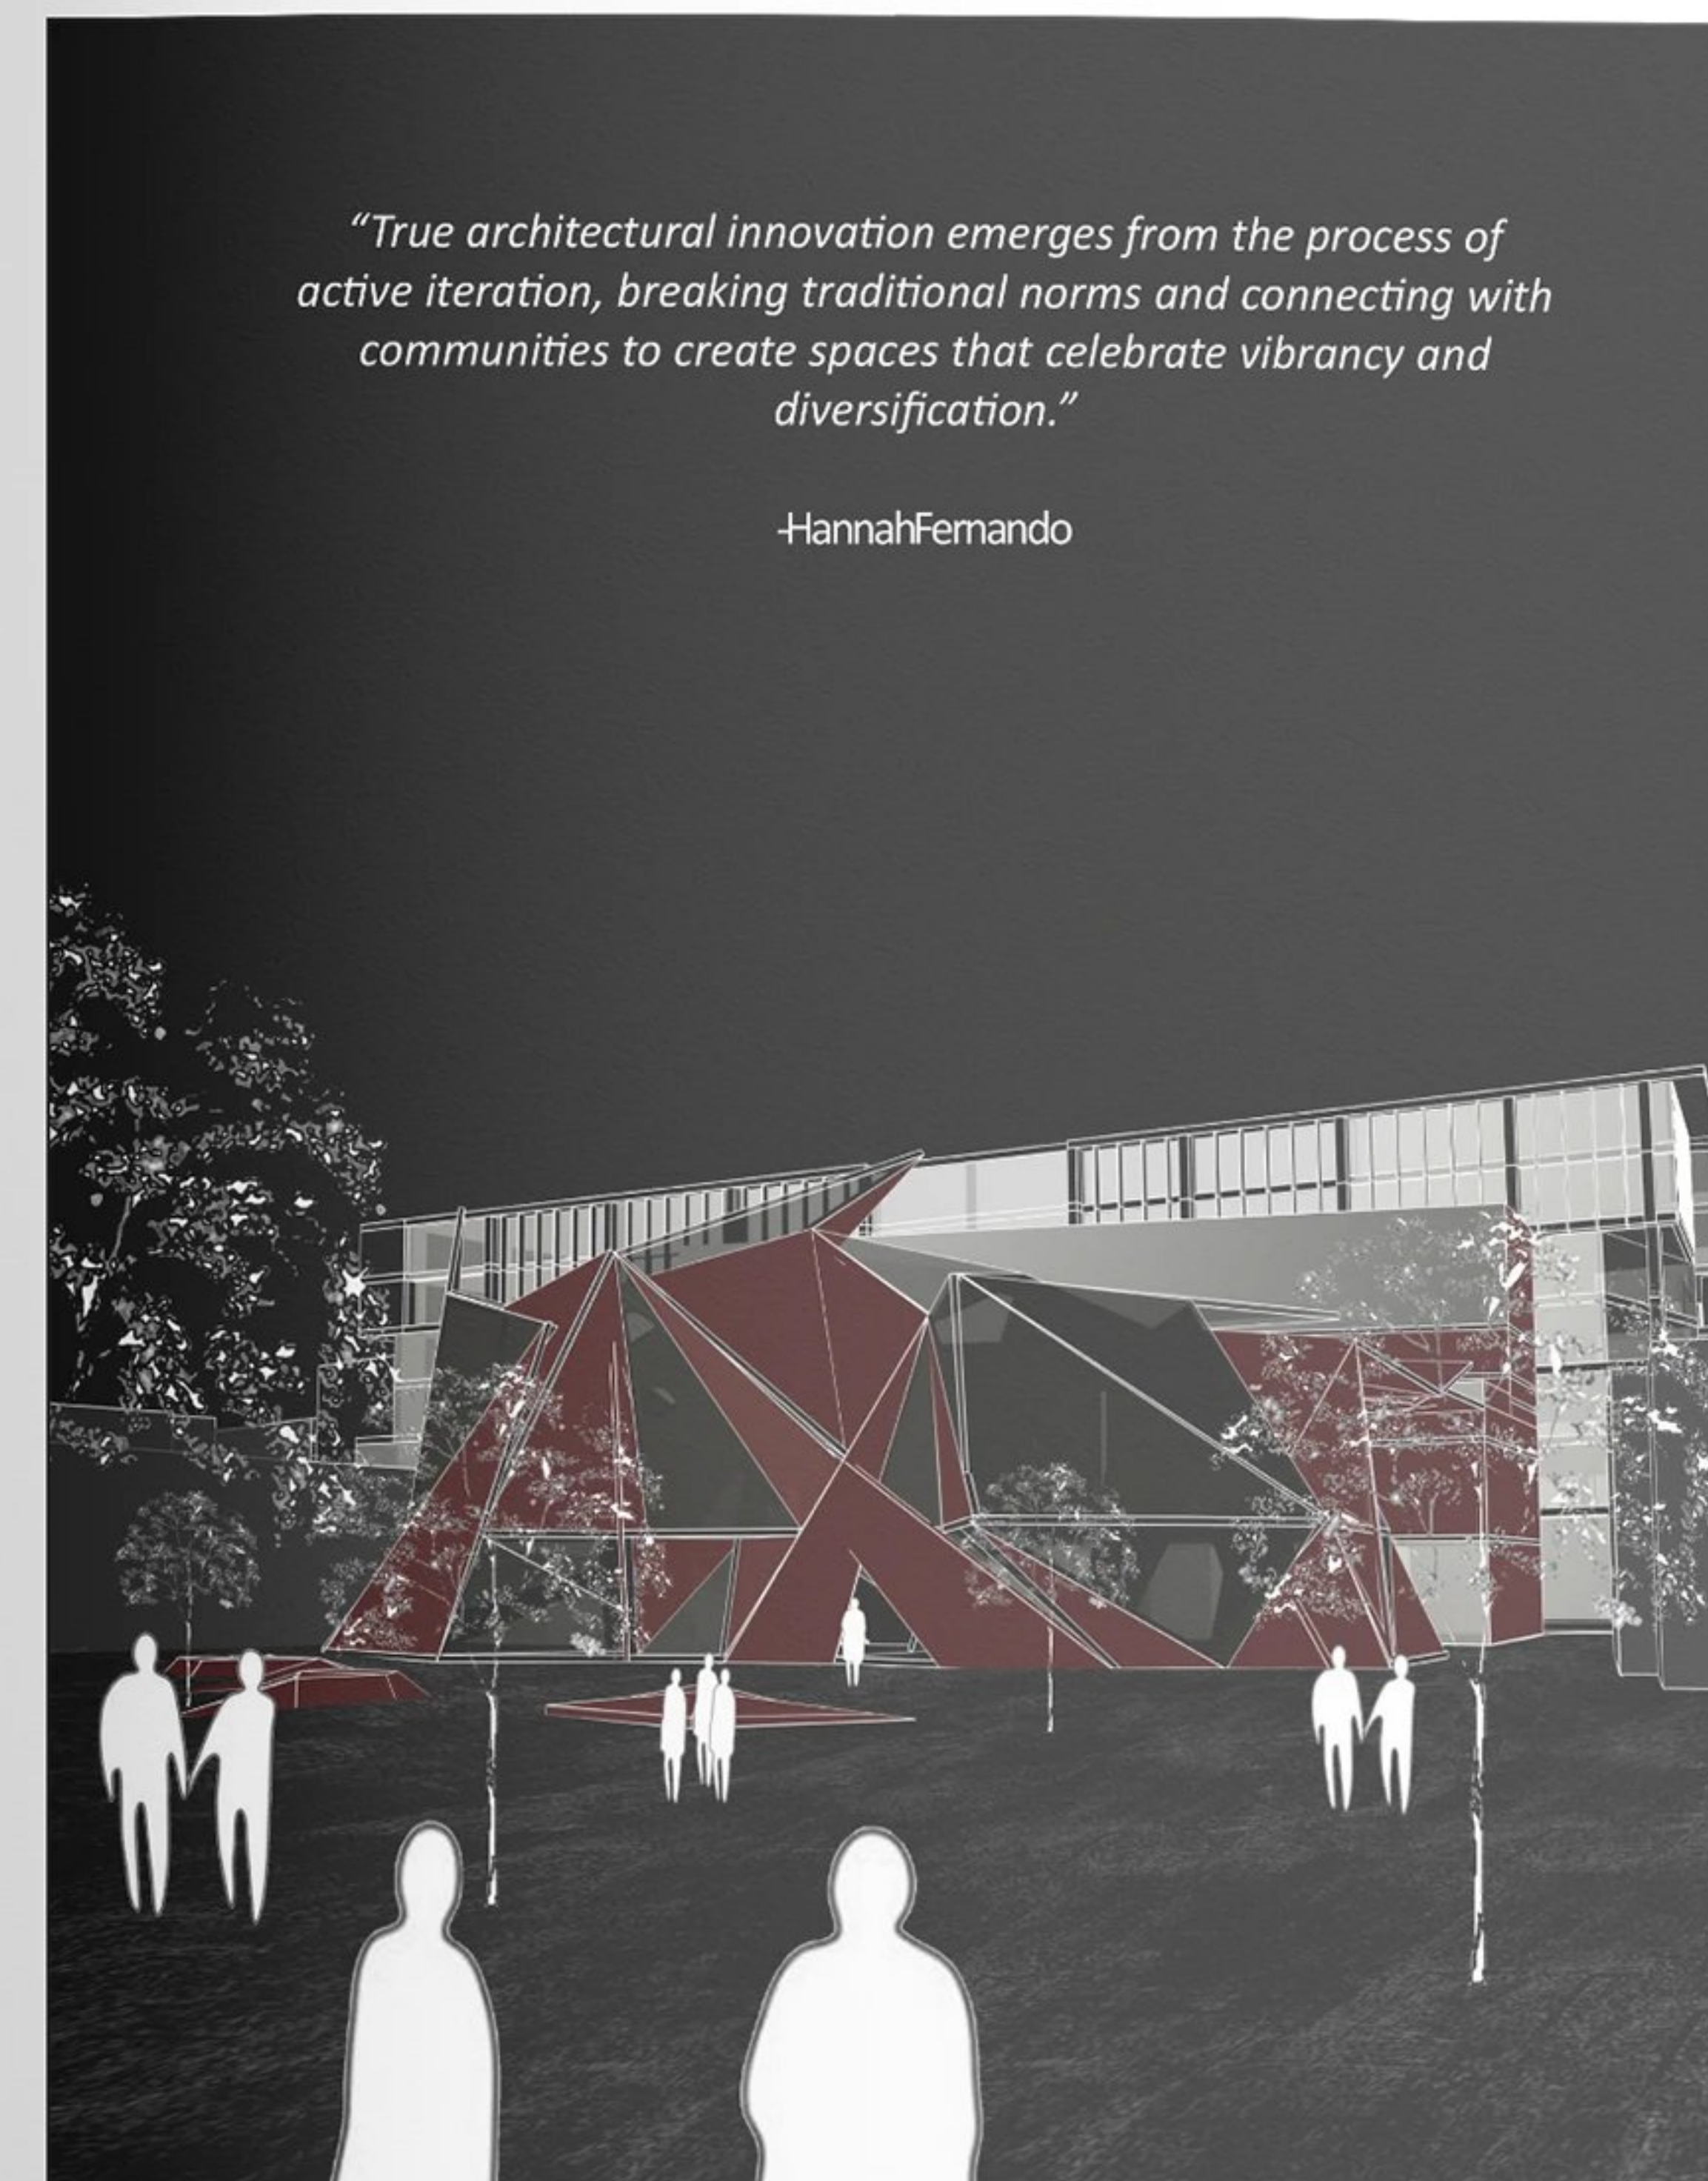

Concept Diagrams and Sketches

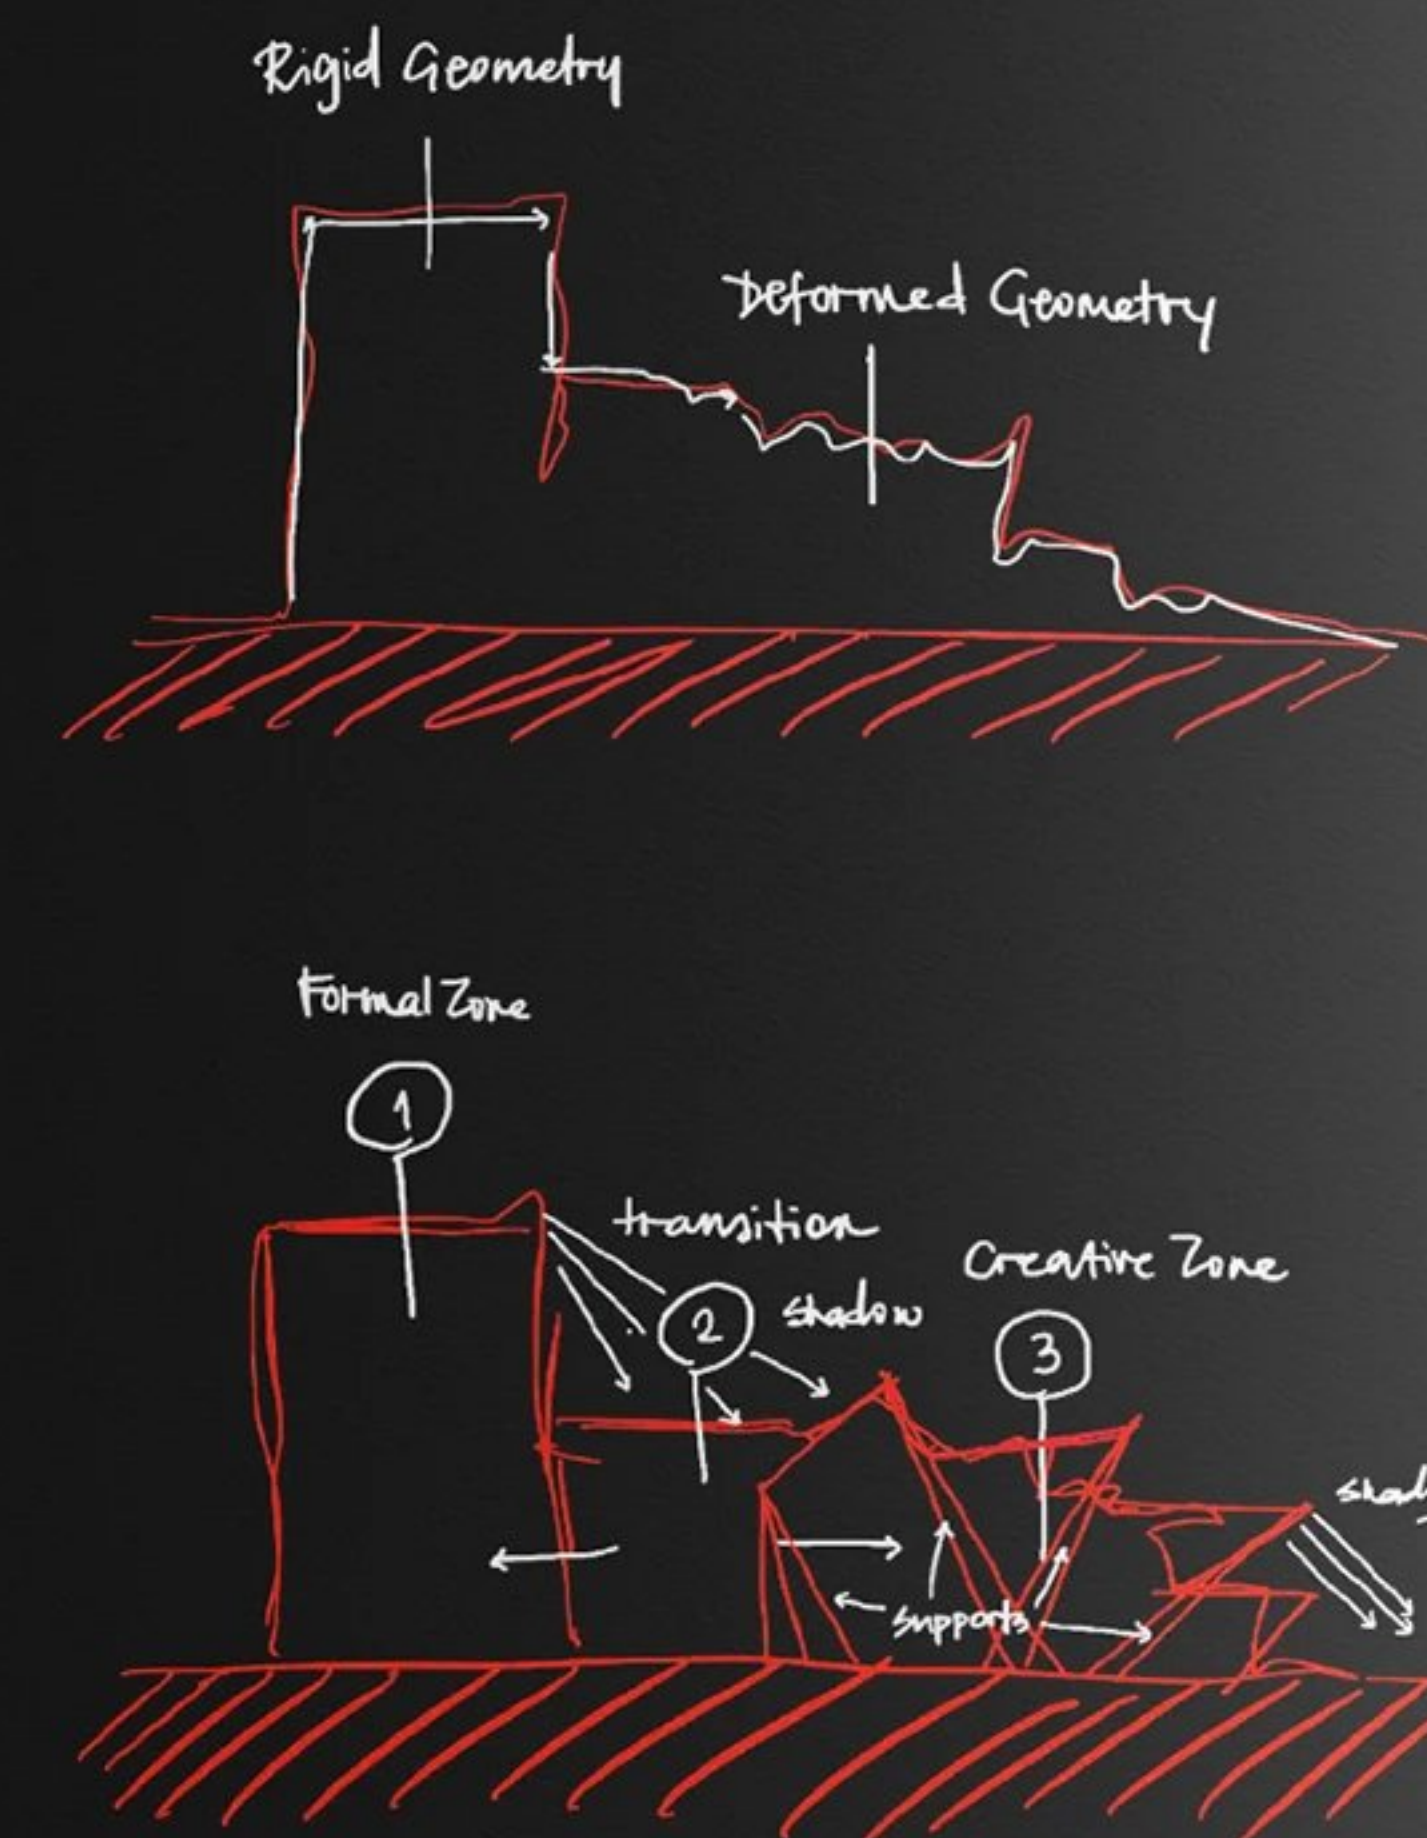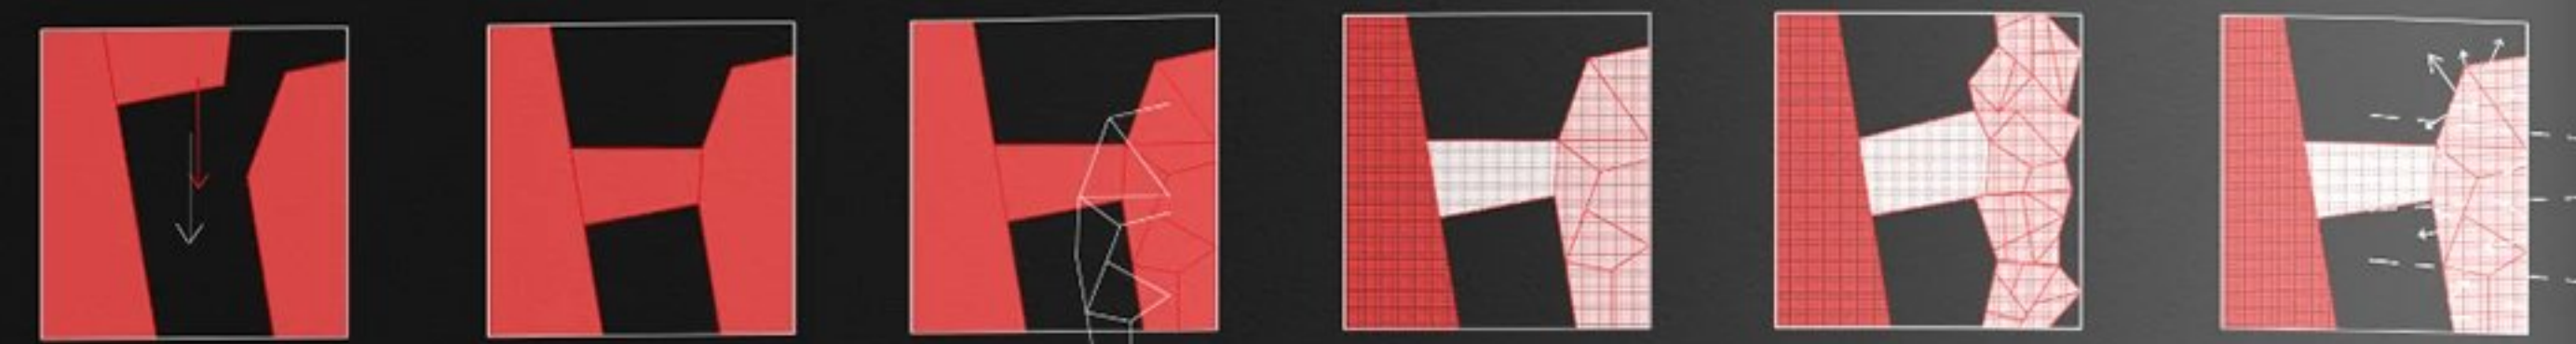

URBAN SECTION AA
SCALE 1:200

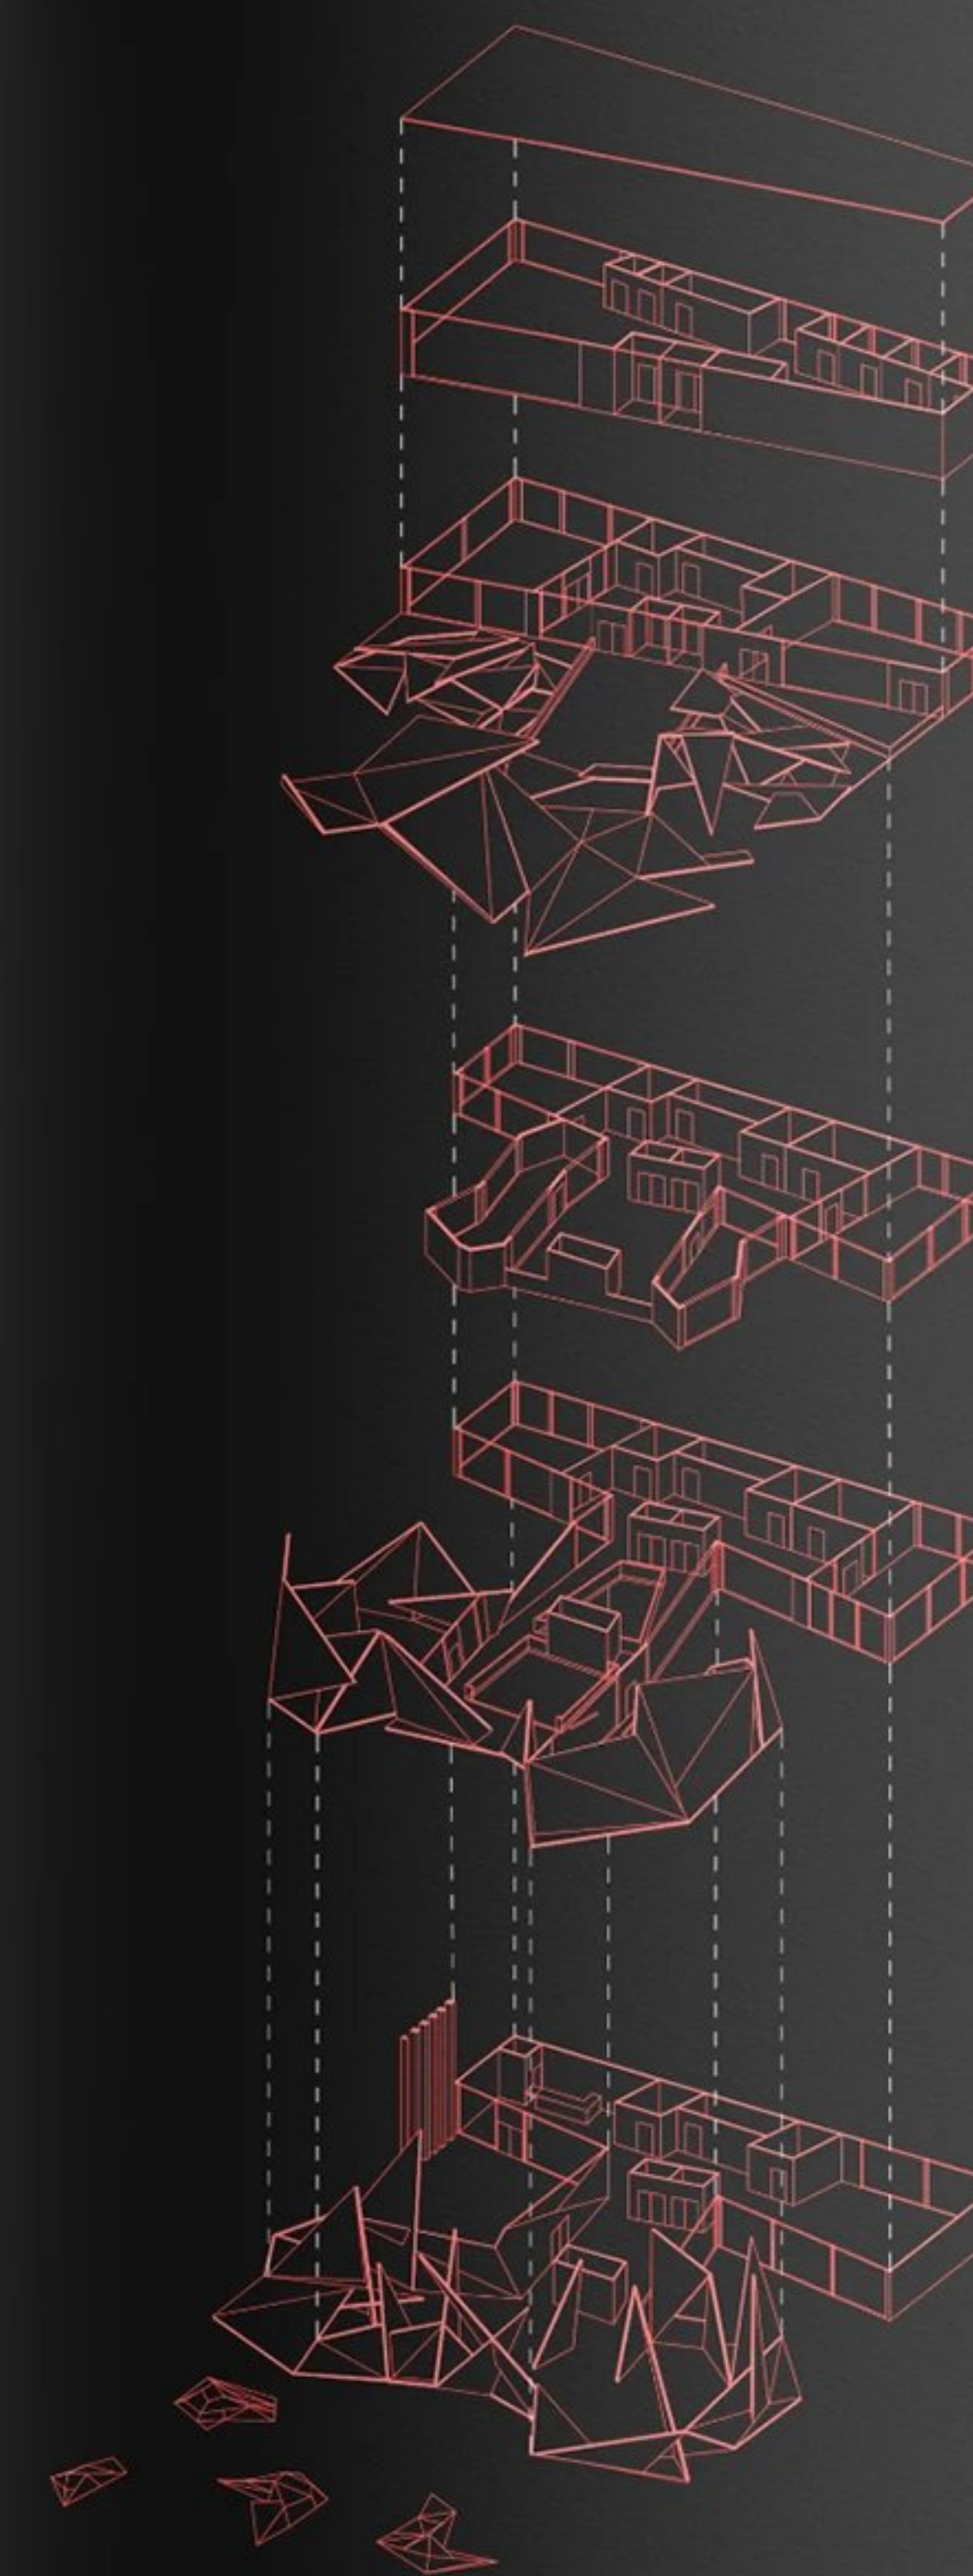

URBAN SECTION BB
SCALE 1:200

Artistic Renders

