

INTERSTITIAL LIVING

DESIGNING CHOICE BETWEEN IMMERSION AND RETREAT

MAYA ABU SAMRA
H00437354

AMPHIBIOUS HOUSING
ARCHITECTURAL DESIGN STUDIO 5

TUTORS
DR HARPREET SETH
ELLI FRAGKAKI
SANMITA PATEL
HAMED HASSANI

2025

THIS PROJECT BEGINS BY LOOKING AT AL FAHIDI NOT THROUGH ITS TOURIST IMAGE BUT THROUGH THE EVERYDAY FRICTION AND STILLNESS THAT DEFINE IT. I WANTED TO UNDERSTAND HOW PEOPLE MOVE, PAUSE, GATHER, AND RETREAT, AND HOW THESE RHYTHMS SHAPE THE IDENTITY OF THE NEIGHBOURHOOD. THE DUALITY DIAGRAM REFLECTS THE CORE STANCE OF THE PROJECT: CREATING A PLACE WHERE INDIVIDUALS CAN CHOOSE BETWEEN IMMERSION IN THE DENSE CULTURAL LIFE OF AL FAHIDI OR RETREAT INTO QUIETER, RESTORATIVE SPACES. THE DESIGN GREW OUT OF THIS TENSION, TREATING ARCHITECTURE AS A MEDIATOR BETWEEN THESE TWO STATES.




ABSTRACT COLLAGE

FELT

COLLAGE MADE USING TEA BAGS, AND LINOPRINTING OF STENCILS CARVED WITH PATTERNS REFLECTING CALM, OR CHAOS, OBSERVED AT AL FAHIDI.



THE LIVED DRAWINGS MAP THE SENSORY WEIGHT OF THE SITE. THEY GREW OUT OF WALKING, WAITING, LISTENING, AND NOTICING THE SMALL MOMENTS THAT OFTEN GO UNRECORDED. THESE IMPRESSIONS SHOWED ME WHERE THE NEIGHBOURHOOD INTENSIFIES AND WHERE IT SOFTENS.



THE FELT COLLAGE WAS MORE PERSONAL. IT TRACES HOW THE PLACE SETTLES IN THE BODY, THE ABRUPT SHIFTS IN LIGHT, THE TIGHT PASSAGES THAT PUSH YOU FORWARD, THE RARE POCKETS OF OPENNESS THAT LET YOU BREATHE. TOGETHER, THEY BECAME THE EMOTIONAL GROUND OF THE PROJECT AND THE FIRST LAYER OF ITS ARCHITECTURAL LANGUAGE.

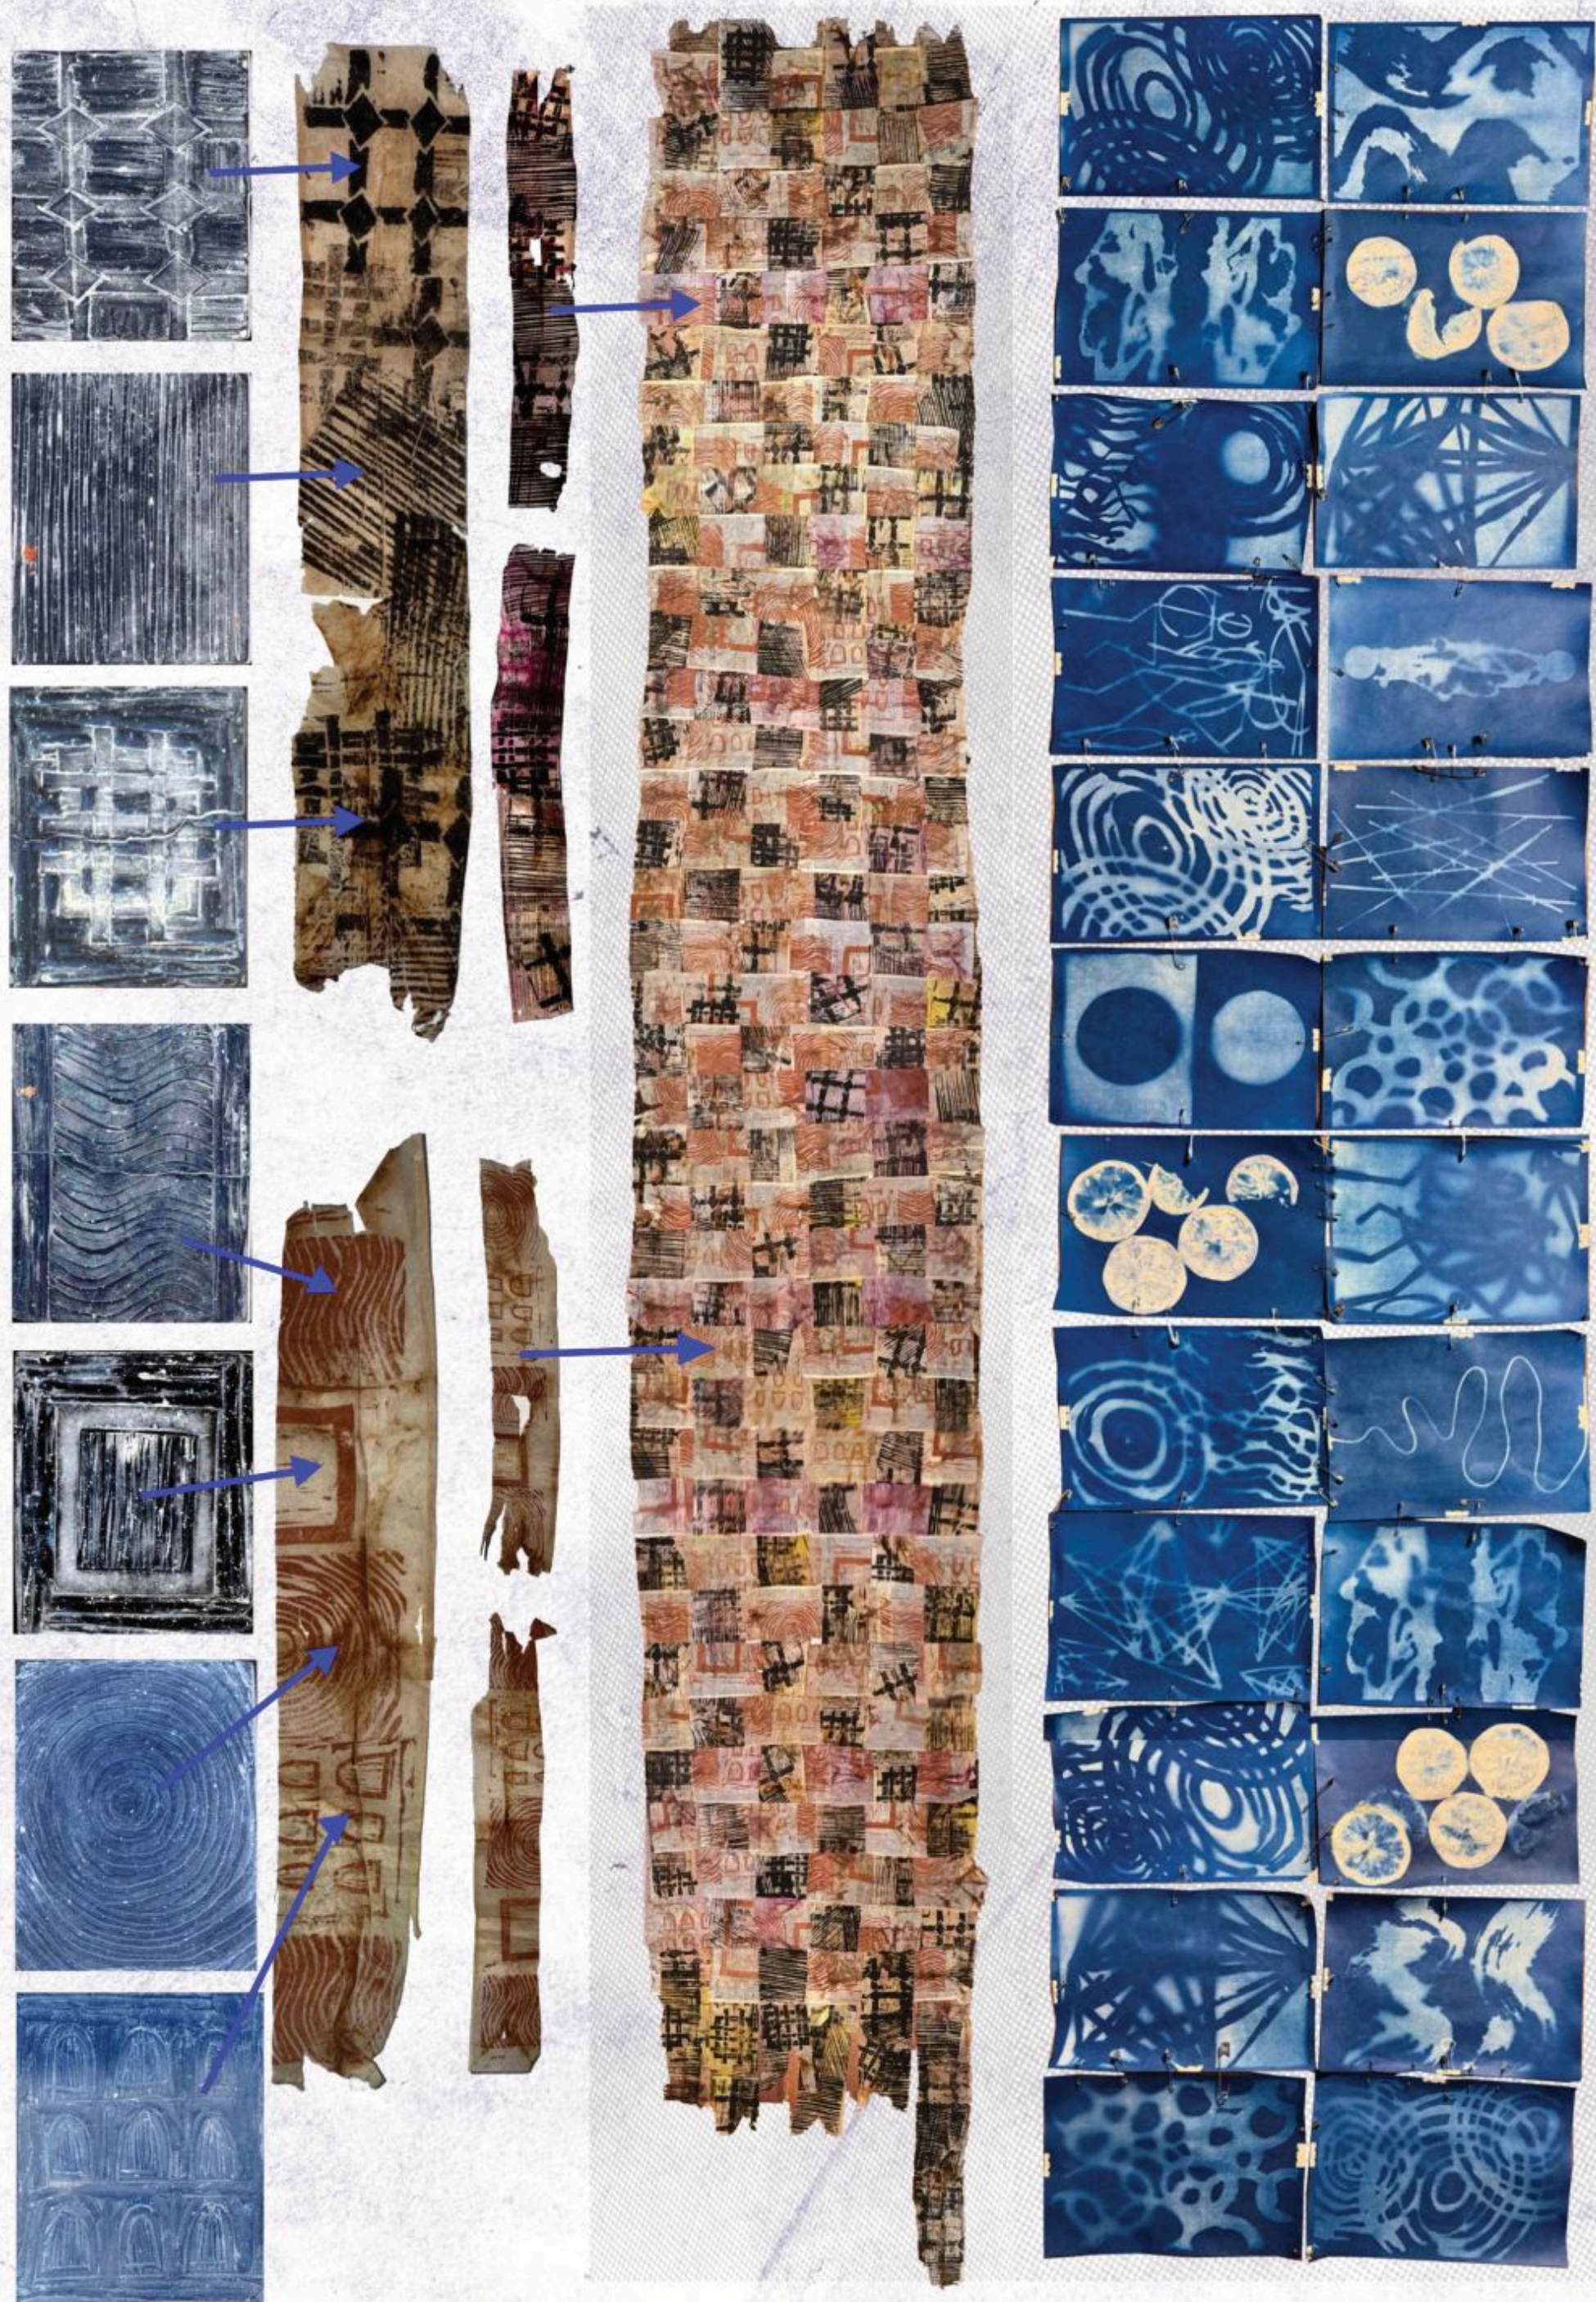

LIVED


STENCILS MADE USING SKETCHES SCANNED AND DIGITALLY MANIPULATED. COLLAGE DONE USING CYNOPRINTING.

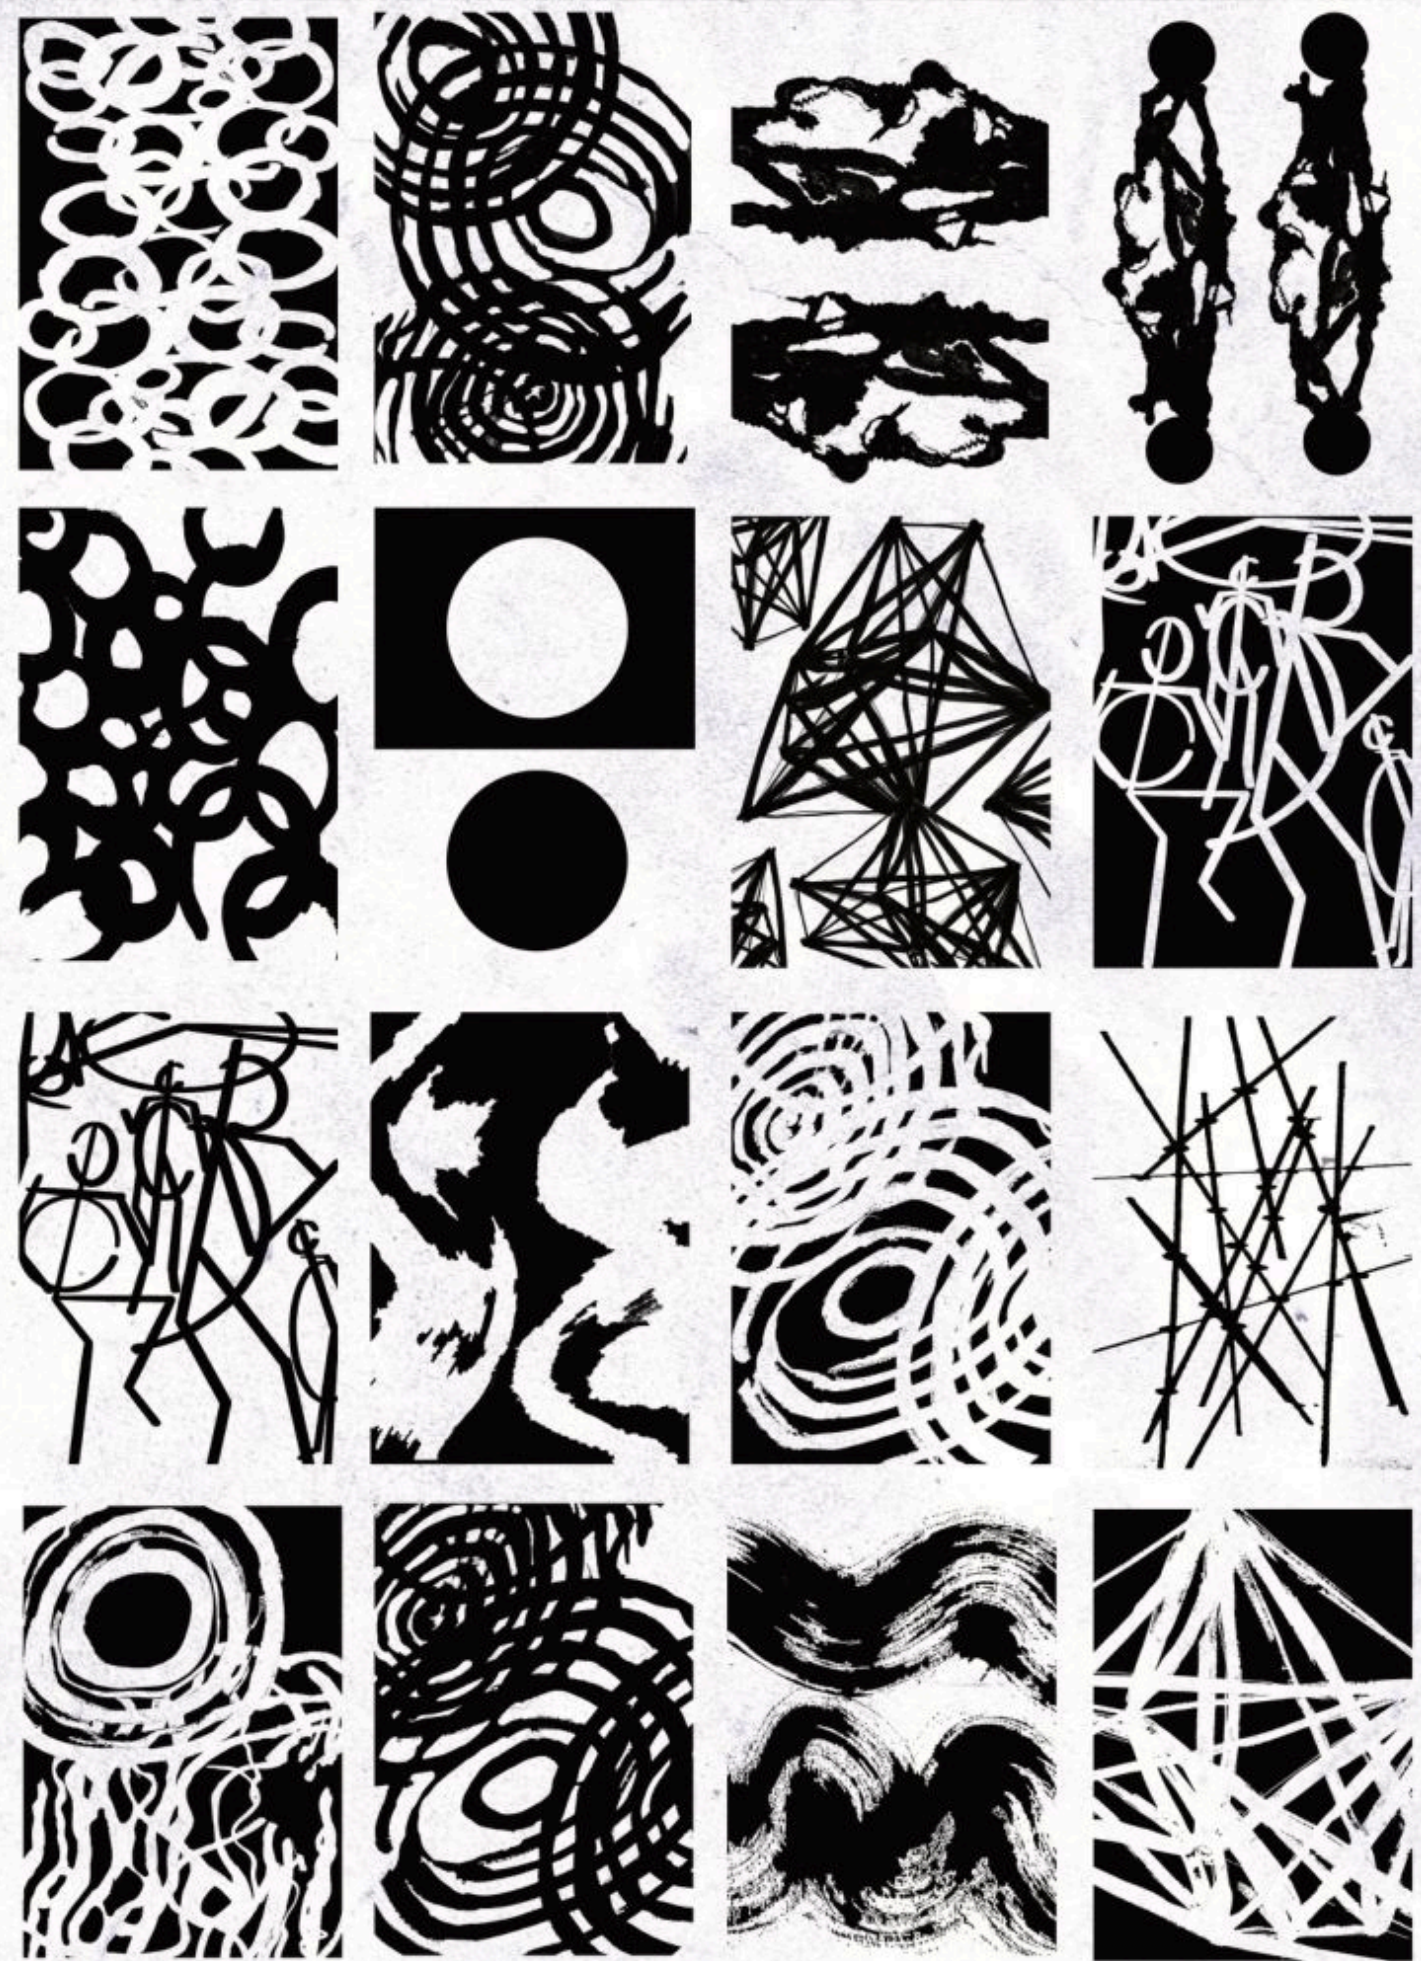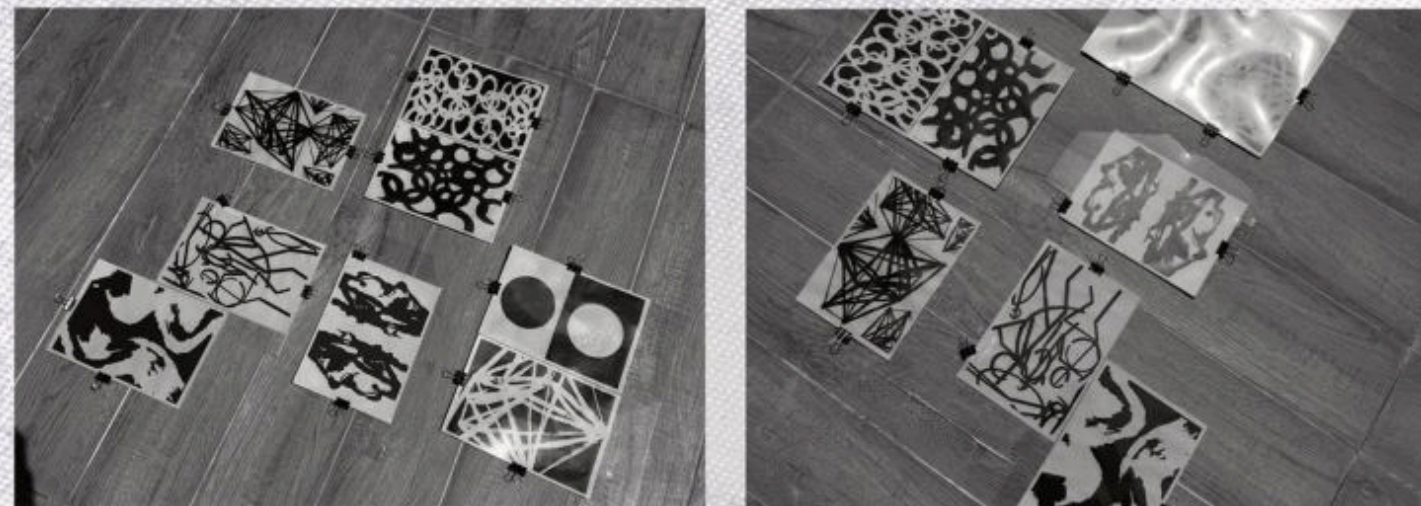

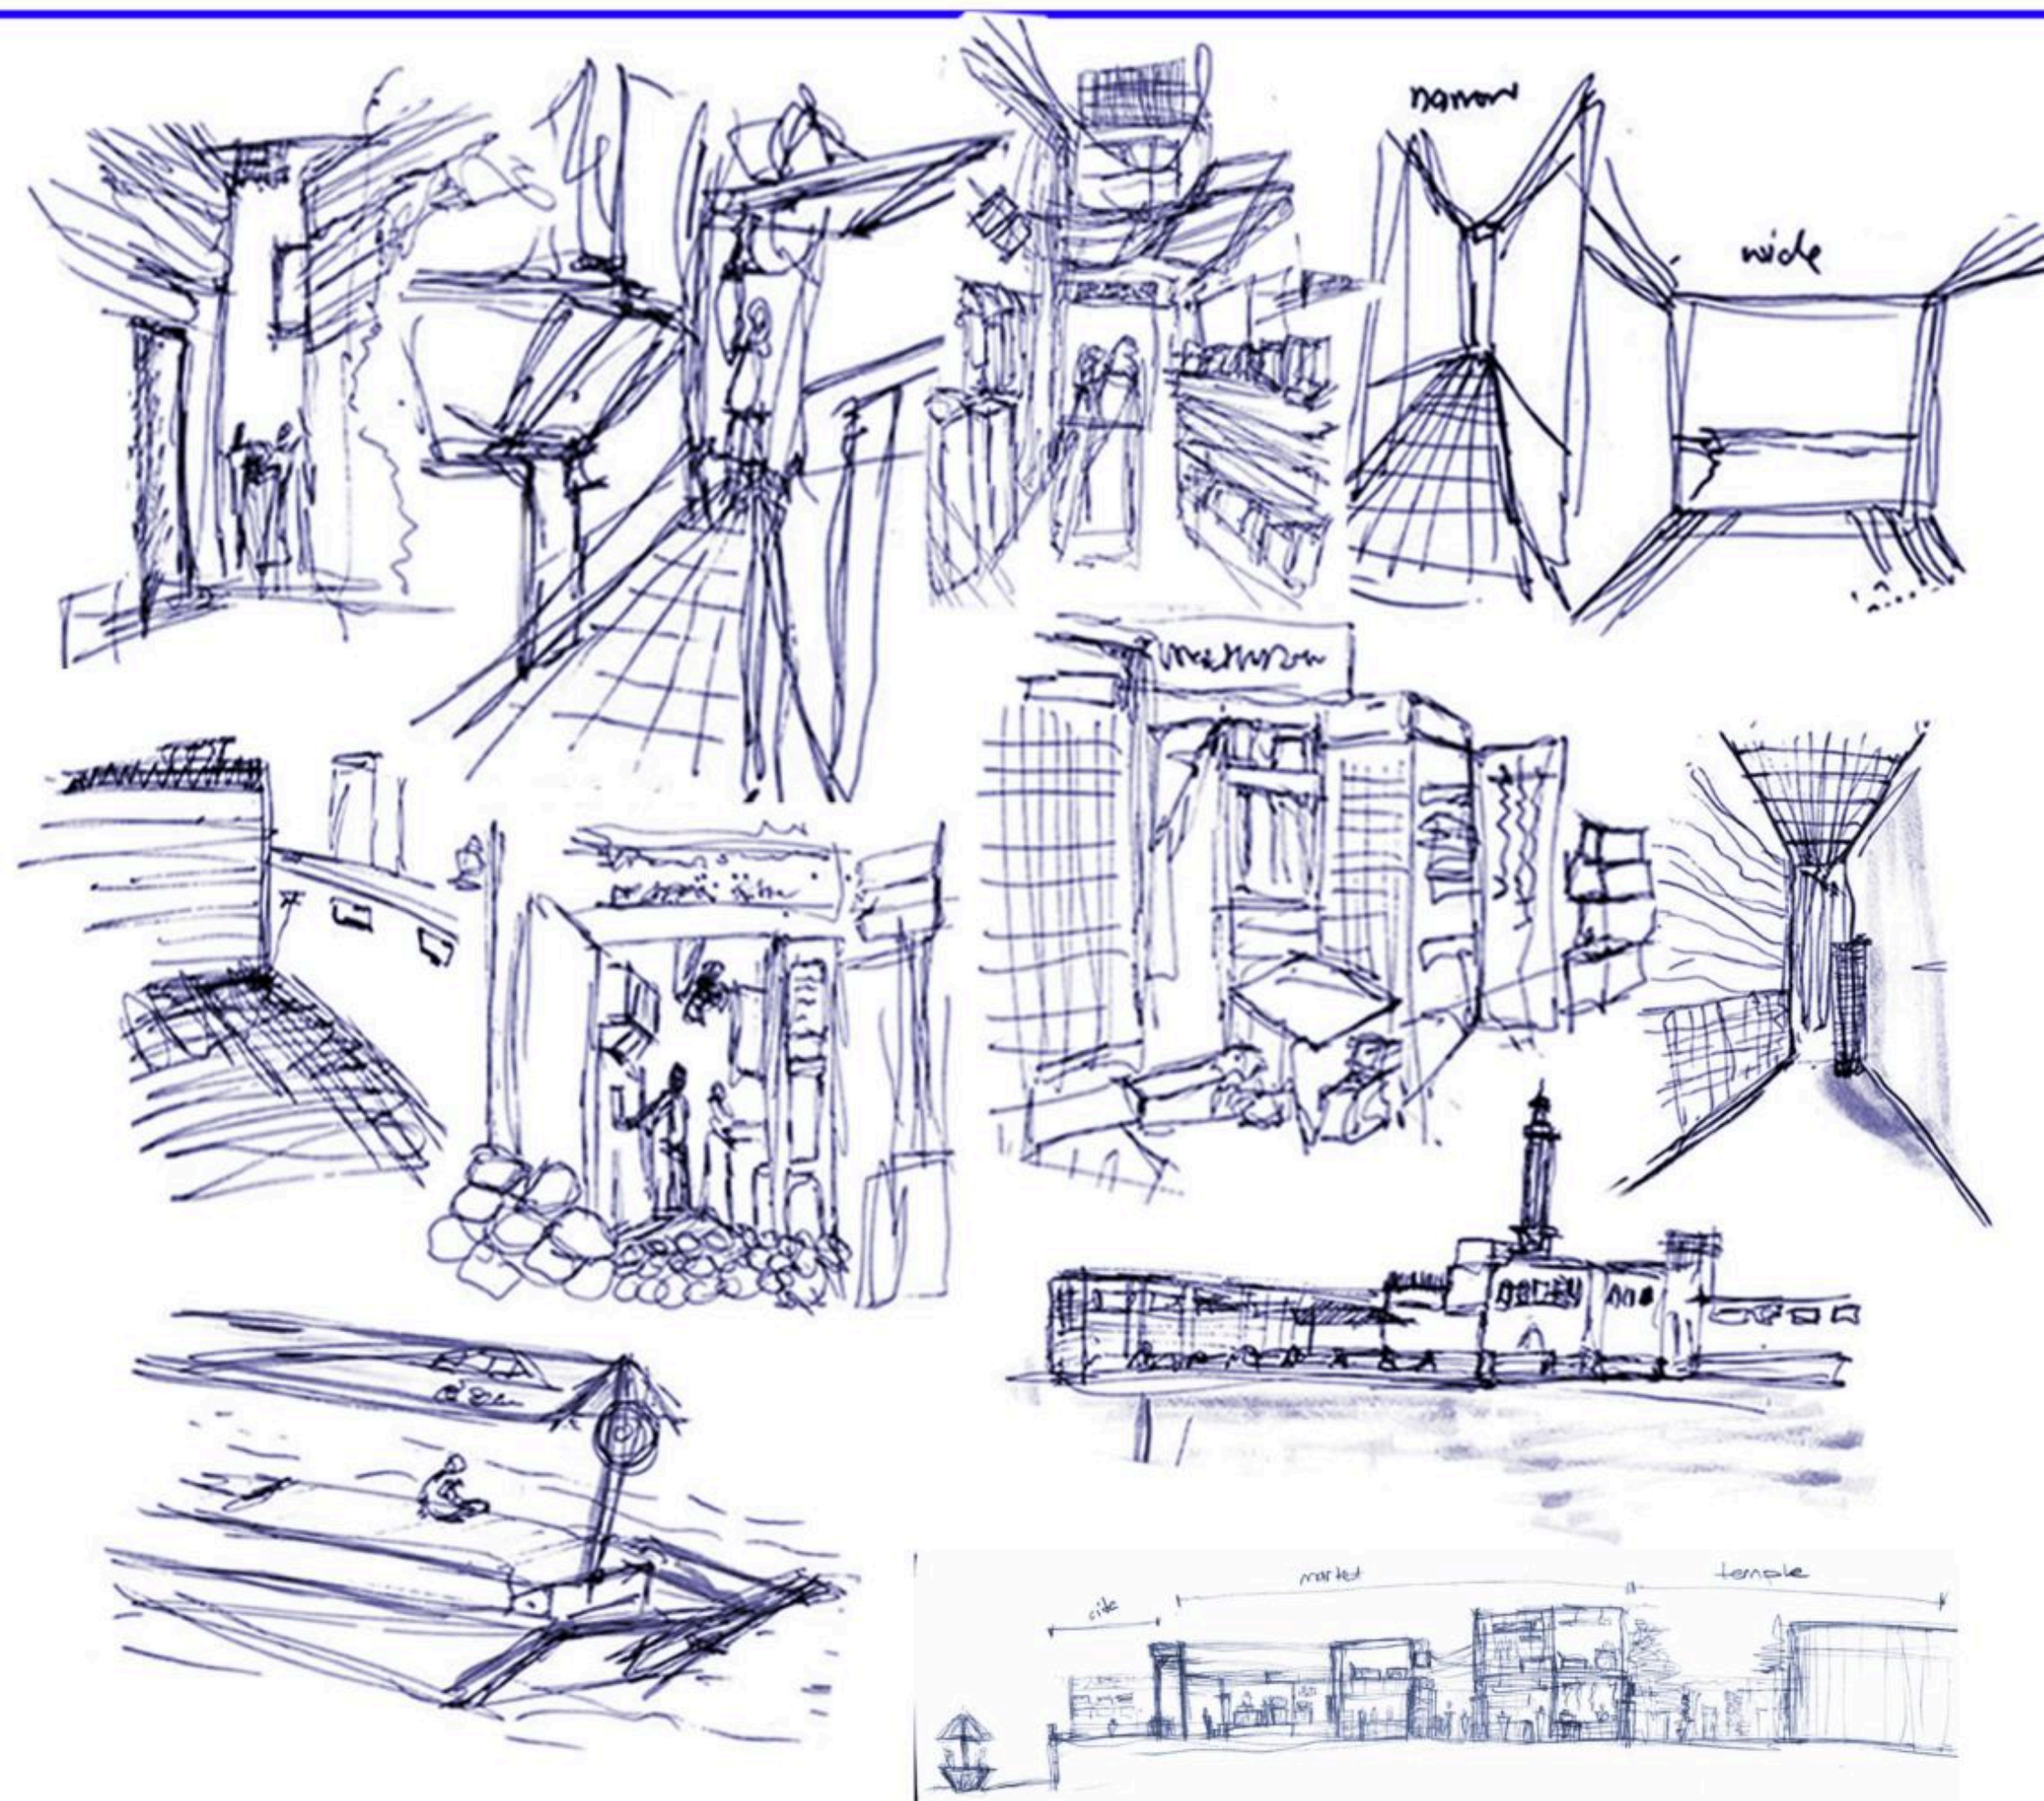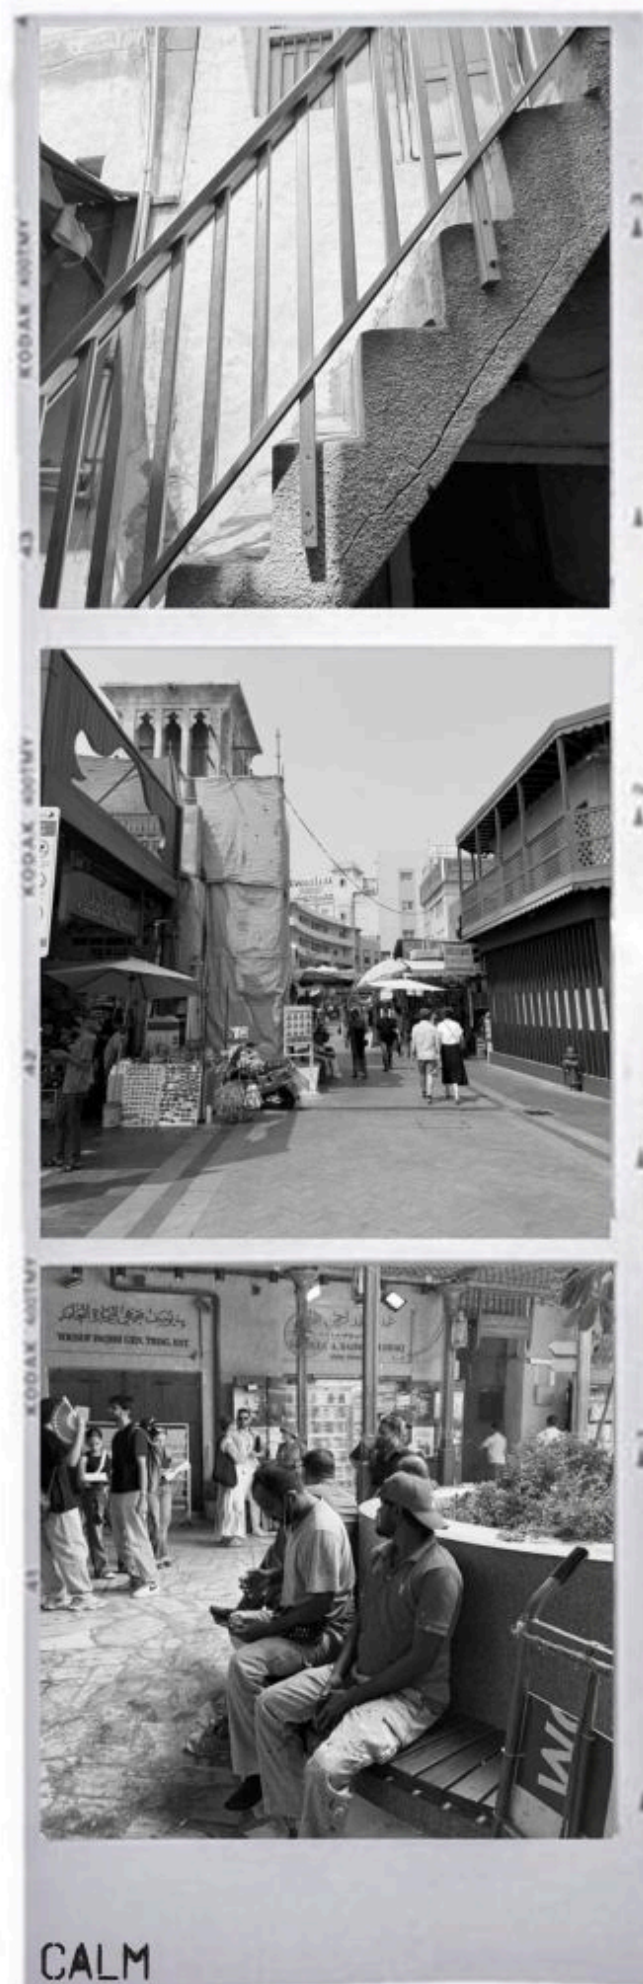


DURING THE SITE VISIT, THE ABRUPTNESS OF AL FAHIDI BECAME IMPOSSIBLE TO IGNORE. SPACES TIGHTENED WITHOUT WARNING, LIGHT SHIFTED SUDDENLY, AND THE ATMOSPHERE CHANGED FROM CALM TO CROWDED IN A SINGLE STEP. INSTEAD OF SMOOTHING THESE TRANSITIONS OUT, I BEGAN TO SEE VALUE IN THEM. THE SKETCHES AND PHOTOGRAPHS ON THIS PAGE CAPTURE THAT RAW IMMEDIACY. THEY HELPED ME UNDERSTAND THAT THE PROJECT SHOULDN'T ALTER THE SITE BUT WORK WITH ITS SHARP EDGES, LETTING THOSE SHIFTS IN SCALE AND MOOD BECOME PART OF THE ARCHITECTURAL EXPERIENCE.

DUBAI, UAE

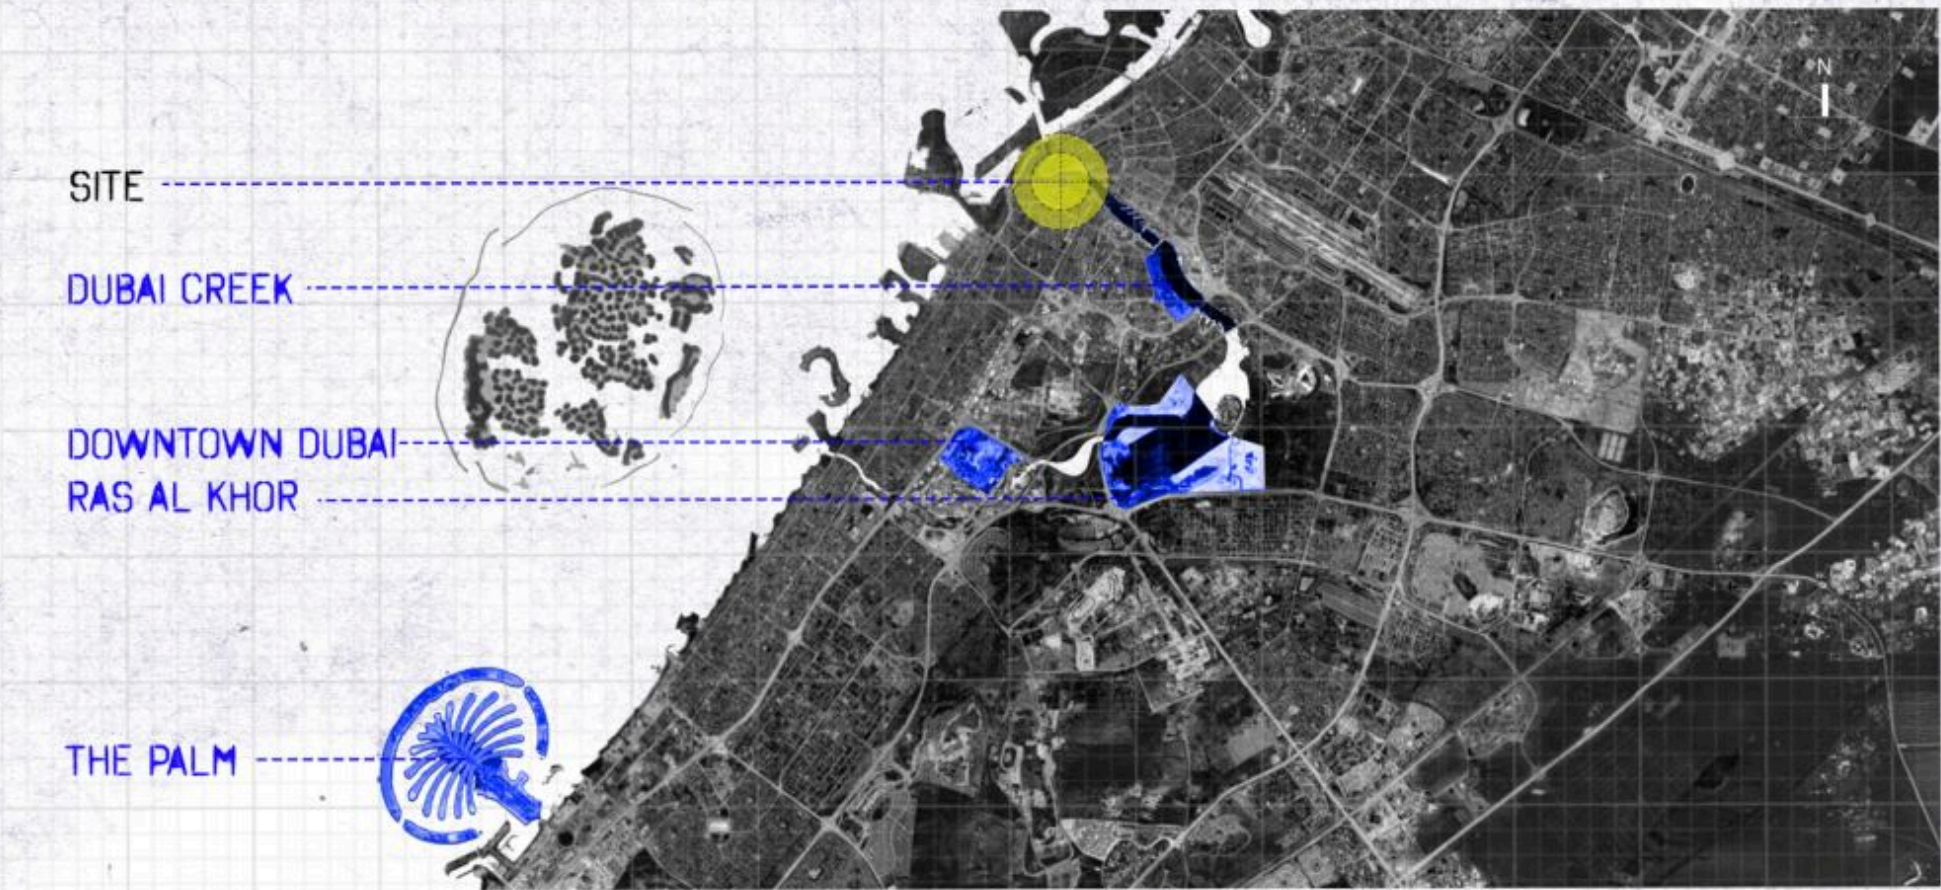


DUBAI CREEK HISTORY

ONCE THE CITY'S LIFELINE, THE CREEK SHAPED DUBAI'S EARLIEST SETTLEMENTS, TRADE, AND CULTURE. OVER TIME, ITS EDGE TRANSFORMED FROM SAND AND SAIL TO CONCRETE AND SKYLINE. YET ITS ESSENCE ENDURES. THE CREEK REMAINS A THRESHOLD BETWEEN PAST AND PRESENT, STILL CARRYING THE RHYTHM OF EXCHANGE, MOVEMENT, AND BELONGING THAT BUILT THE CITY.

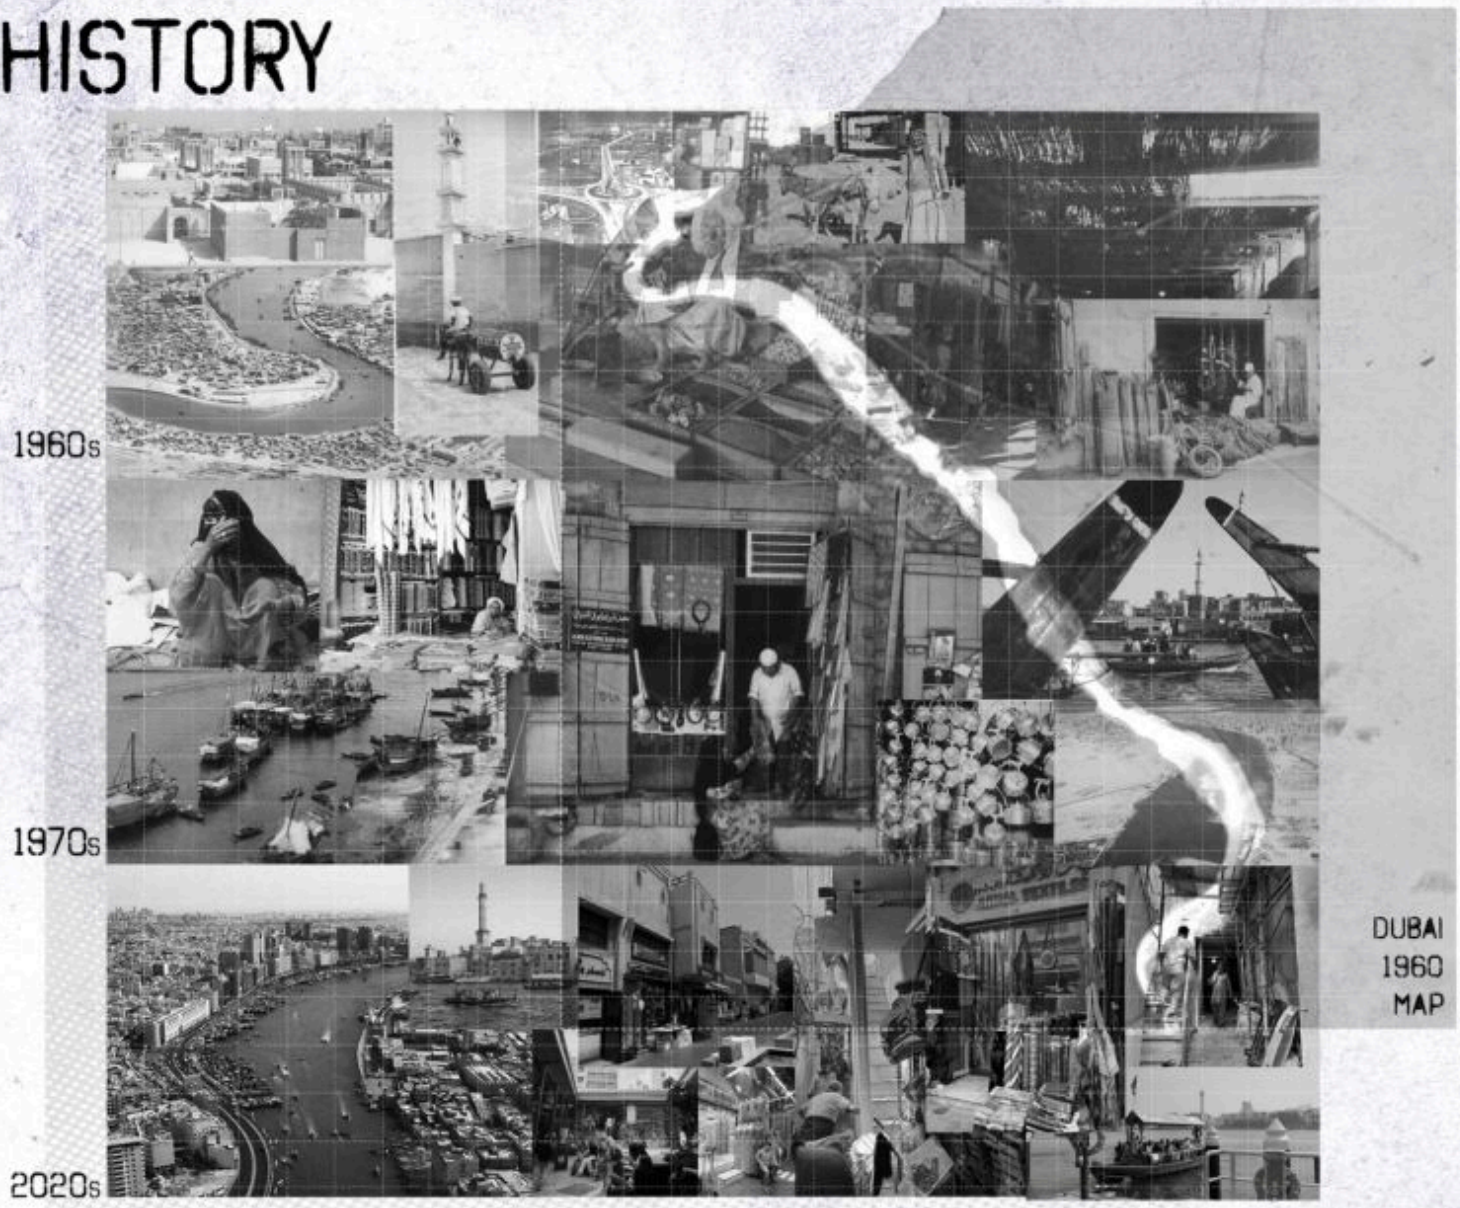

DUBAI CREEK, DUBAI


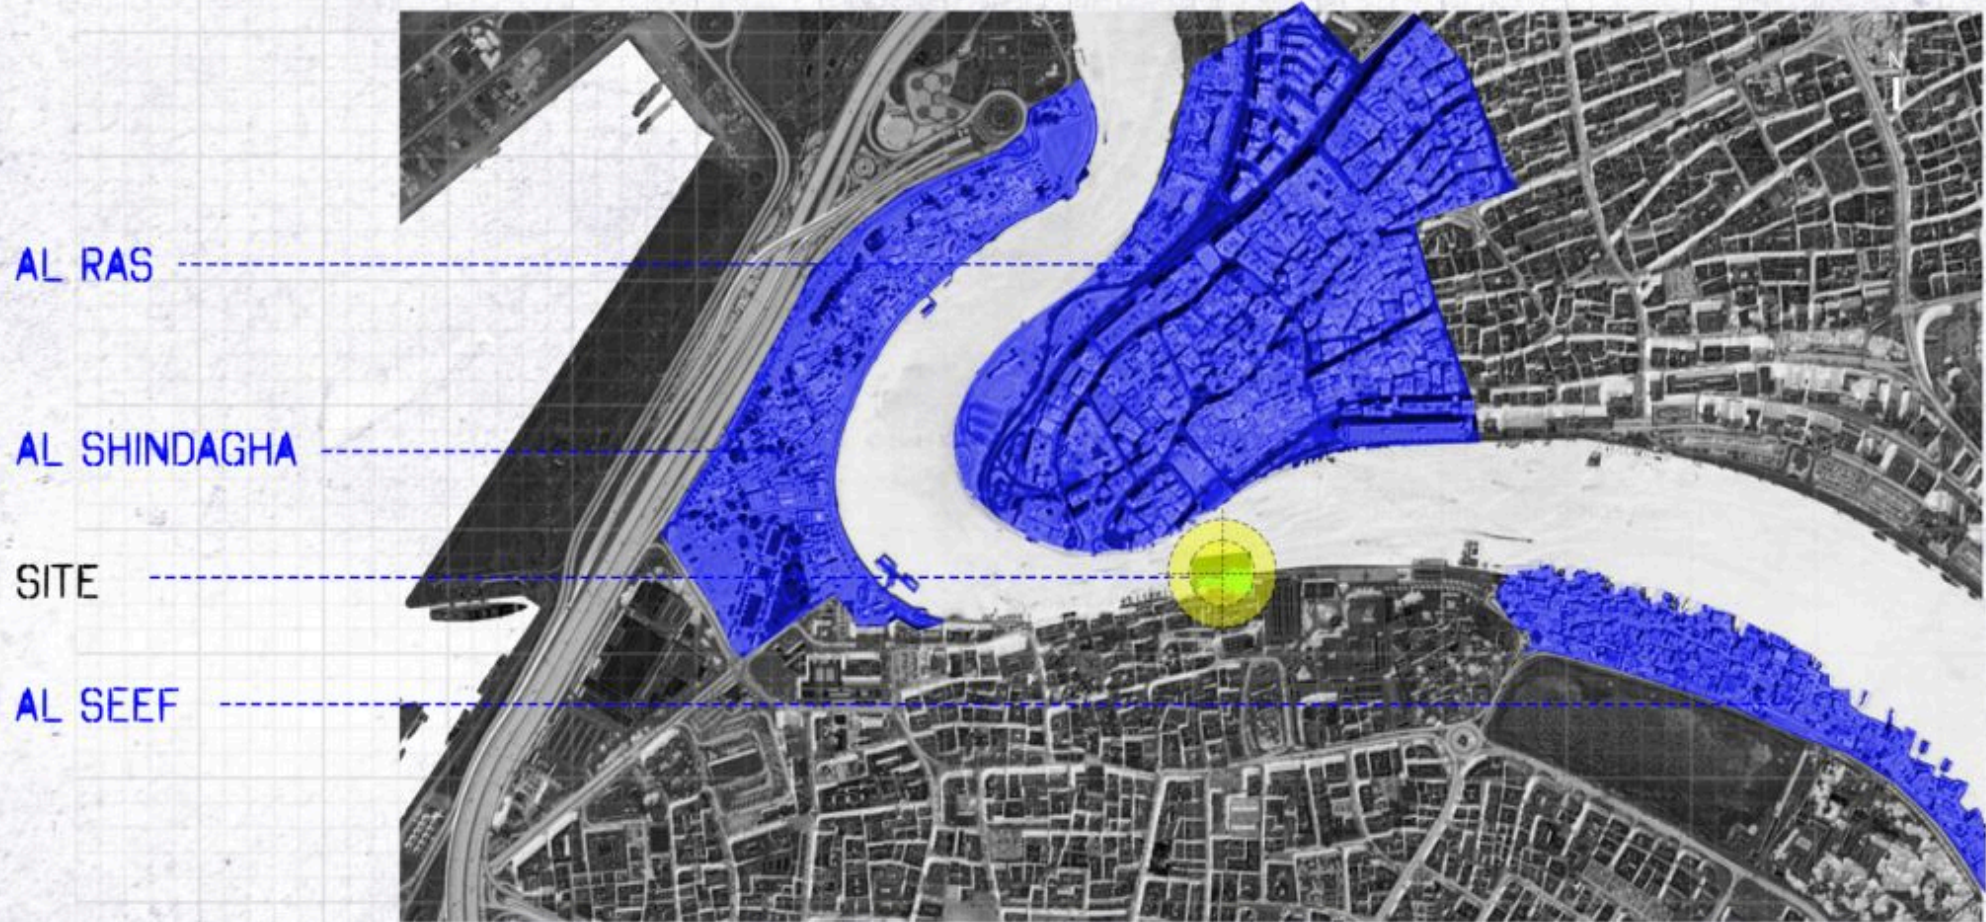


AL FAHIDI, DUBAI



DEMOGRAPHIC

COMMERCIAL - RESIDENTIAL - CULTURAL OVERLAP

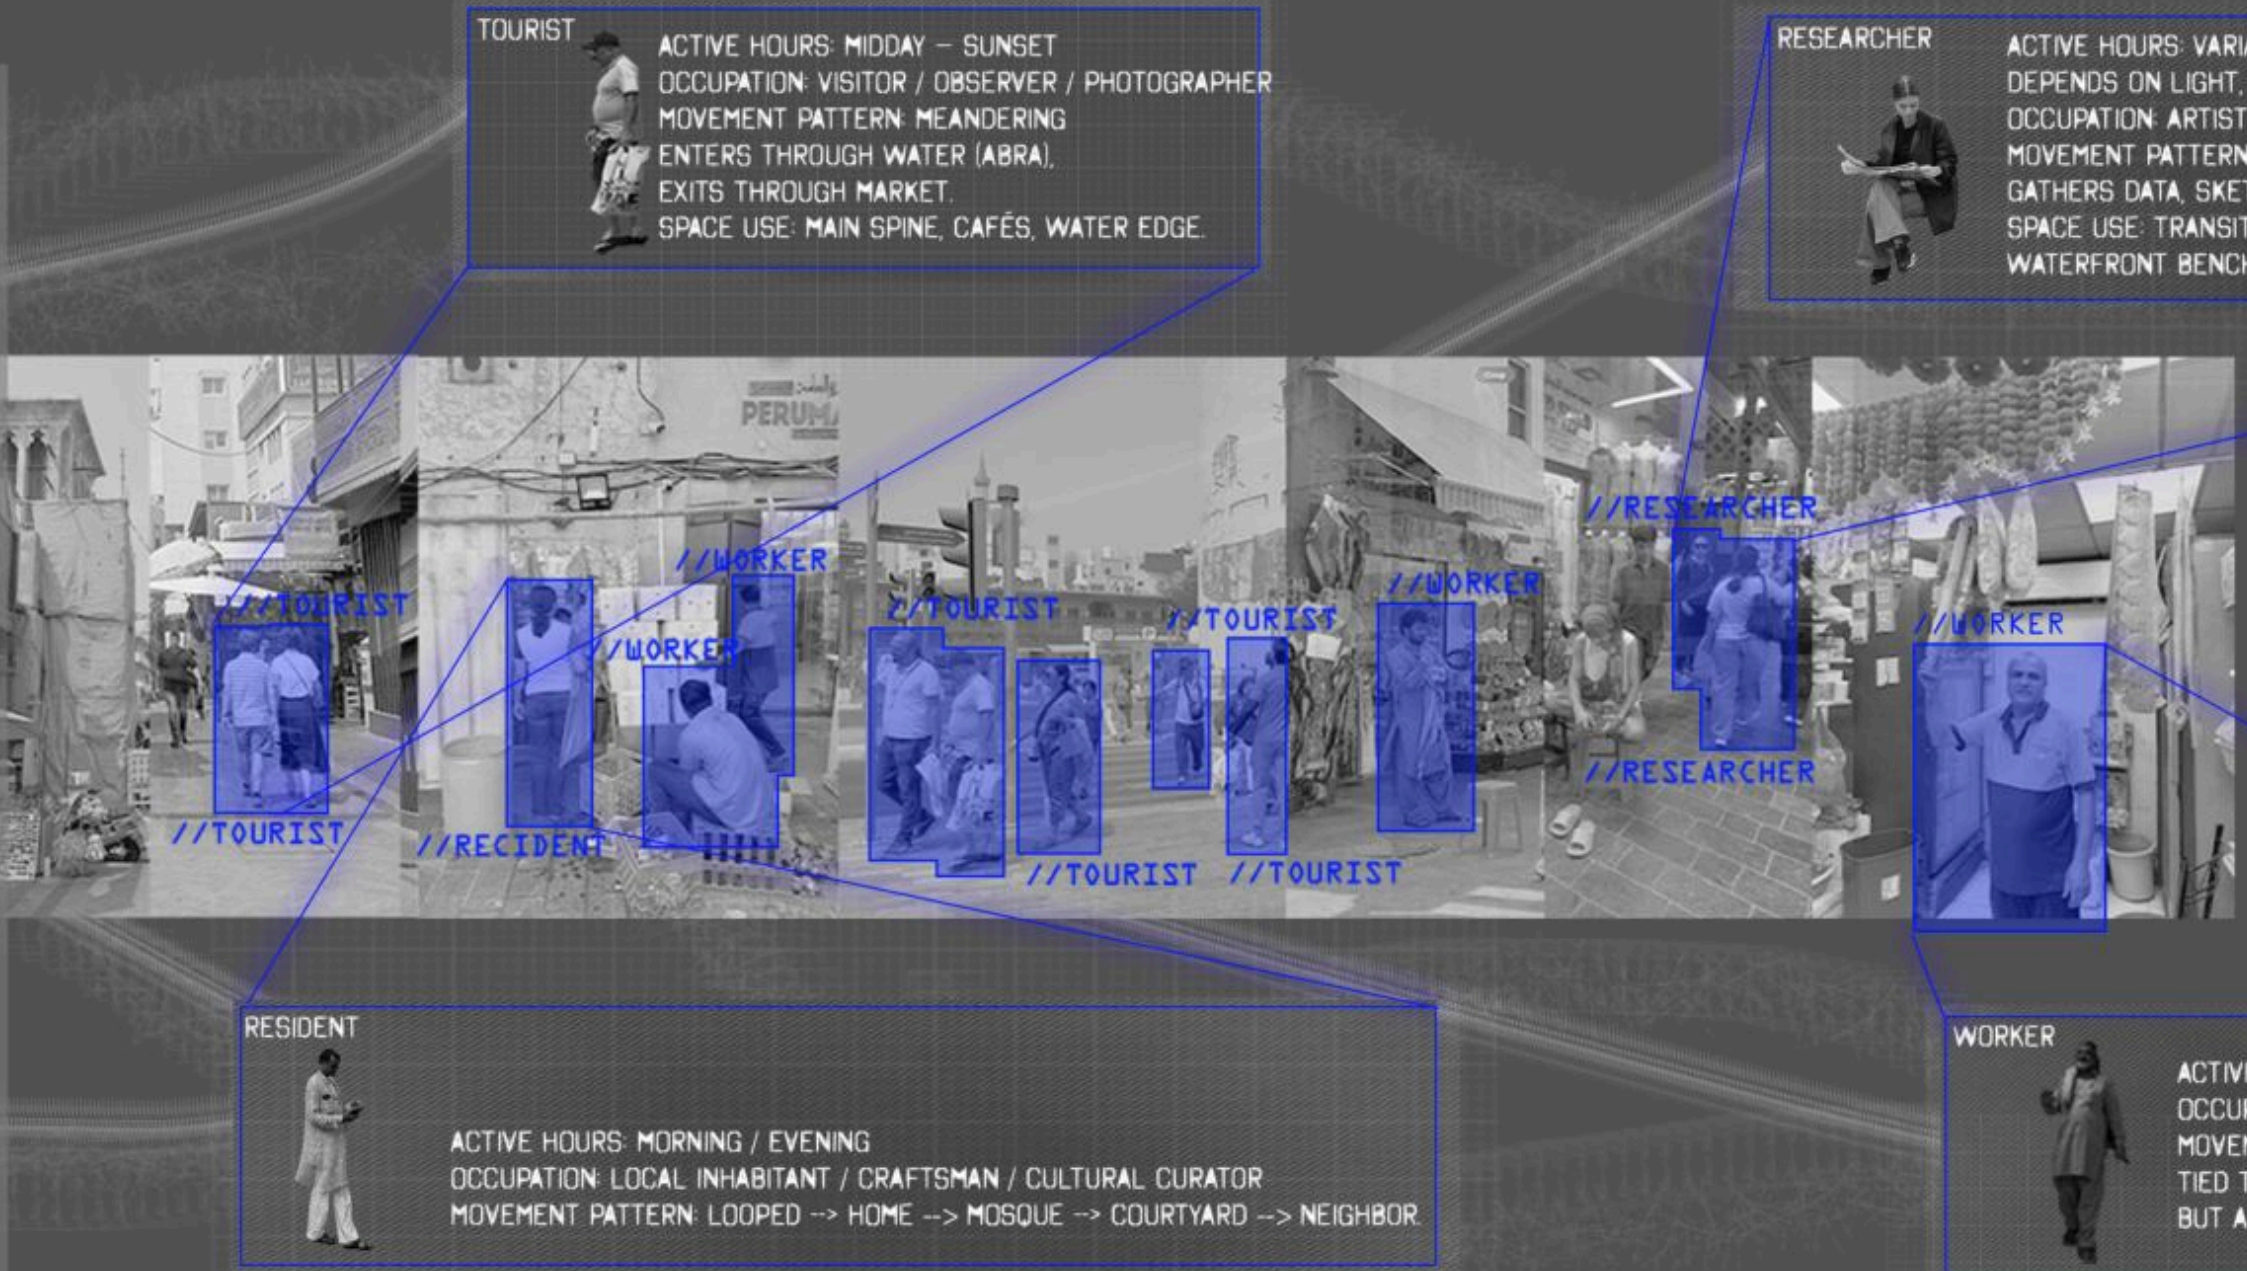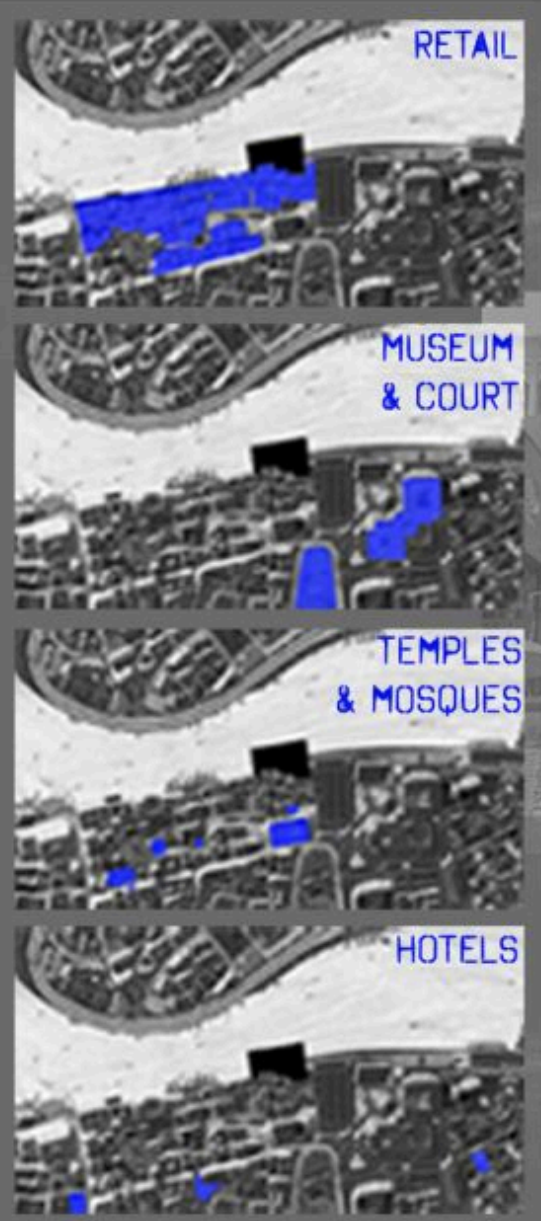

TOURIST
ACTIVE HOURS: MIDDAY – SUNSET
OCCUPATION: VISITOR / OBSERVER / PHOTOGRAPHER
MOVEMENT PATTERN: MEANDERING
ENTERS THROUGH WATER (ABRA),
EXITS THROUGH MARKET.
SPACE USE: MAIN SPINE, CAFÉS, WATER EDGE.


RESEARCHER
ACTIVE HOURS: VARIABLE
DEPENDS ON LIGHT, EVENT, OR SOCIAL RHYTHM.
OCCUPATION: ARTIST / STUDENT / BIOLOGIST / CULTURAL OBSERVER
MOVEMENT PATTERN: FRAGMENTED
GATHERS DATA, SKETCHES, RECORDS, THEN RETREATS.
SPACE USE: TRANSITIONAL VOIDS, SHADED CORNERS,
WATERFRONT BENCHES.

RESIDENT
ACTIVE HOURS: MORNING / EVENING
OCCUPATION: LOCAL INHABITANT / CRAFTSMAN / CULTURAL CURATOR
MOVEMENT PATTERN: LOOPED --> HOME --> MOSQUE --> COURTYARD --> NEIGHBOR.

WORKER
ACTIVE HOURS: DAWN – LATE EVENING
OCCUPATION: SHOPKEEPER / LABORER / DELIVERY
MOVEMENT PATTERN: STATIC YET RHYTHMIC
TIED TO ONE STALL,
BUT ALWAYS IN MOTION WITHIN IT.

HYBRID USE OF SPACE


GATHERING SPACE

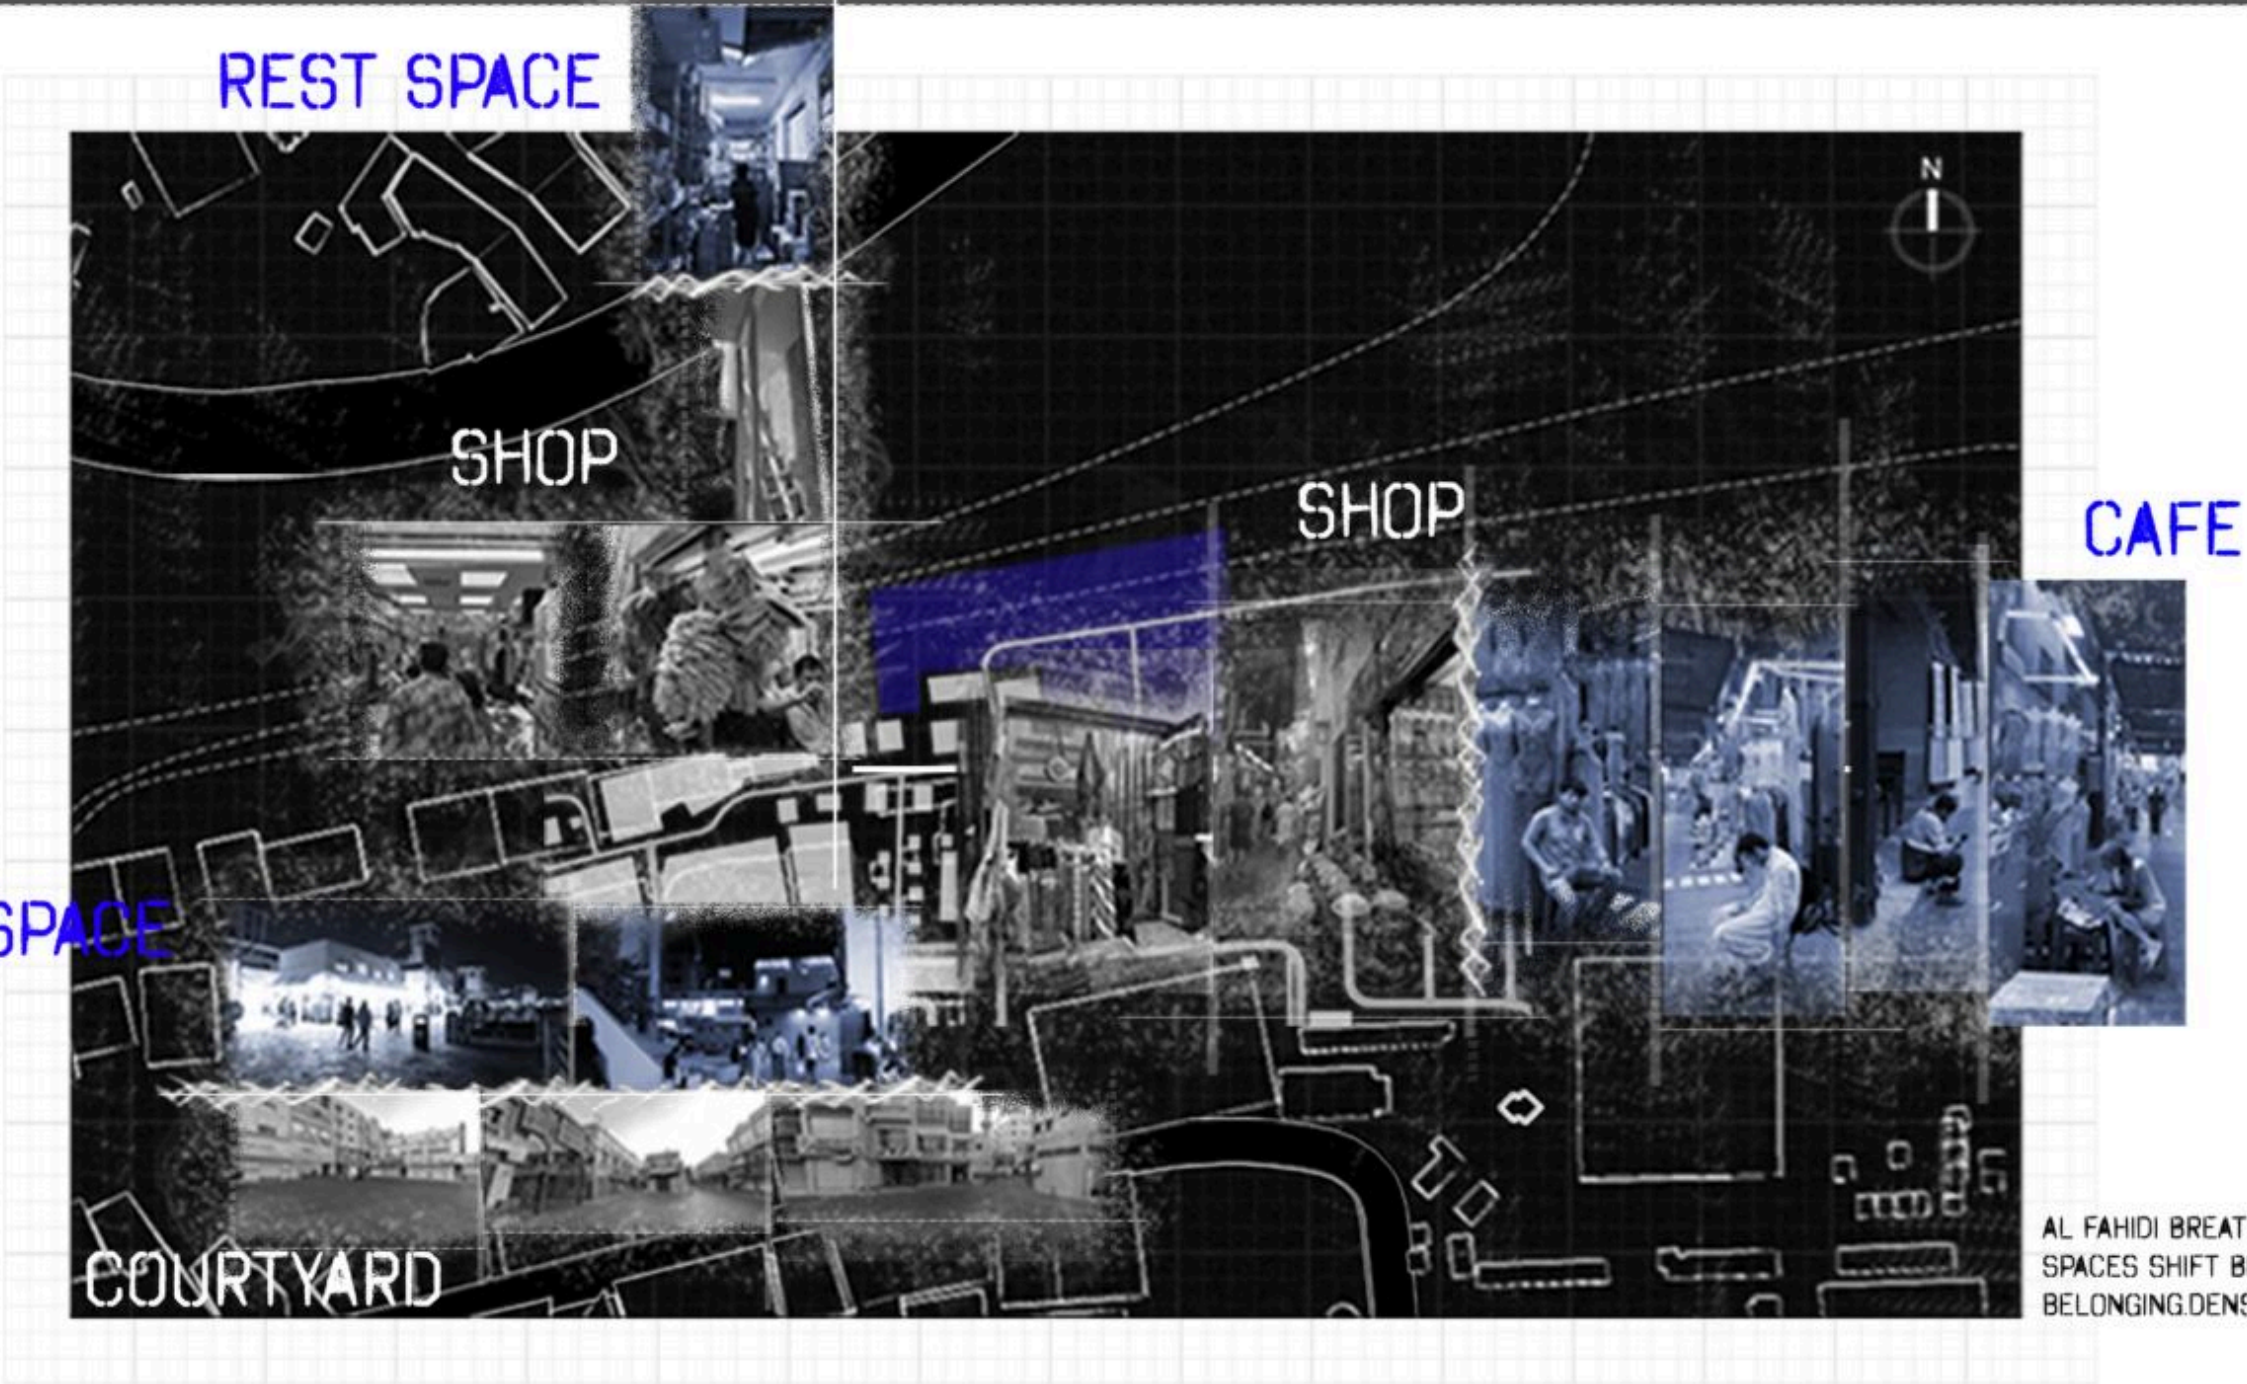


AL FAHIDI HOLDS A MIX OF RESIDENTS, WORKERS, AND VISITORS, CREATING OVERLAPPING PATTERNS OF USE THROUGHOUT THE DAY. THESE LAYERS HELPED DEFINE MY DESIGN DIRECTION, ESPECIALLY THE NEED TO PROVIDE MOMENTS OF REST WITHIN A NEIGHBOURHOOD THAT CAN FEEL PHYSICALLY AND SOCIALLY DENSE. THE HYBRID SPACES, CAFÉS, WORKSHOPS, COURTYARDS, AND NARROW PASSAGES, GUIDED MY UNDERSTANDING OF HOW ARCHITECTURE HERE MUST SUPPORT BOTH COMMUNITY AND SOLITUDE. THE INSIGHTS ON THIS PAGE FEED DIRECTLY INTO THE PROJECT'S CENTRAL IDEA OF CHOICE BETWEEN IMMERSION AND RETREAT.


AL FAHIDI BREATHES THROUGH BLURRED THRESHOLDS
SPACES SHIFT BETWEEN WORK, LIFE, AND LEISURE AS ACTS OF BELONGING. DENSITY CAUSE DISORIENTATION

CLIMATE AND LANDUSE STUDY

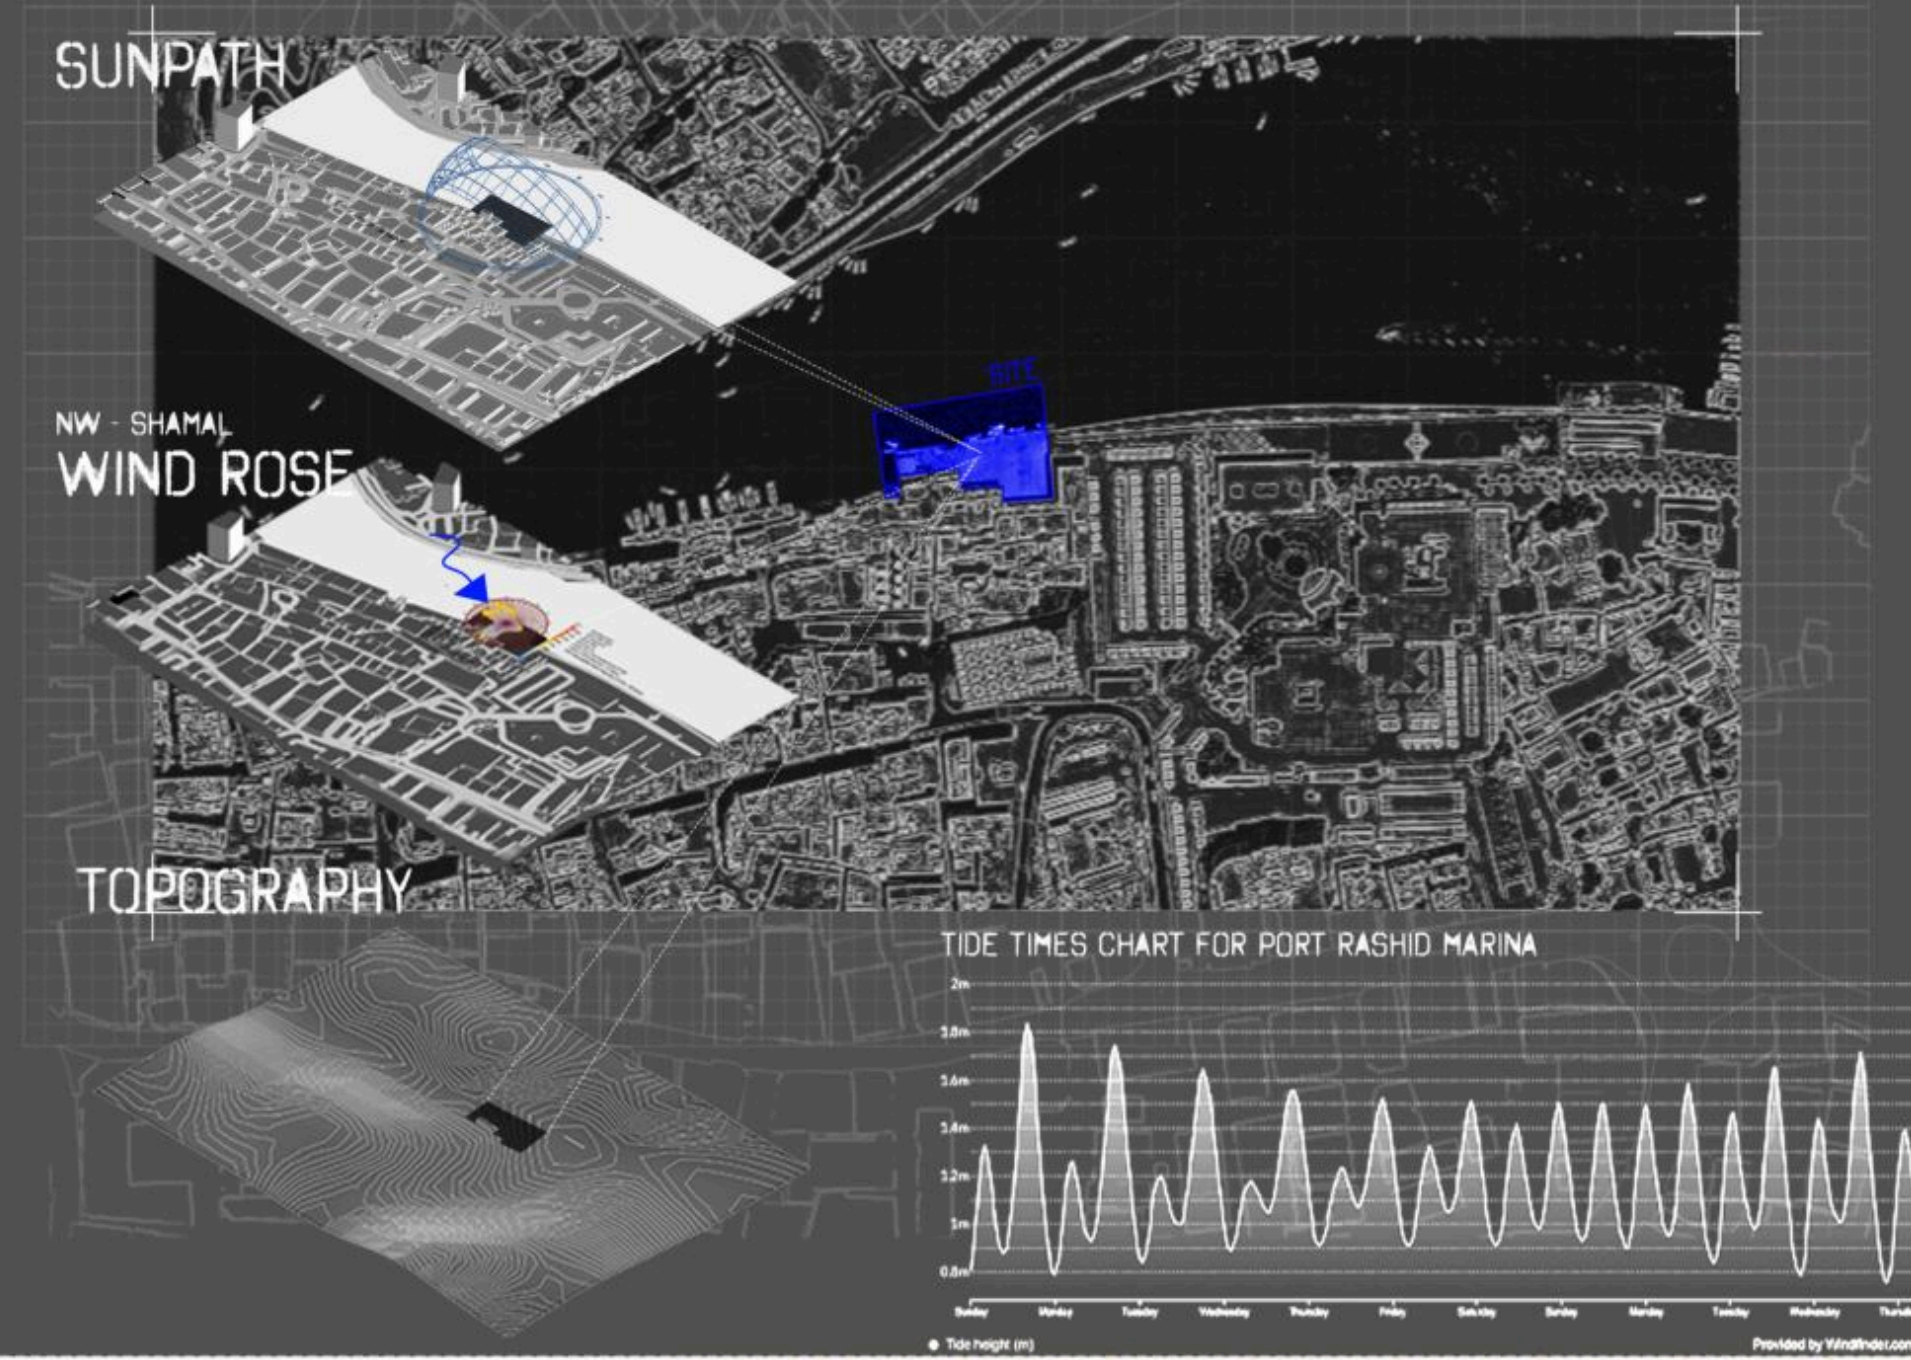

SENSORY OVERLAP

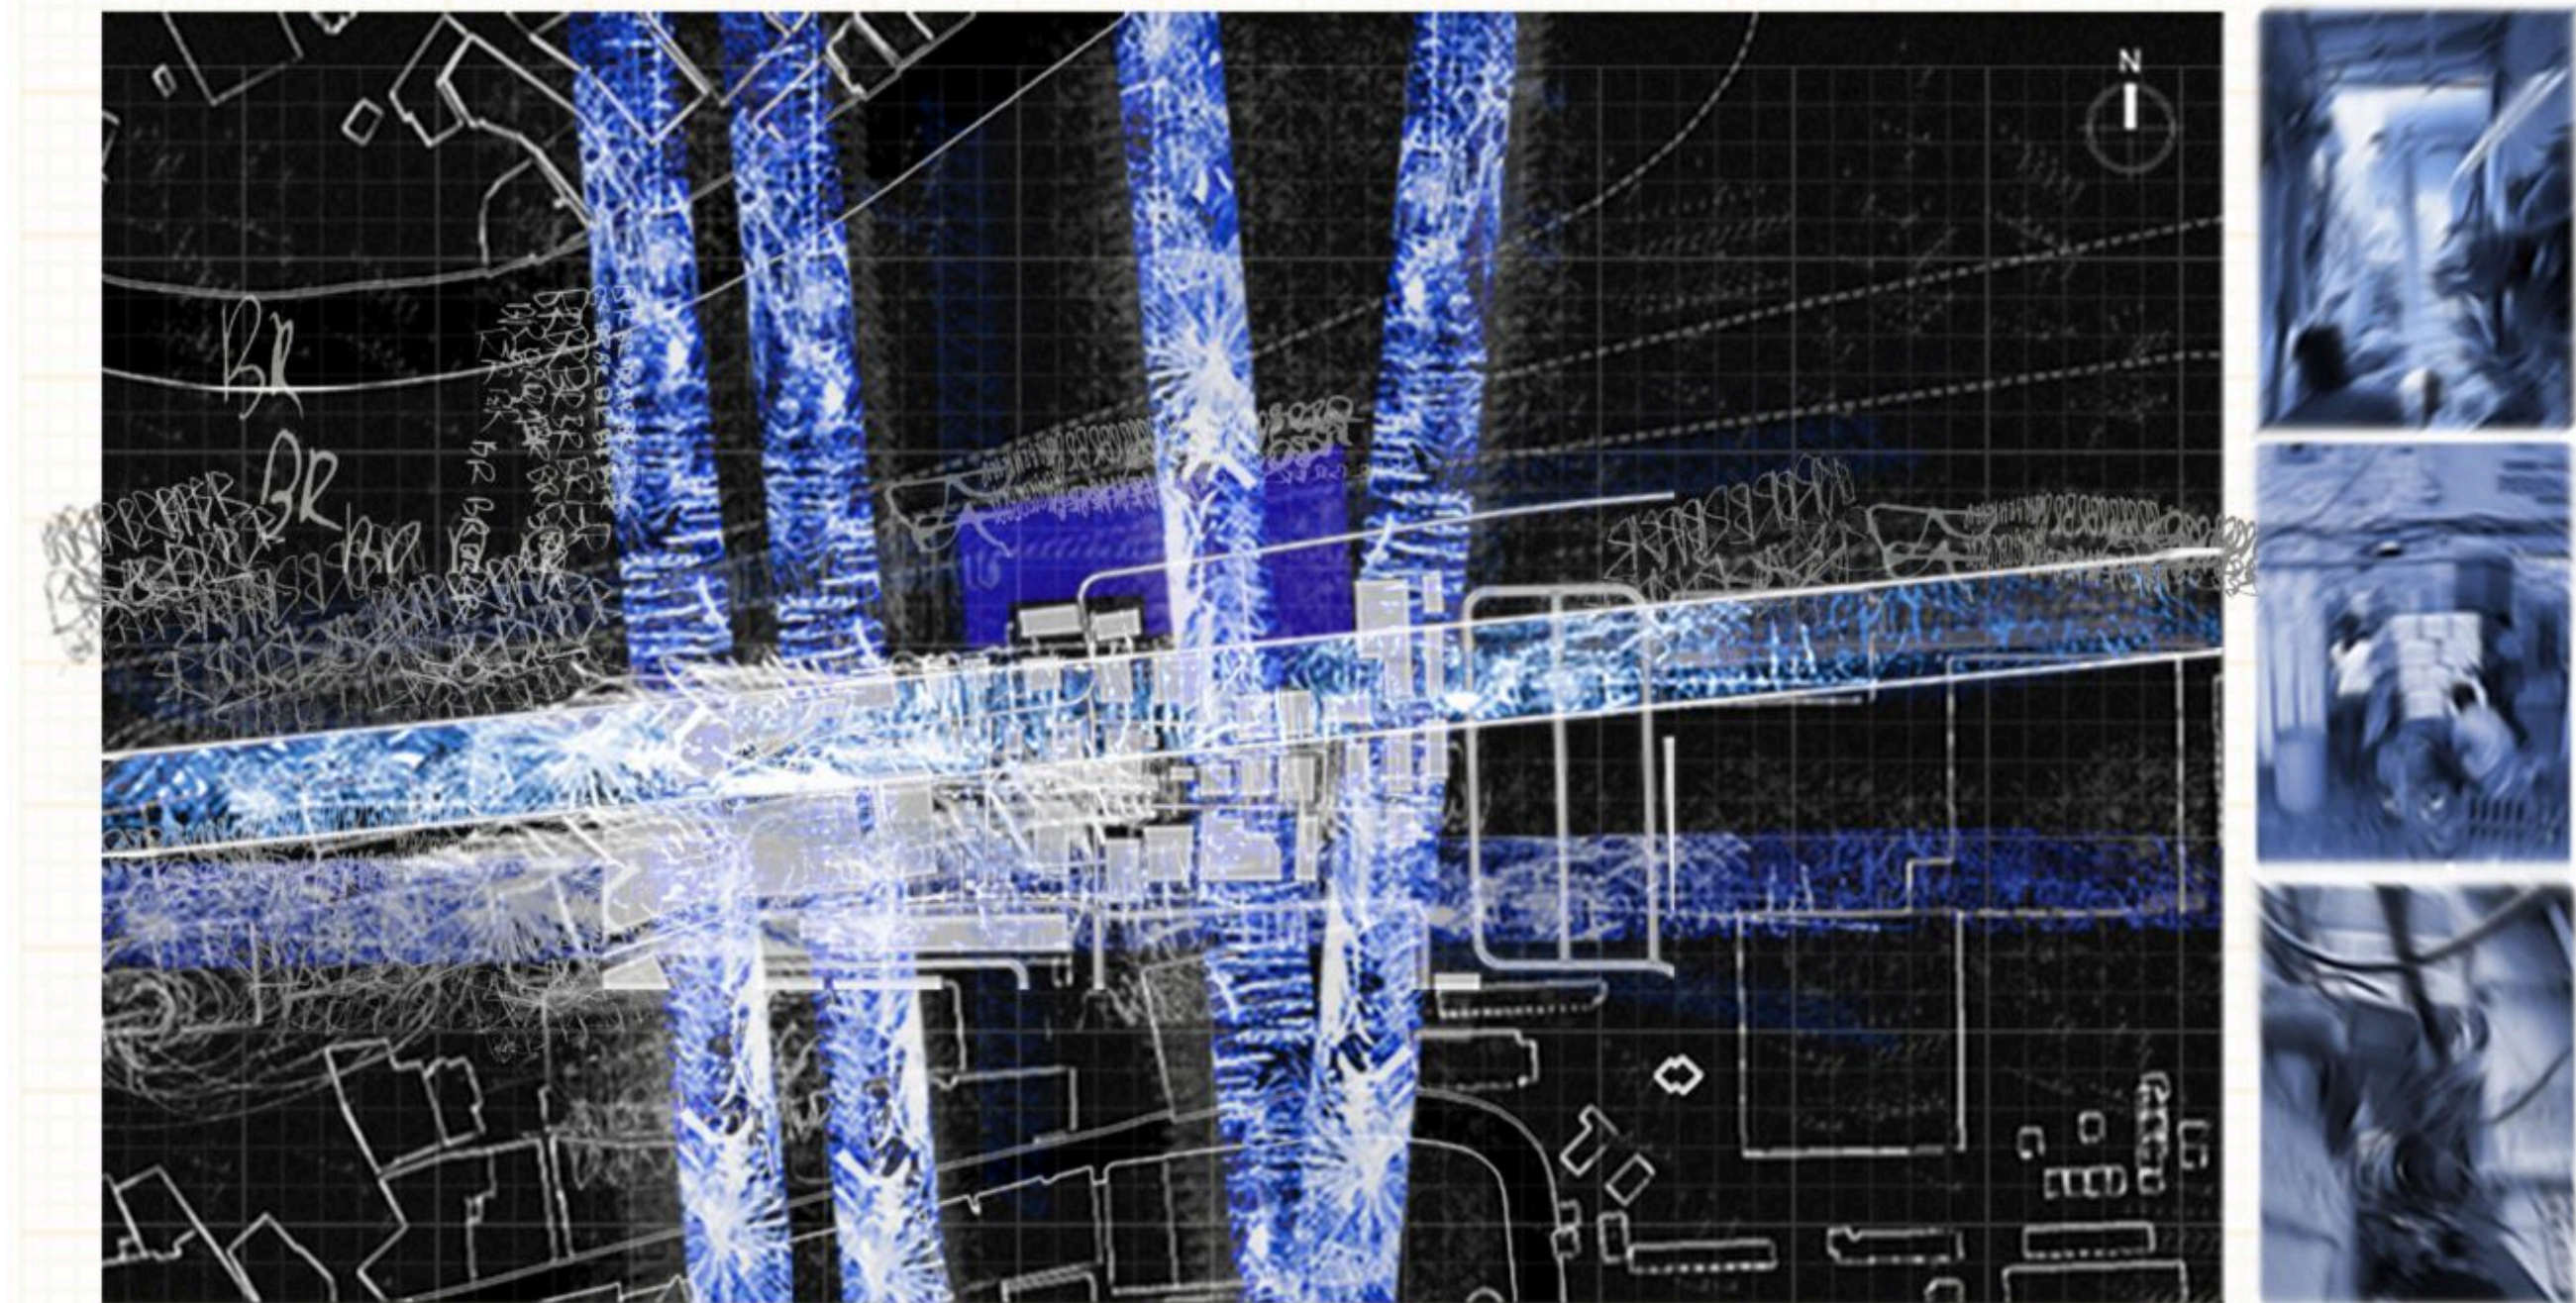



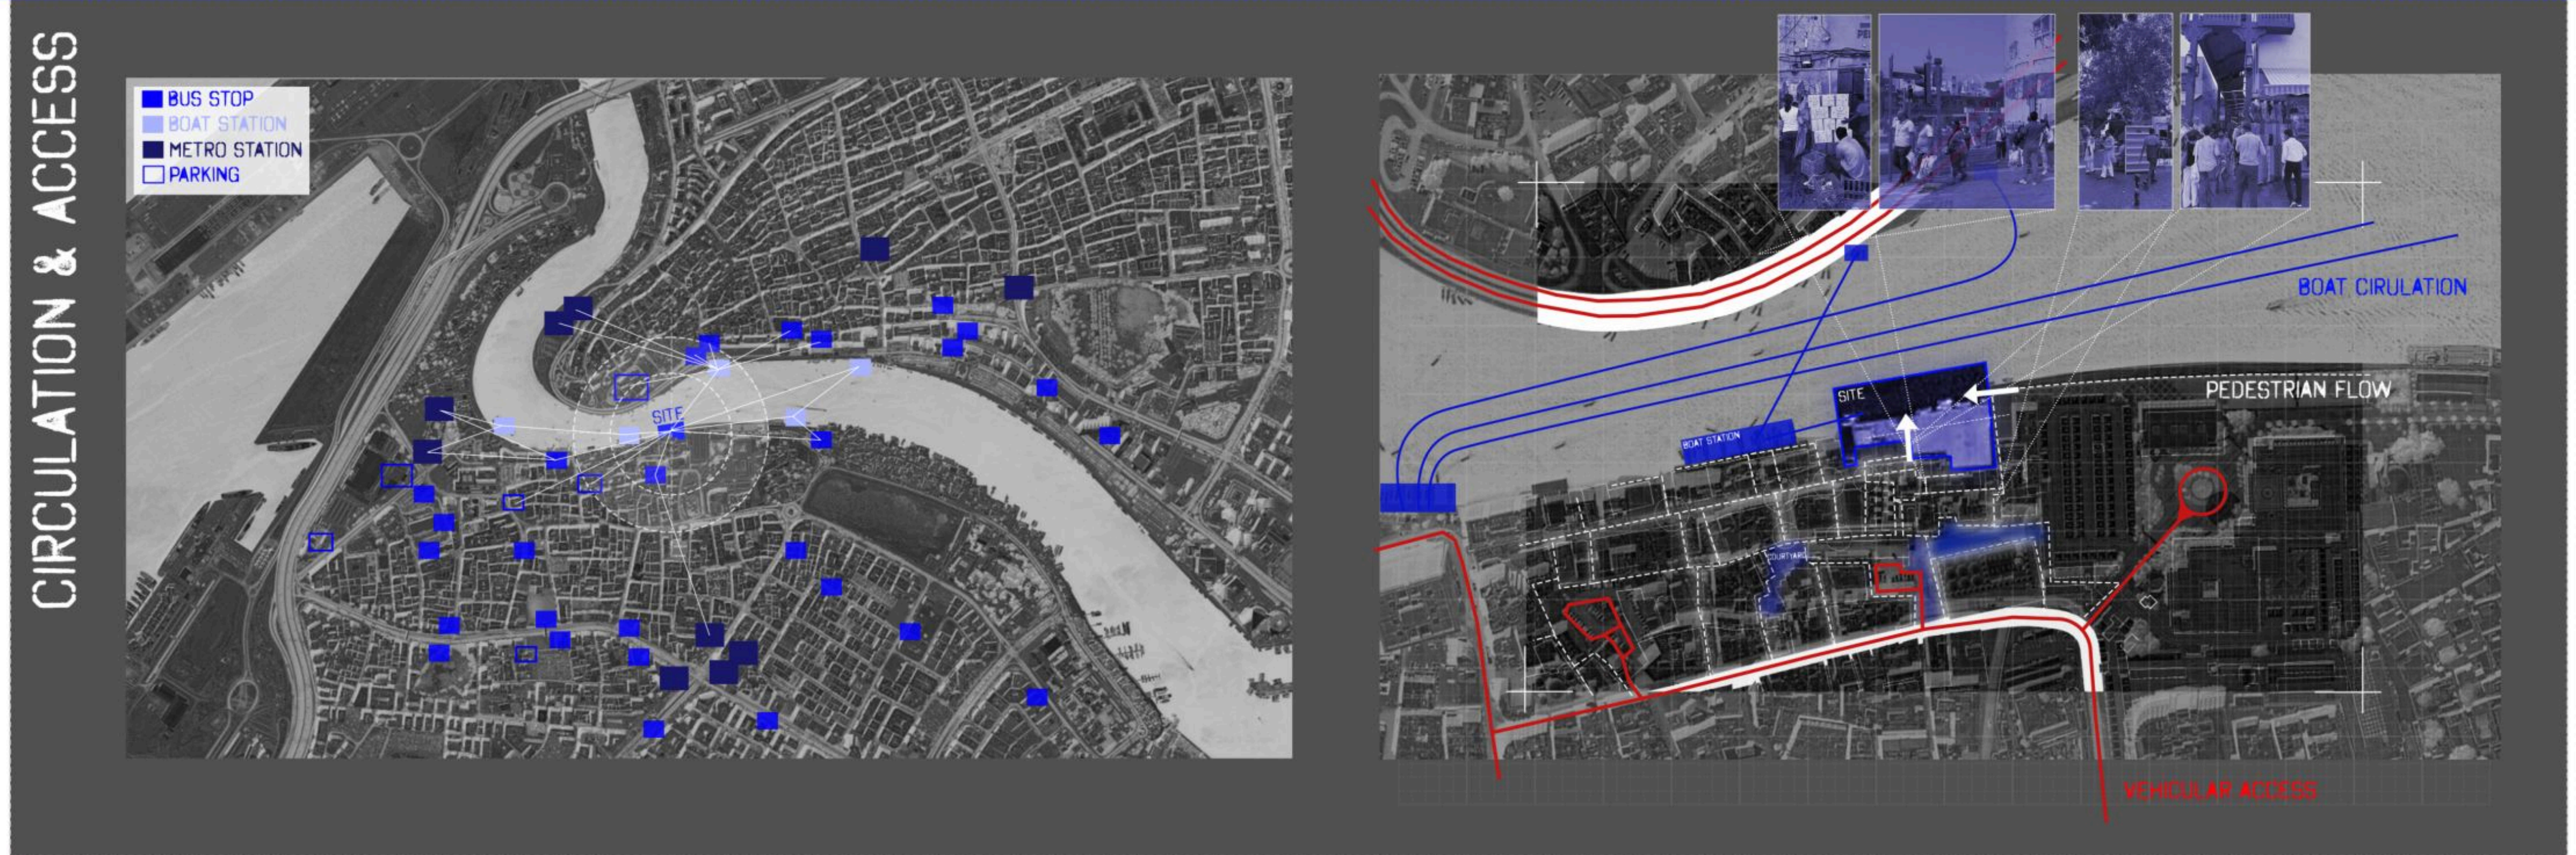


SITE SECTION

URBAN FORCES

SITE SECTION

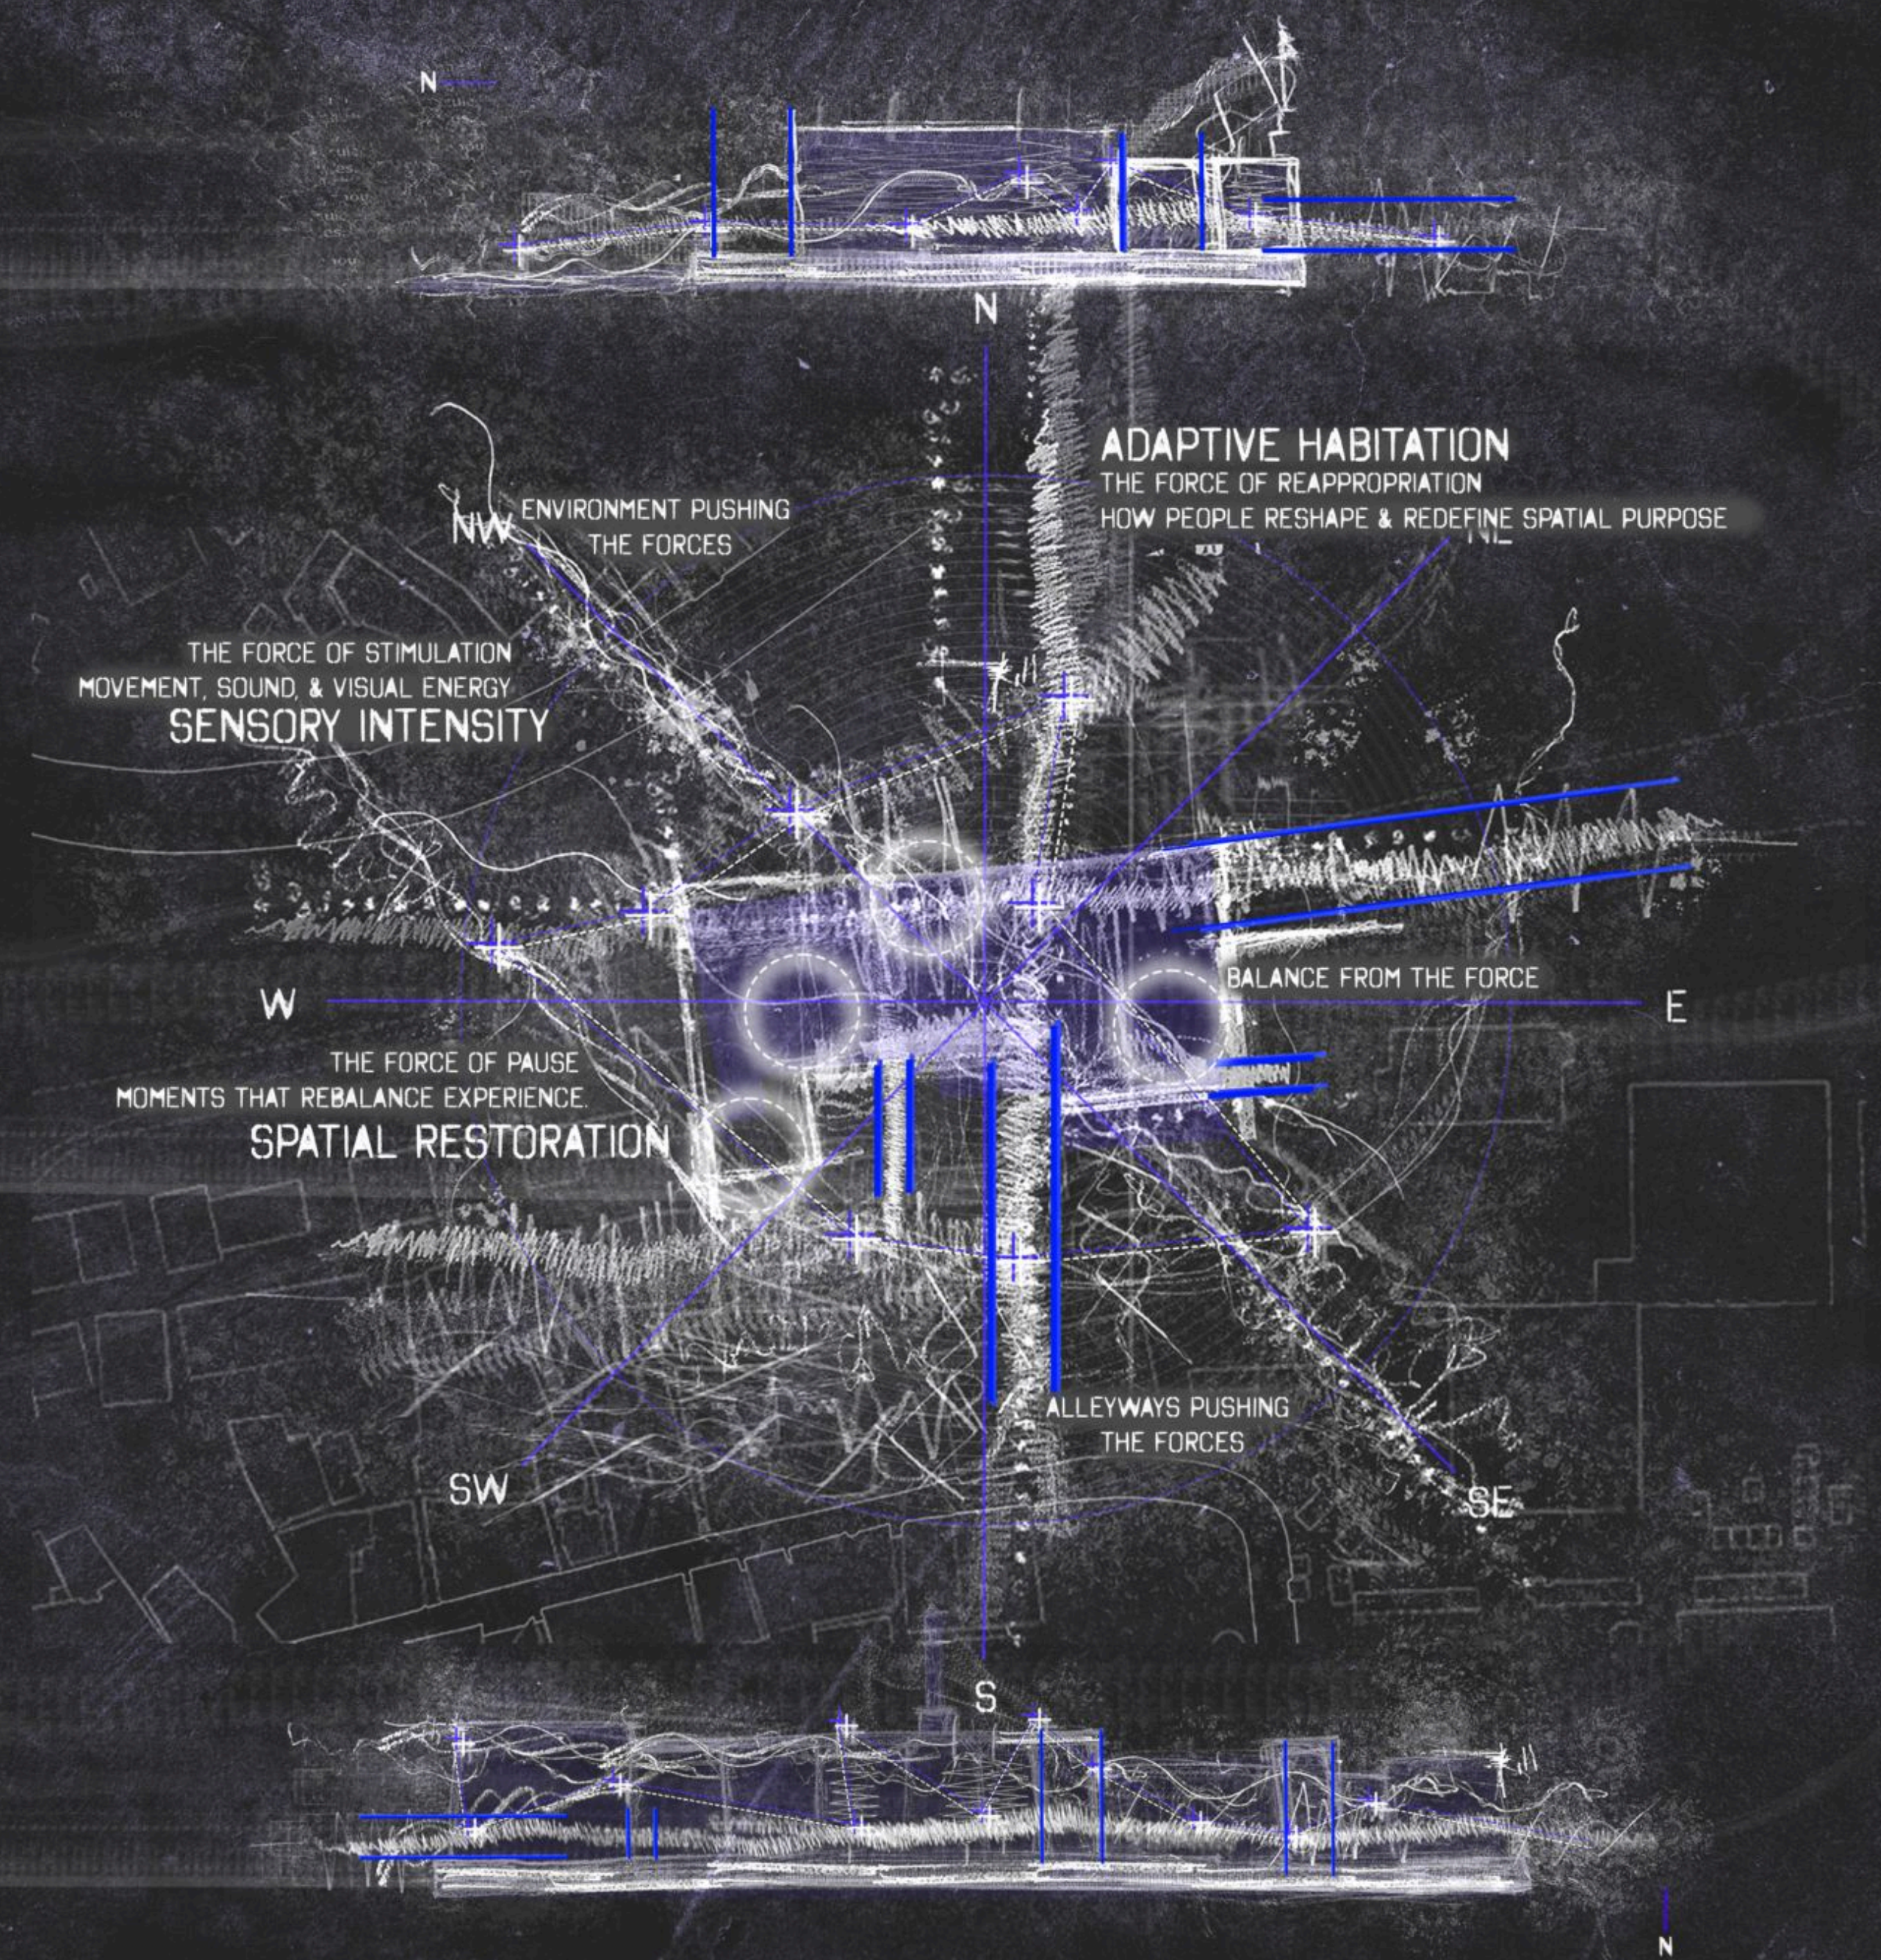

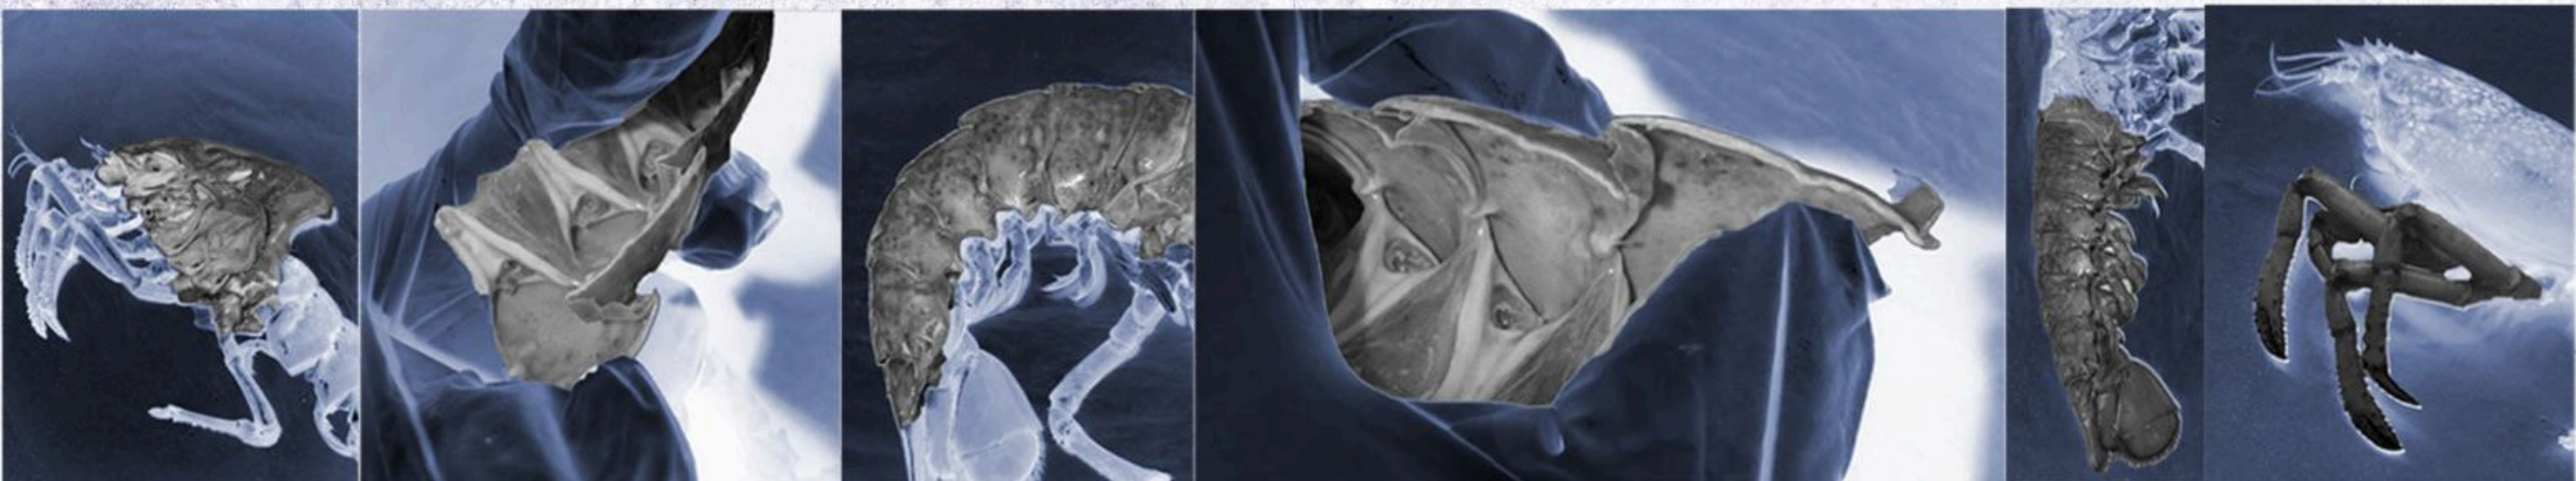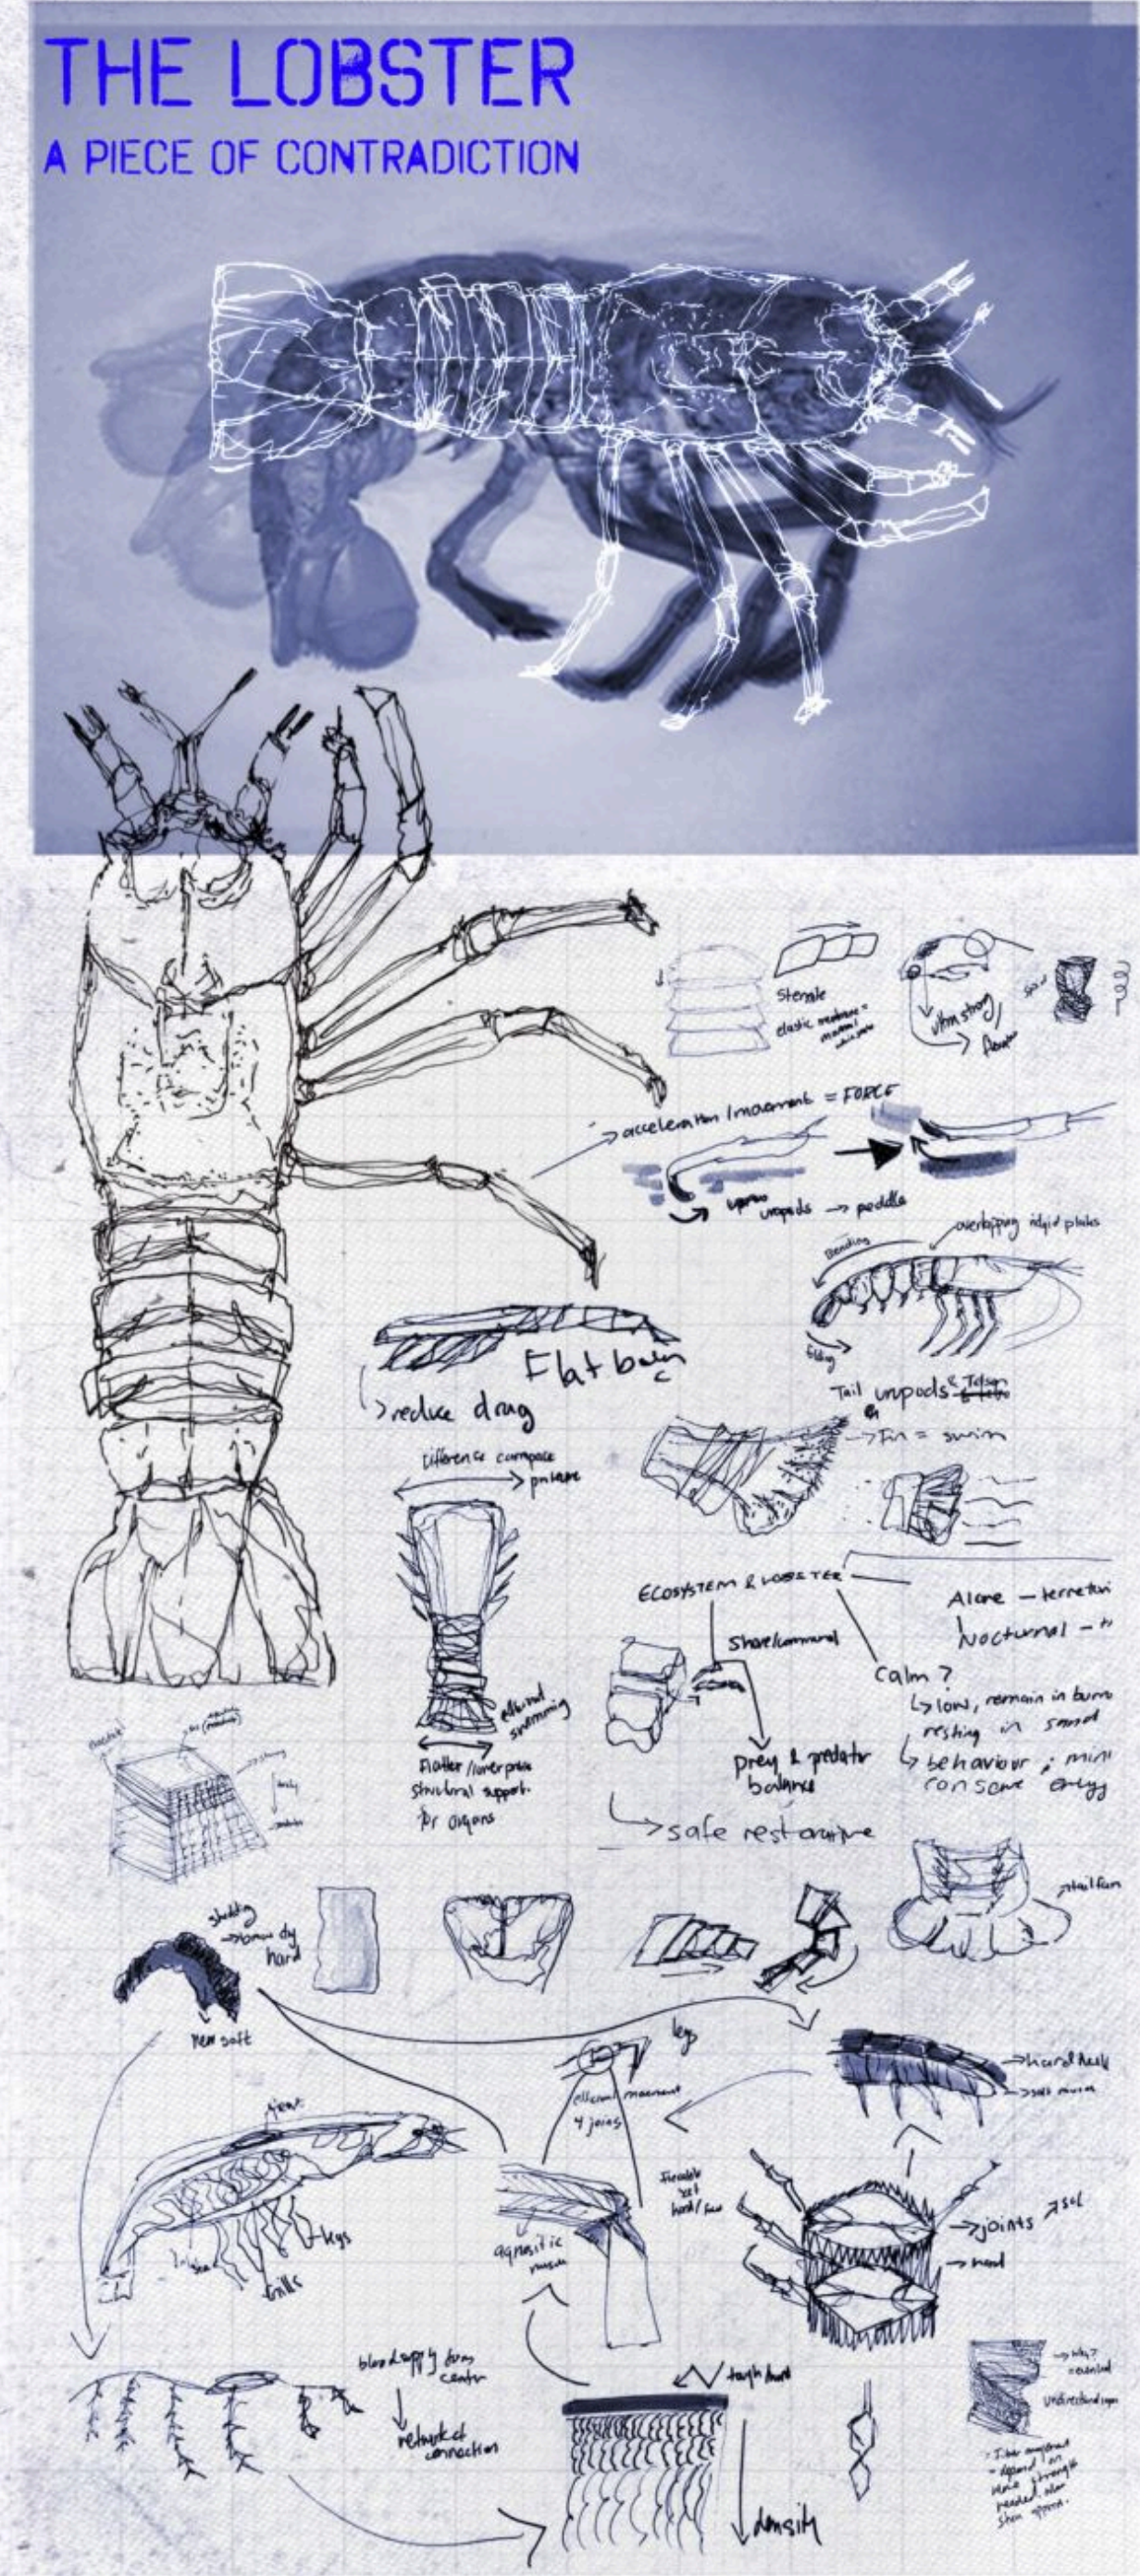

JOINTS



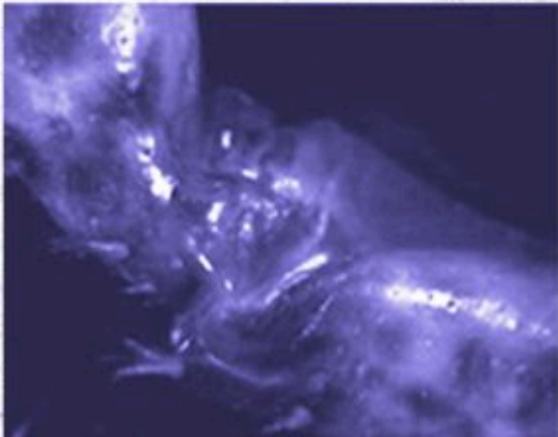


IMAGE FROM GOOGLE.
BEND

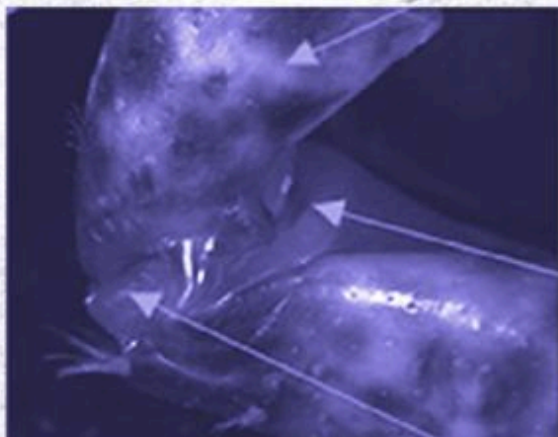

UNBEND

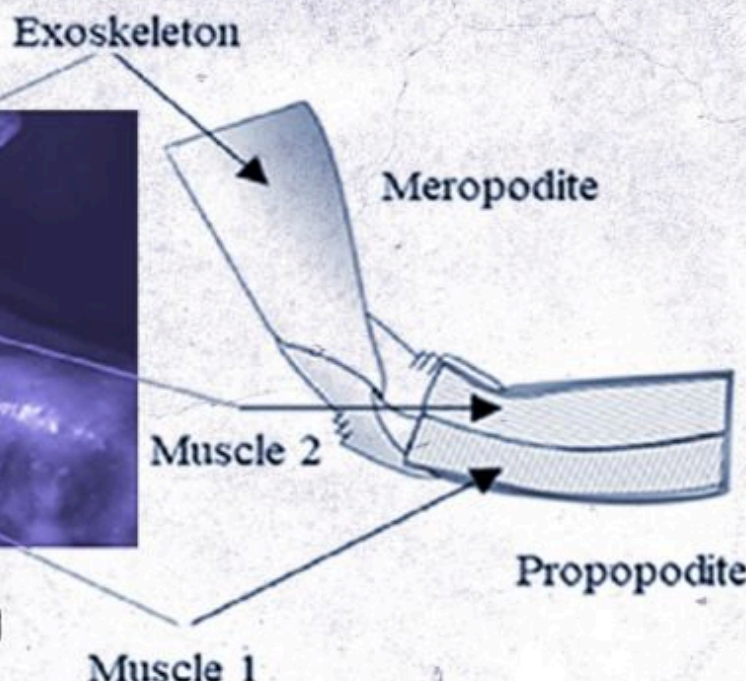

EFFICIENCY

THIN BUT STRONG SHELL
PROTECTS LARGE VOLUME

FIBER STRUCTURE


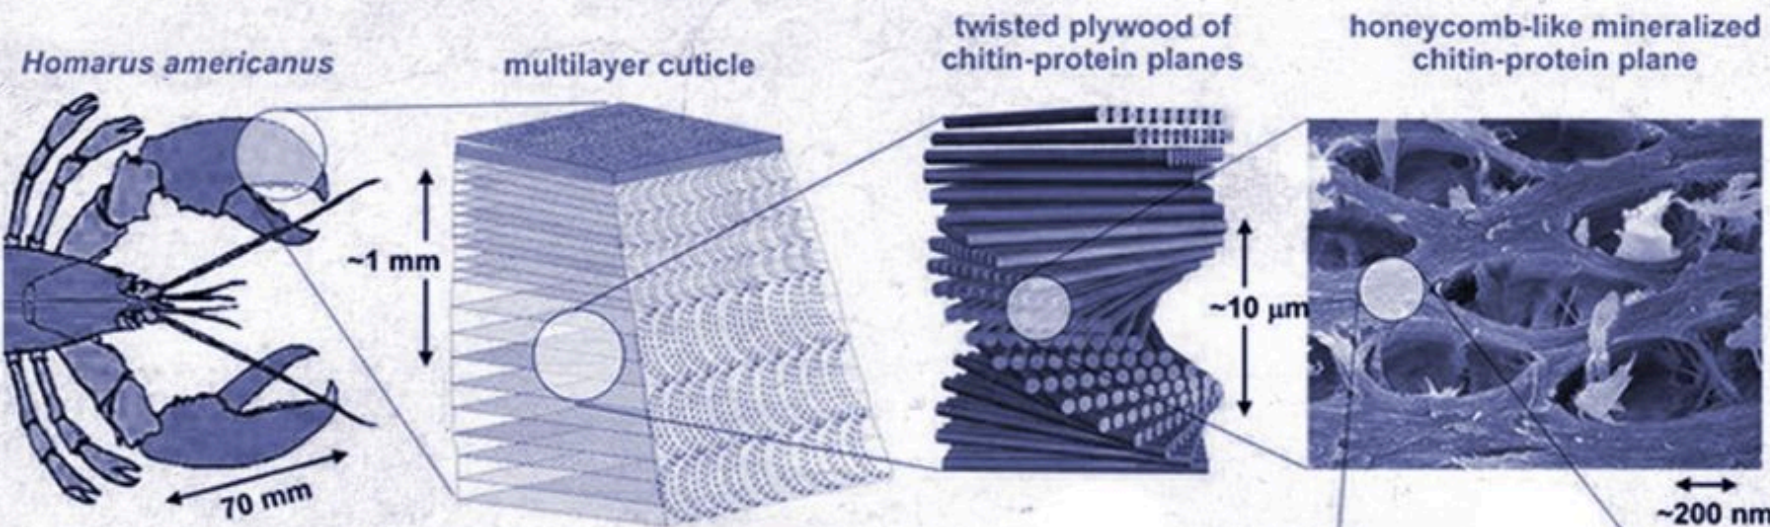


IMAGE FROM GOOGLE.


SUSTAINABILITY
& EFFICIENCY

MAXIMIZE STRENGTH
WITH MINIMAL MATERIAL

MOLTING

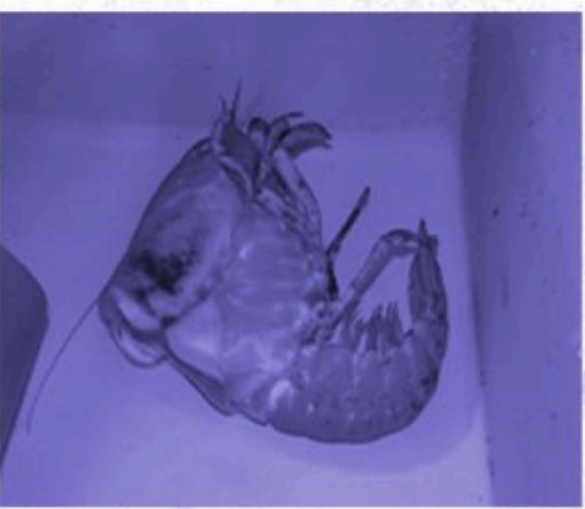

SEGMENTED BODY

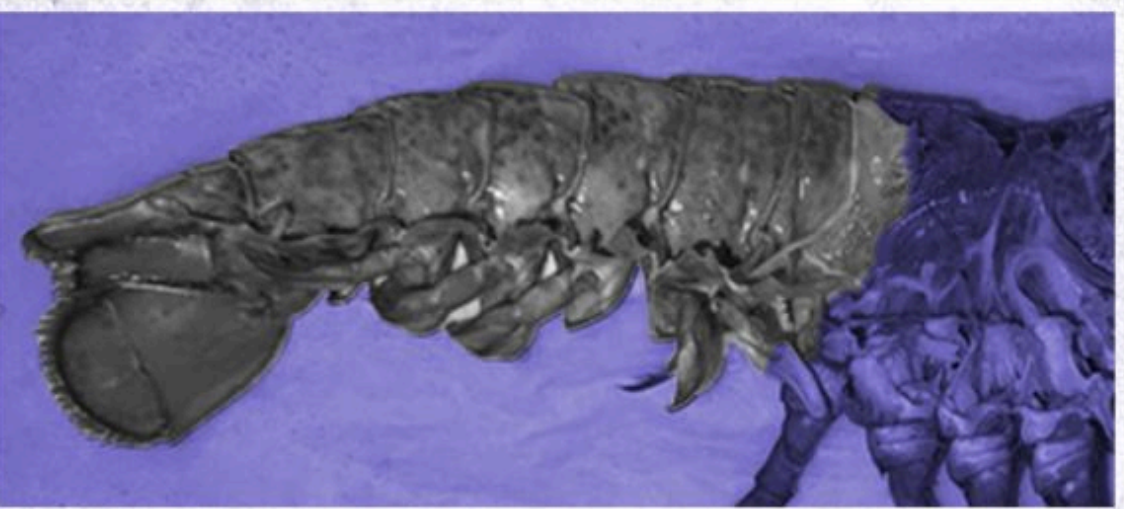

AESTHETICS
& INNOVATION


MOVABLE & ADAPTIVE
STRUCTURE. SOFT & HARD

INTERSTILITY IN THE LOBSTER

INDIVIDUAL BUT
COMMUNAL



FIXED BUT
ADAPTIVE

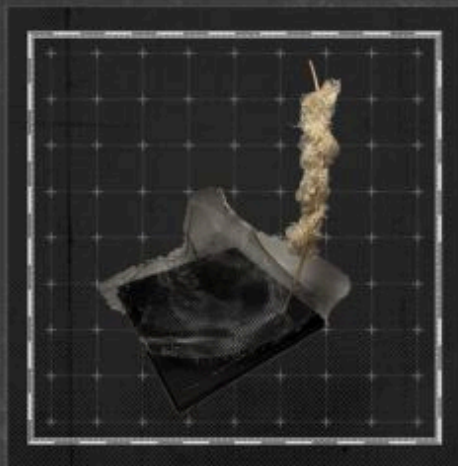

HARD BUT
SOFT




HARD BUT
FLEXABLE














HARD BUT
SOFT



HARD BUT
FLEXABLE

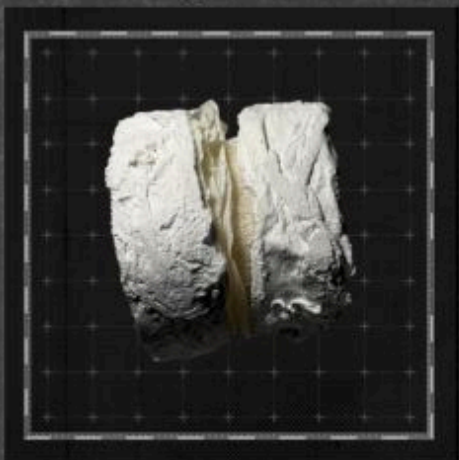

THIS DIAGRAM UNCOVERS THE CORE IDEA I CARRIED FORWARD: INDIVIDUAL COMPONENTS THAT REMAIN CONNECTED, ALWAYS NEGOTIATING BETWEEN SEPARATION AND UNITY. EACH QUALITY, FIXED BUT ADAPTIVE, HARD BUT SOFT BECAME AN ARCHITECTURAL FORCE.

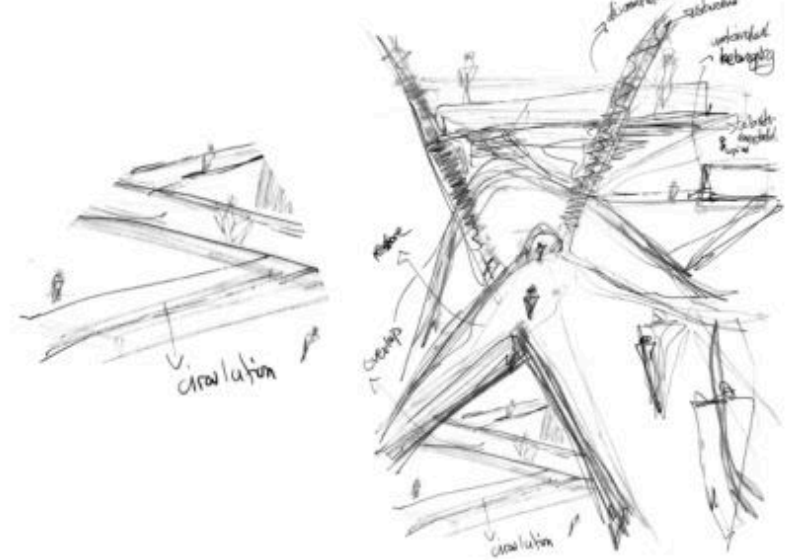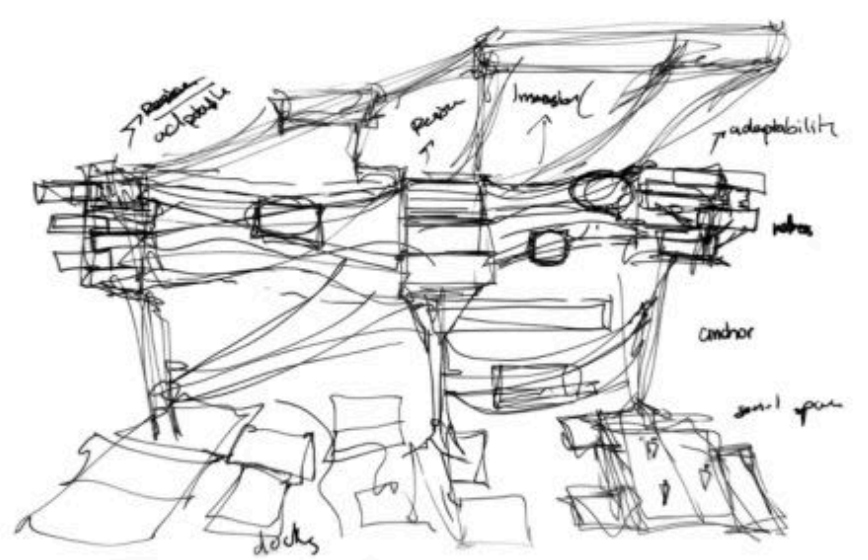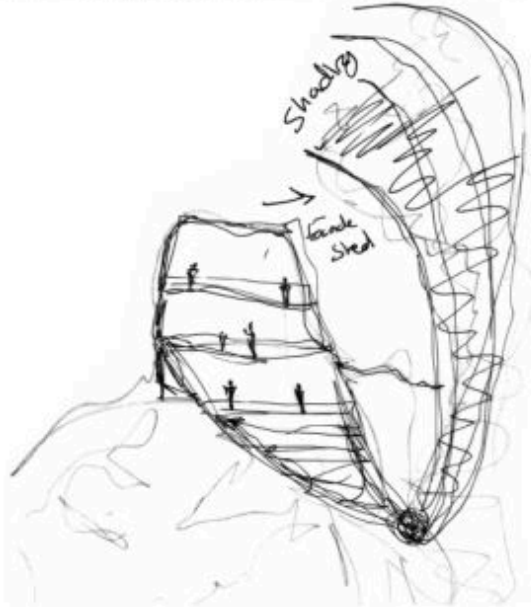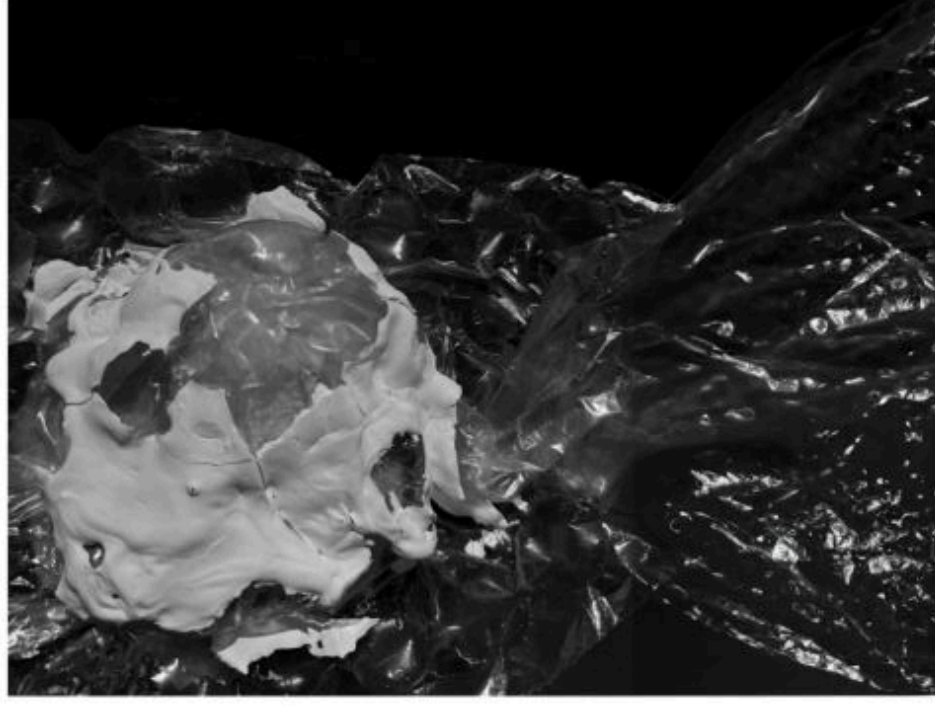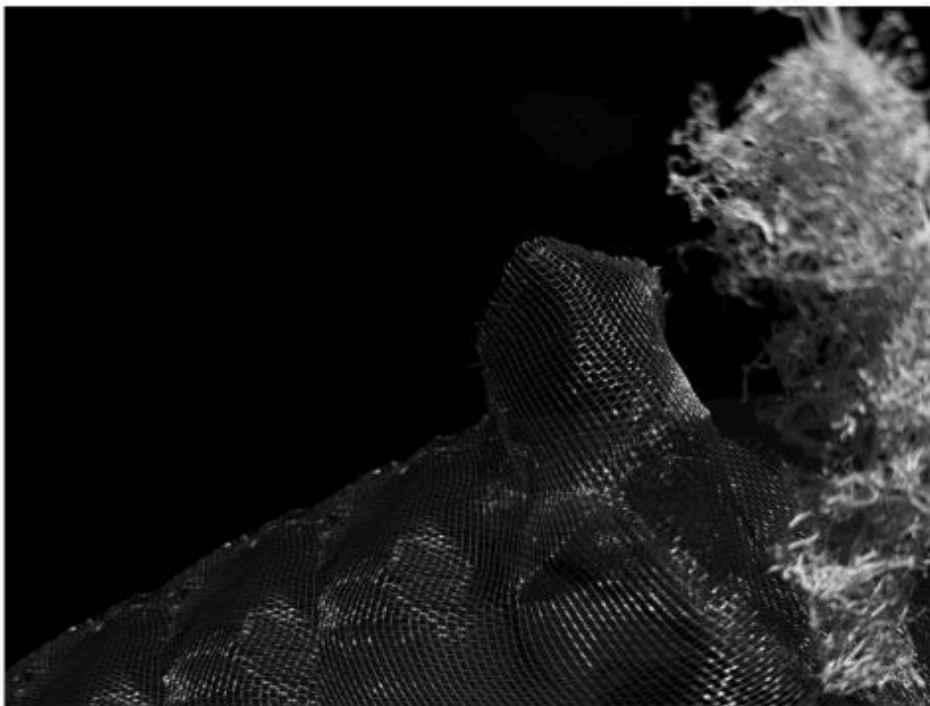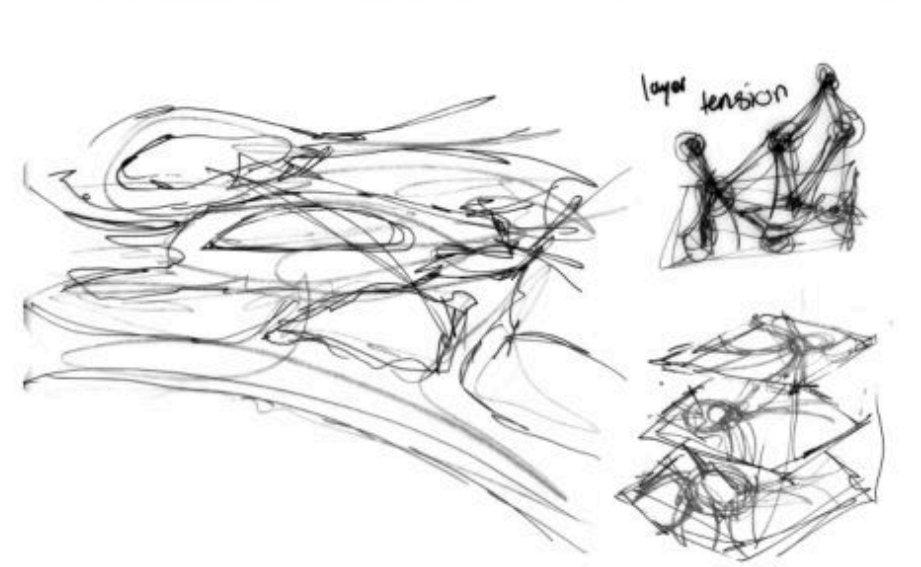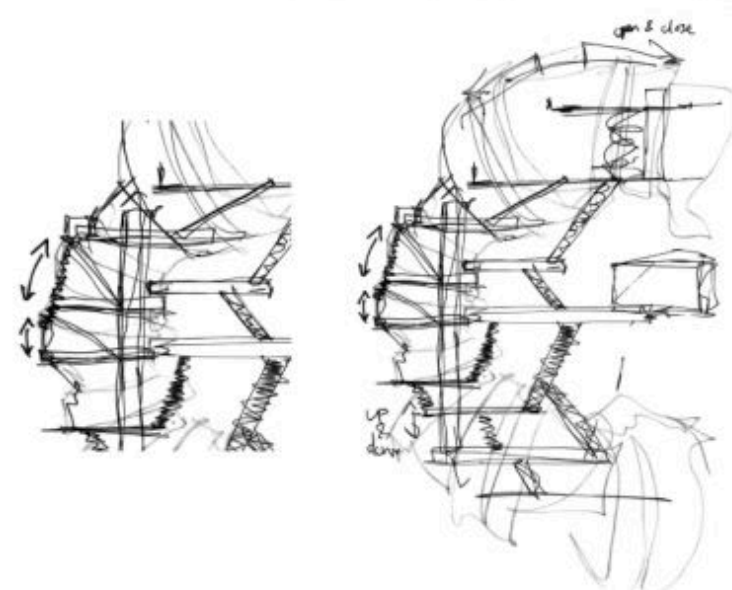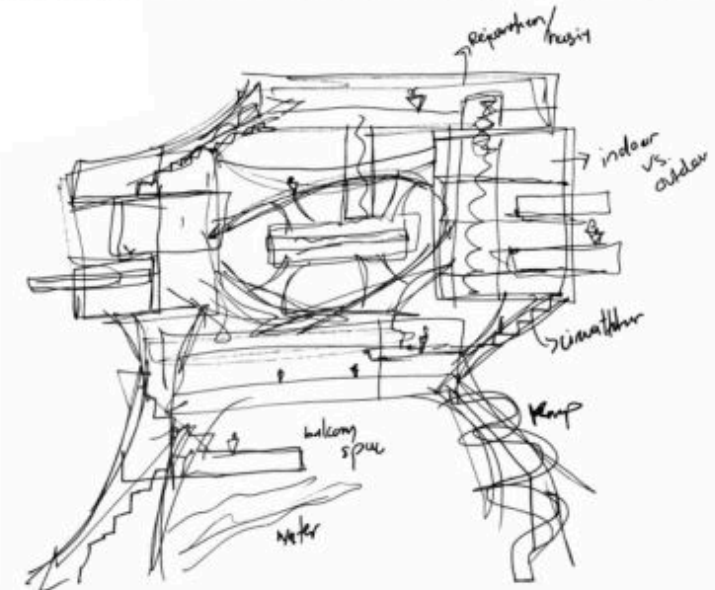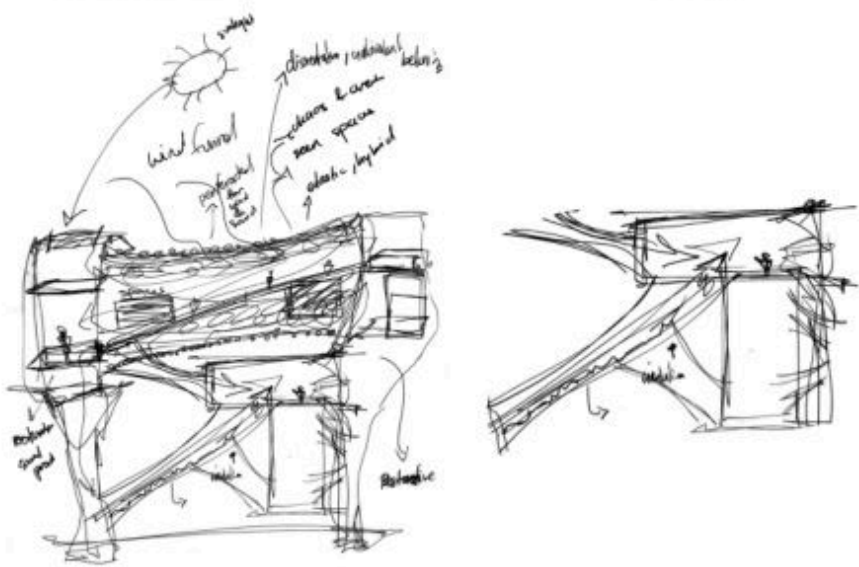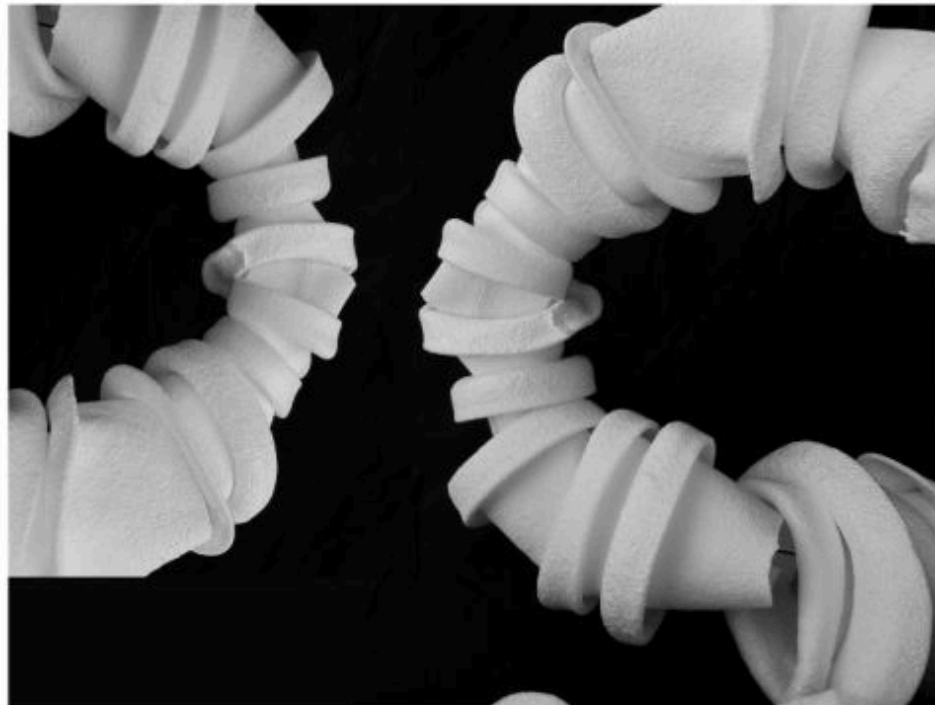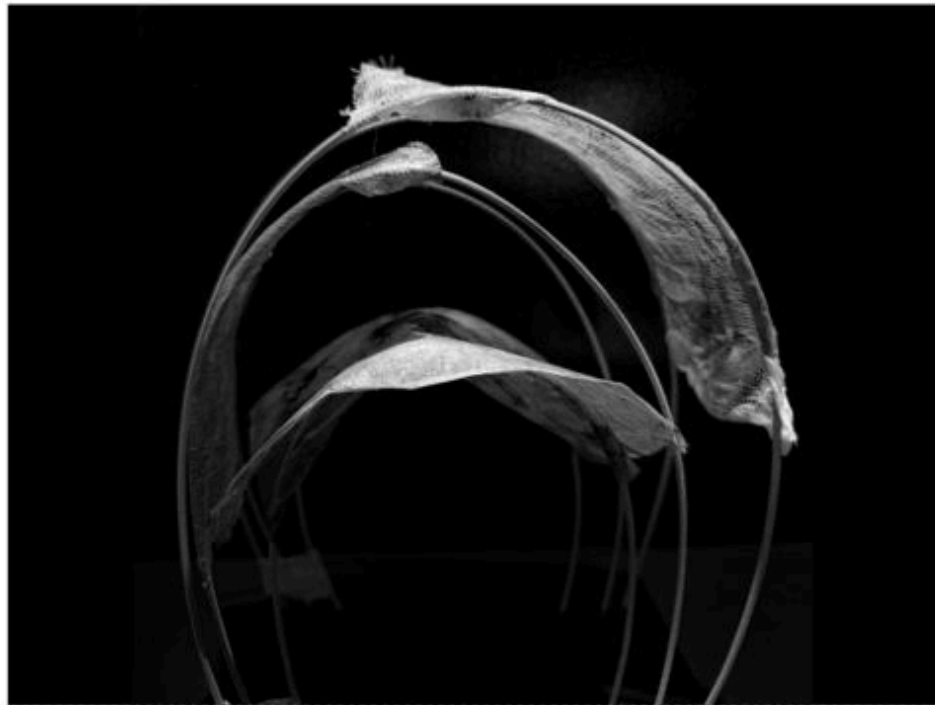

BIOARTIFACT AND URBAN FORCE SHAPED INTO MODELS

THE BIO MODEL BECAME A WAY TO TEST HOW MOVEMENT COULD BE TRANSLATED INTO FORM. BY PINCHING, STRETCHING, AND PULLING THE MATERIAL, I COULD MIMIC THE WAY A LOBSTER'S BODY SHIFTS AS IT MOVES , SEGMENTS TIGHTENING, EXPANDING, AND ADJUSTING TO PRESSURE. WHEN I HANDLED THE MODEL, IT RESPONDED IN THE SAME WAY THE SITE DOES: CERTAIN DIRECTIONS RESISTED, OTHERS OPENED EASILY. THIS HELPED ME IMAGINE THE BUILDING NOT AS A FIXED OBJECT BUT AS SOMETHING SHAPED BY THE FORCES ACTING ON IT. THE GESTURES IN THE MODEL REFLECT BOTH BIOLOGICAL MOTION AND THE PUSH AND PULL OF AL FAHIDI'S URBAN CONDITIONS. THESE MOVEMENTS LATER INFORMED HOW VOLUMES COLLIDE, LIFT, AND FOLD IN THE FINAL ARCHITECTURE.






LOBSTER INSPIRED MODEL.

URBAN FORCES MODEL










FABRIC PIECE USED TO CREATE MODEL. FABRIC PATTERN ILLUSTRATED SITE RHYTHMS AND TENSION.

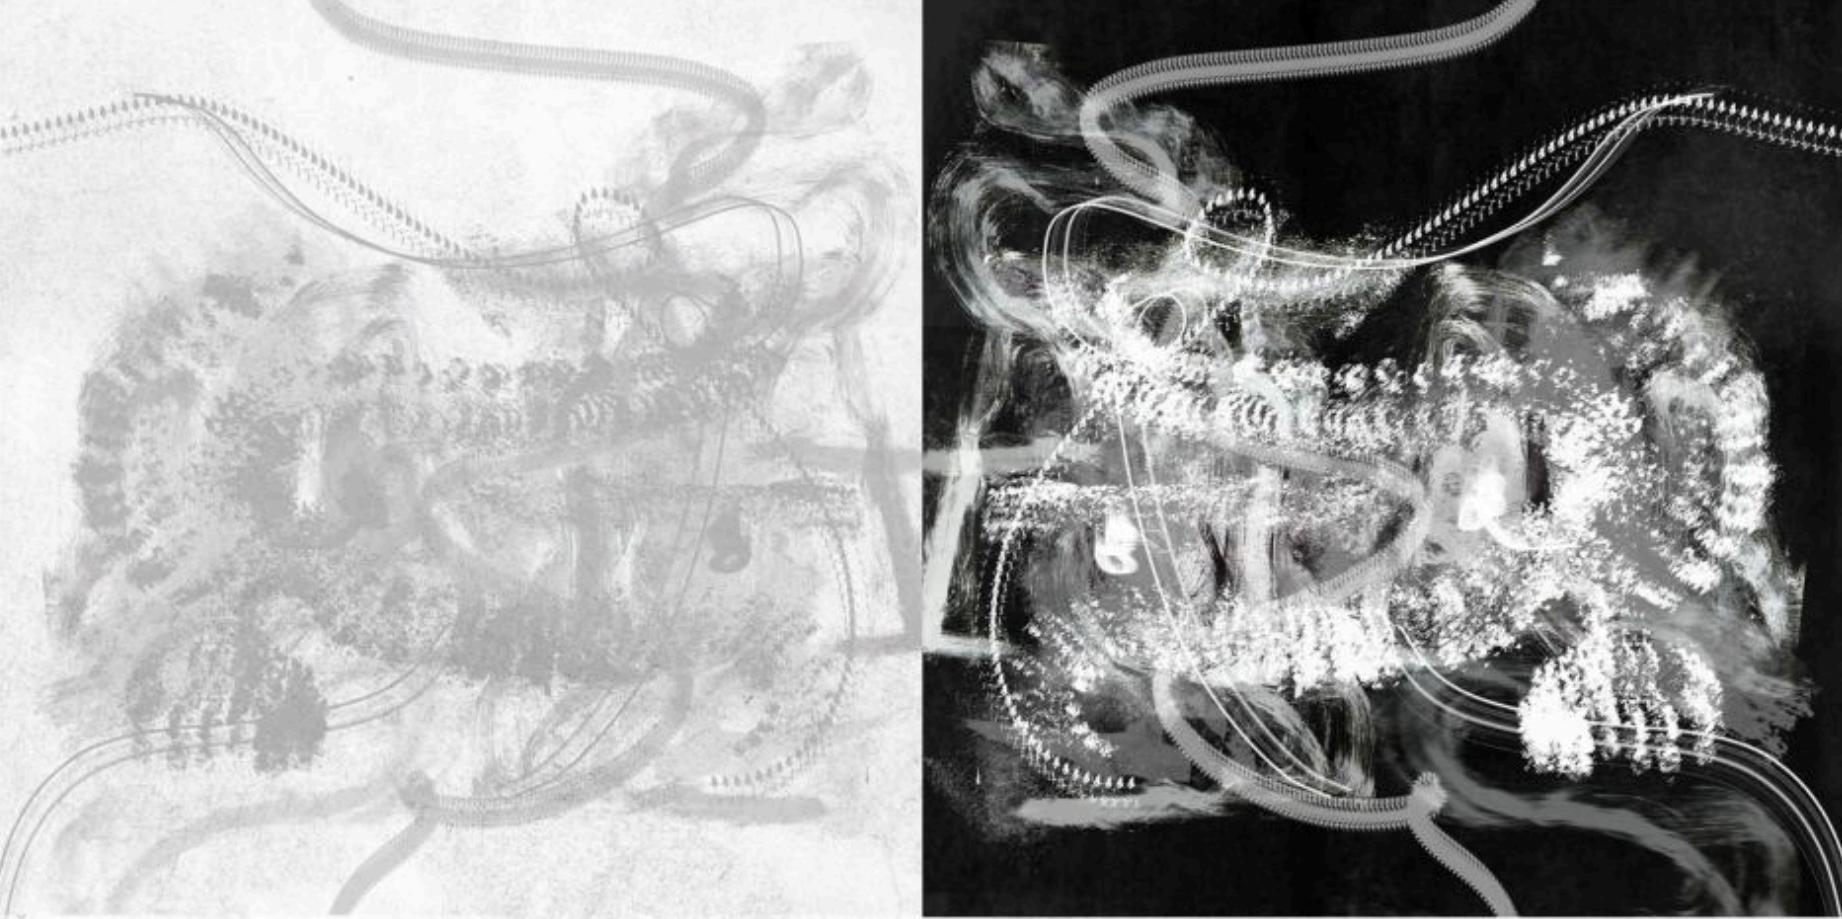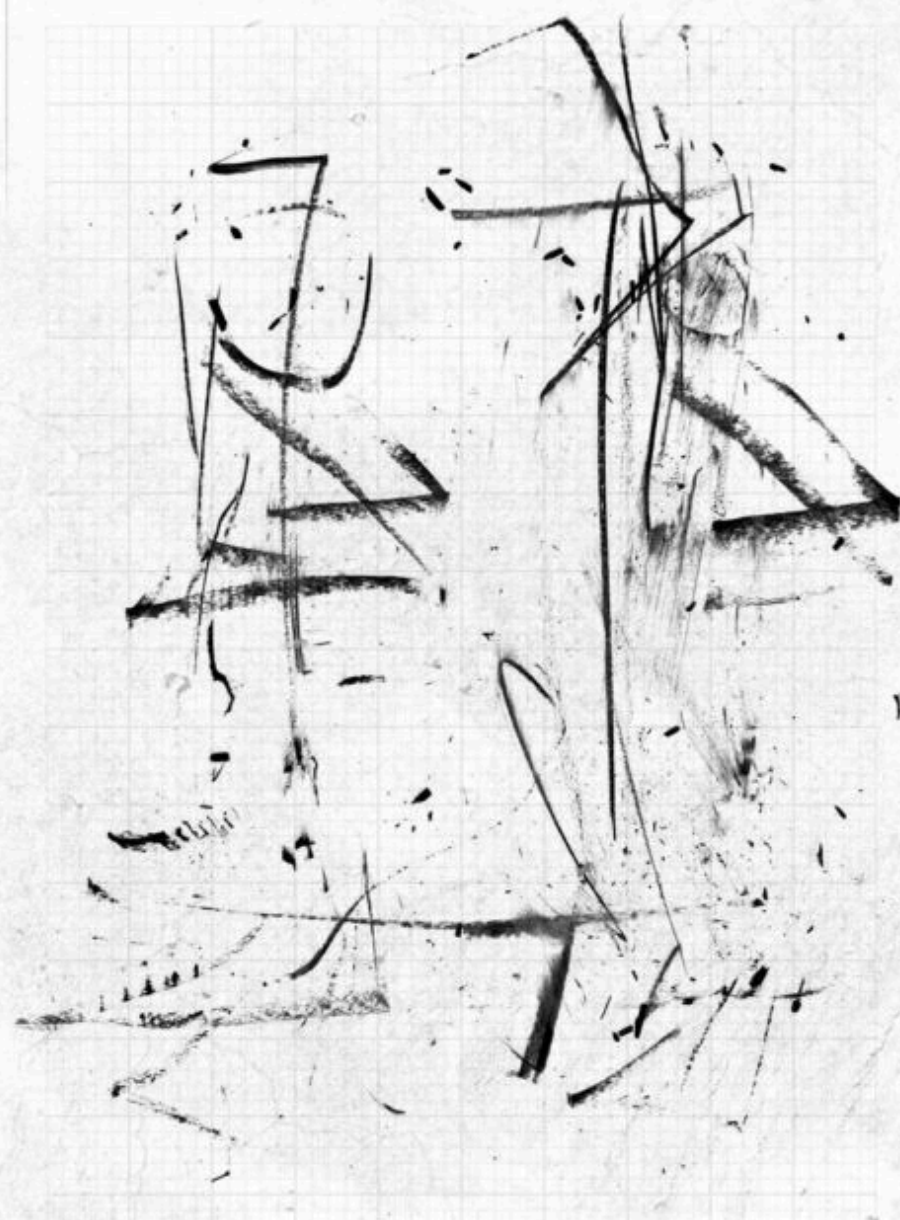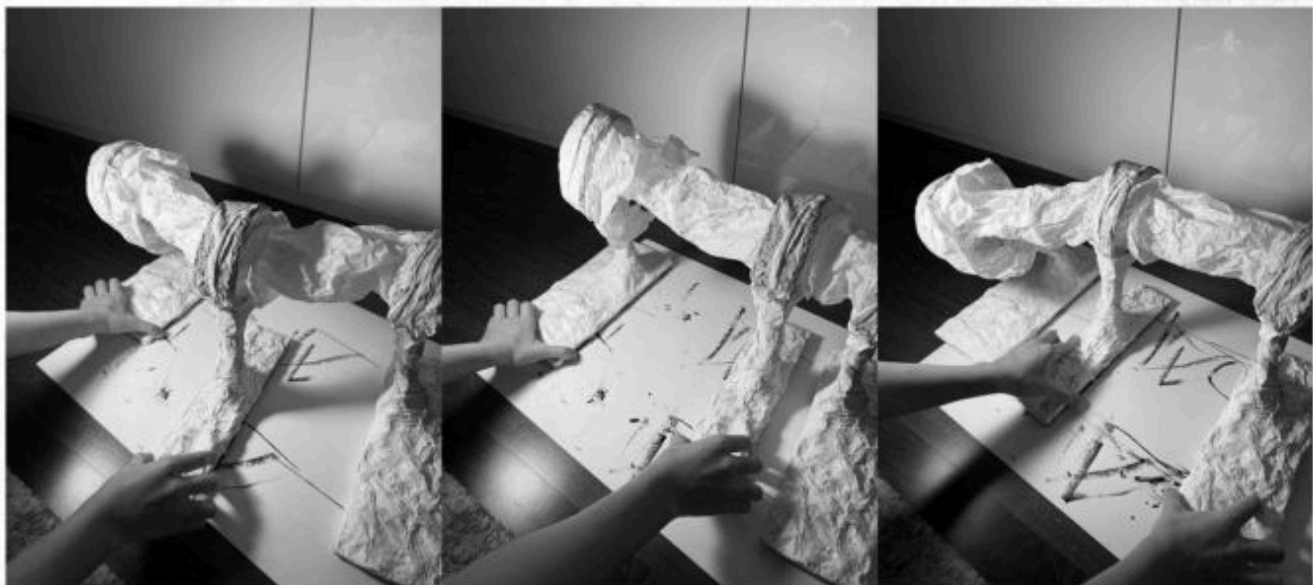


THIS PROJECT EXPLORES HOW ARCHITECTURE CAN MEDIATE BETWEEN IMMERSION AND RETREAT WITHIN THE LAYERED INTENSITY OF AL FAHIDI. I CHOSE TO DESIGN AN AMPHIBIOUS HOUSING PROPOSAL THAT GIVES RESIDENTS THE AGENCY TO DECIDE HOW DEEPLY THEY WANT TO ENGAGE WITH THE NEIGHBOURHOOD'S CULTURAL AND SOCIAL RHYTHMS. RATHER THAN CREATING A SEALED SANCTUARY OR A FULLY EXPOSED COMMUNAL SPACE, THE PROJECT SITS IN THE IN-BETWEEN, SHAPED BY PULLING, PINCHING, AND SEGMENTING FORCES INSPIRED BY BOTH THE SITE AND THE LOBSTER STUDIES. THE BRIEF CENTRES ON ACCESSIBILITY, ADAPTABILITY, AND EMOTIONAL COMFORT, OFFERING HOUSING THAT RESPONDS TO SHIFTING NEEDS AND CHANGING LEVELS OF PUBLIC INTERACTION. THE AIM WAS TO CREATE A PLACE WHERE YOU CAN STEP INTO THE ENERGY OF AL FAHIDI WHEN YOU WANT TO, AND STEP BACK WHEN YOU NEED TO, WITHOUT EVER FEELING DISCONNECTED FROM THE LIFE AROUND YOU.





FORM DEVELOPMENT

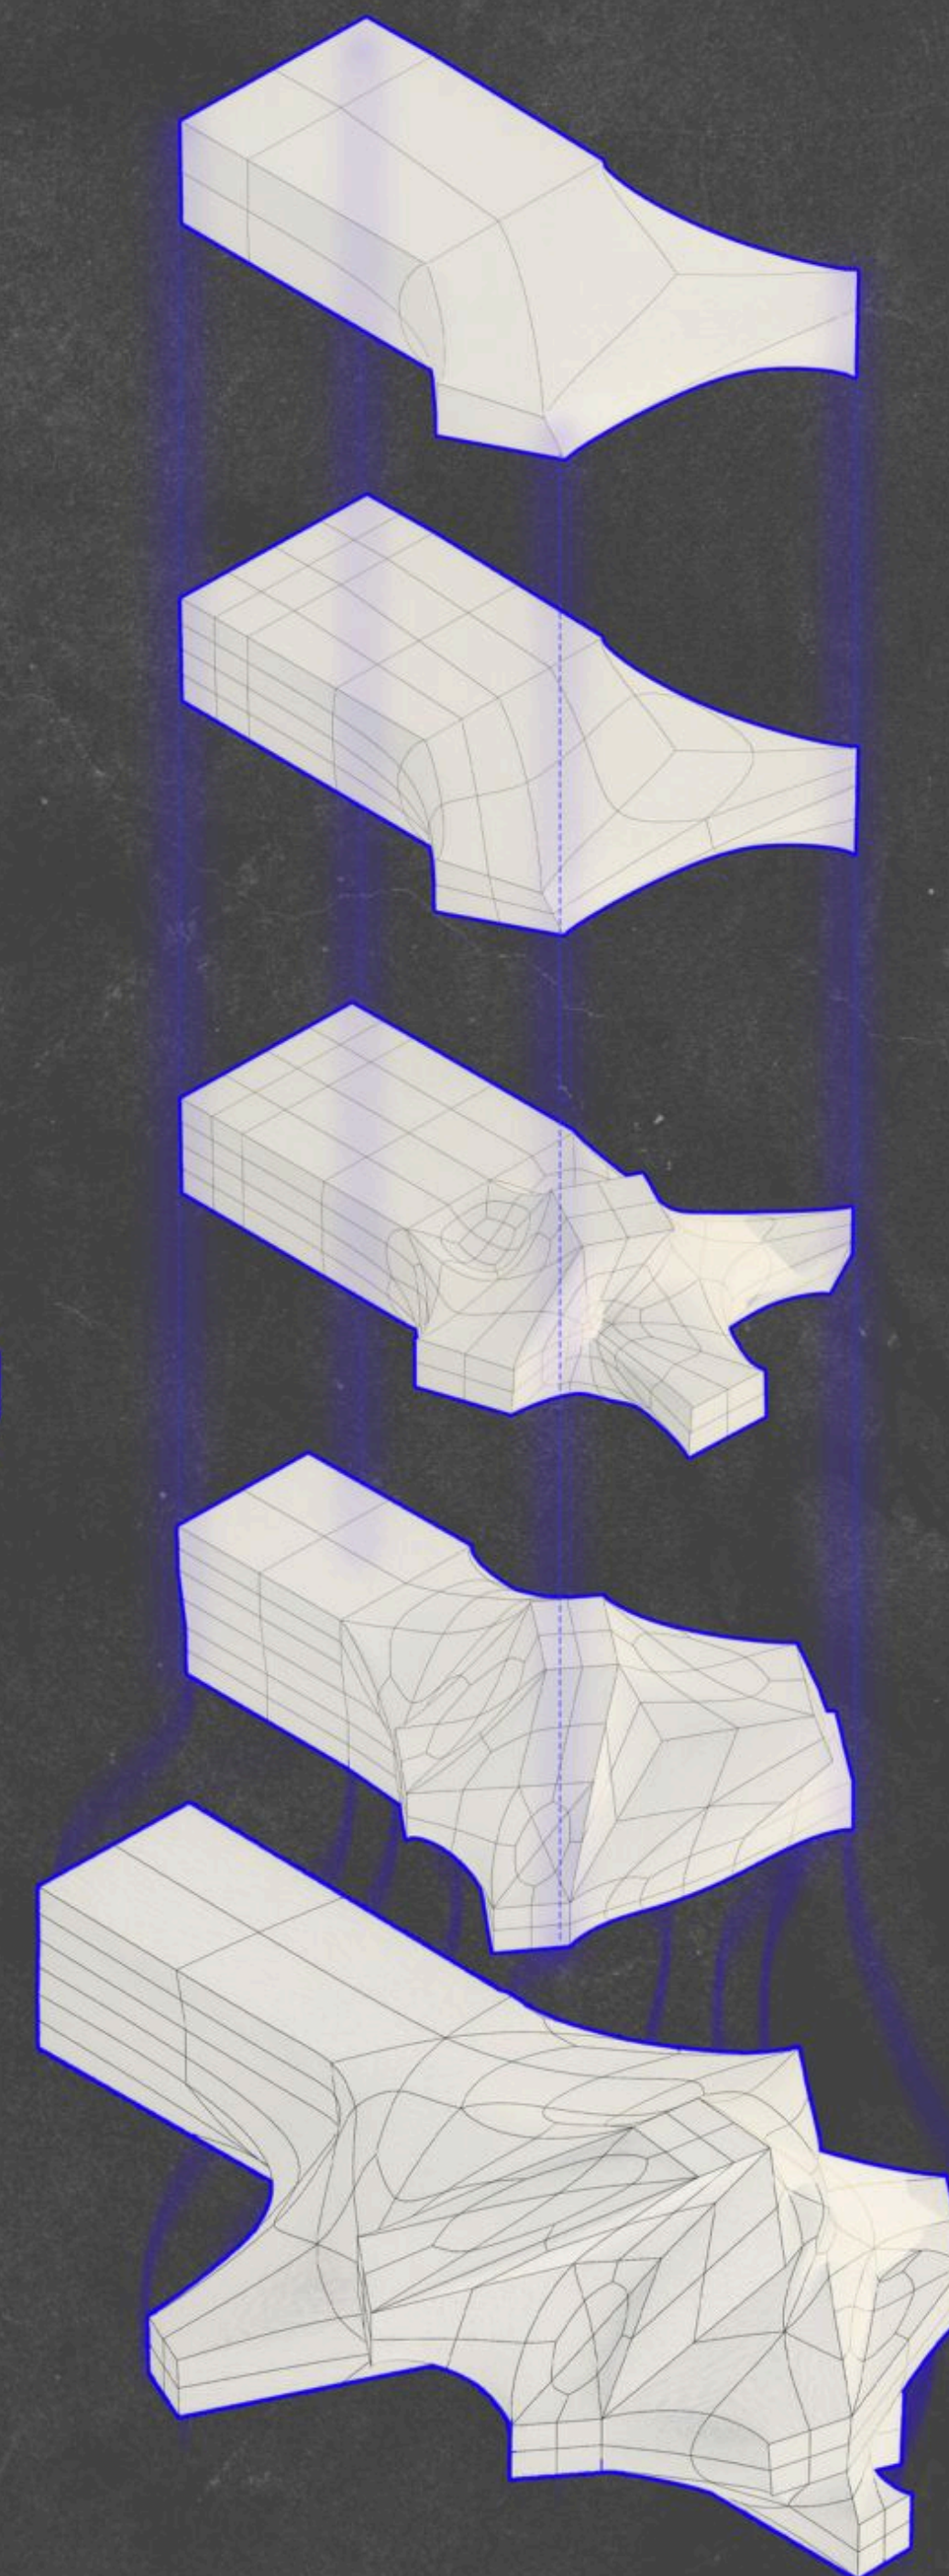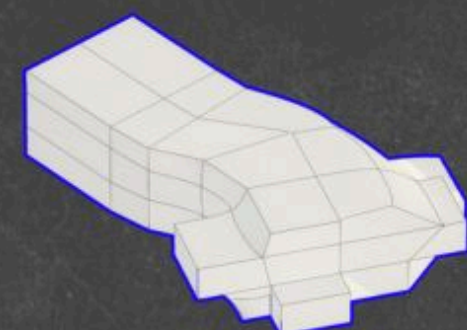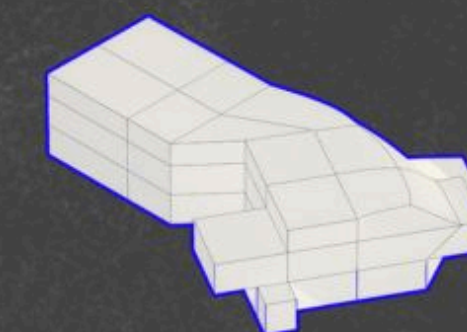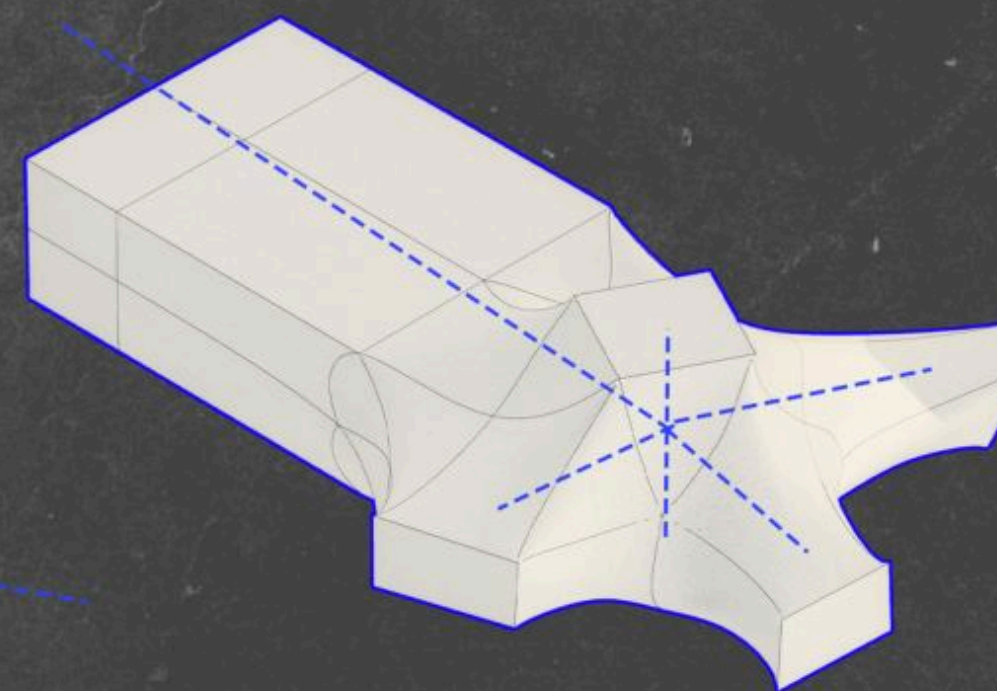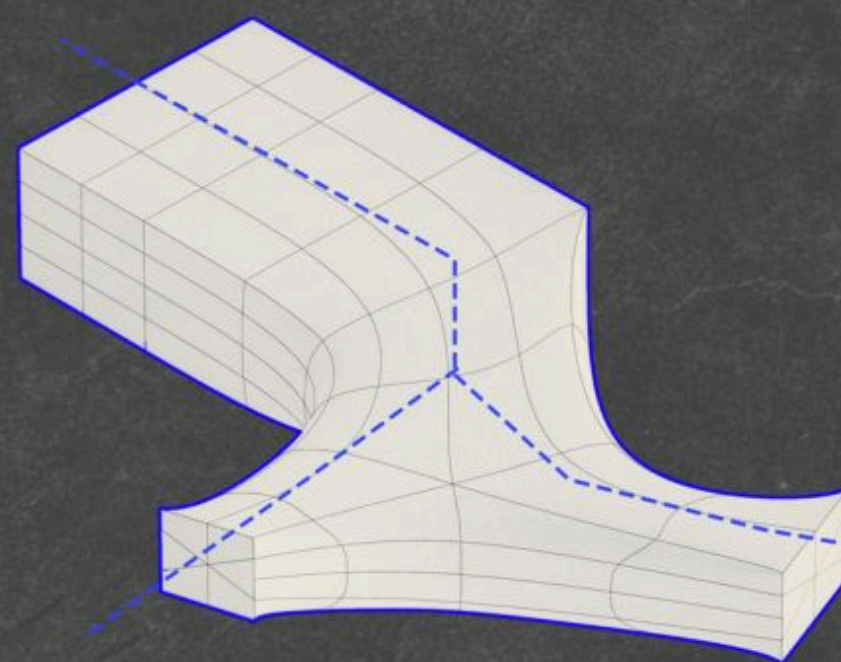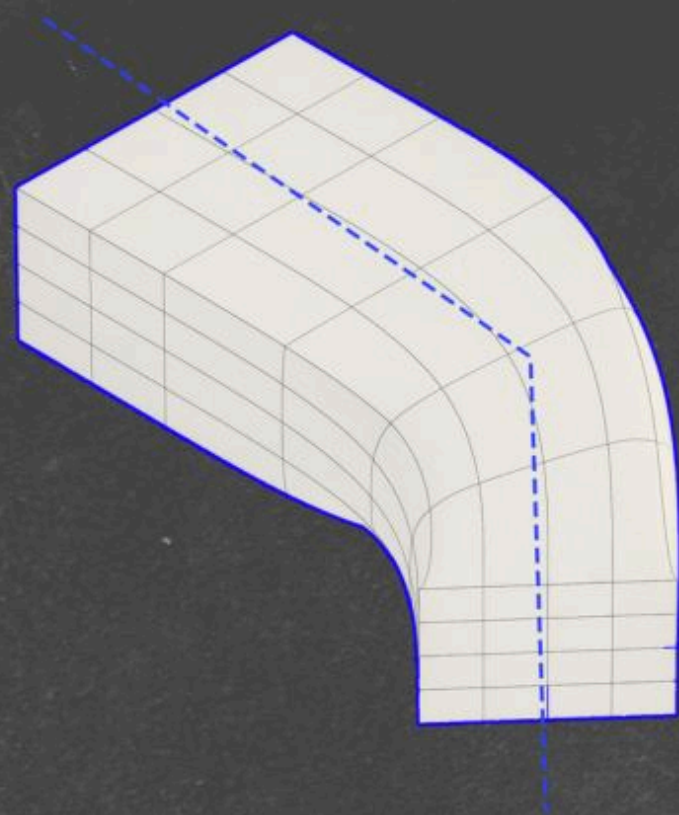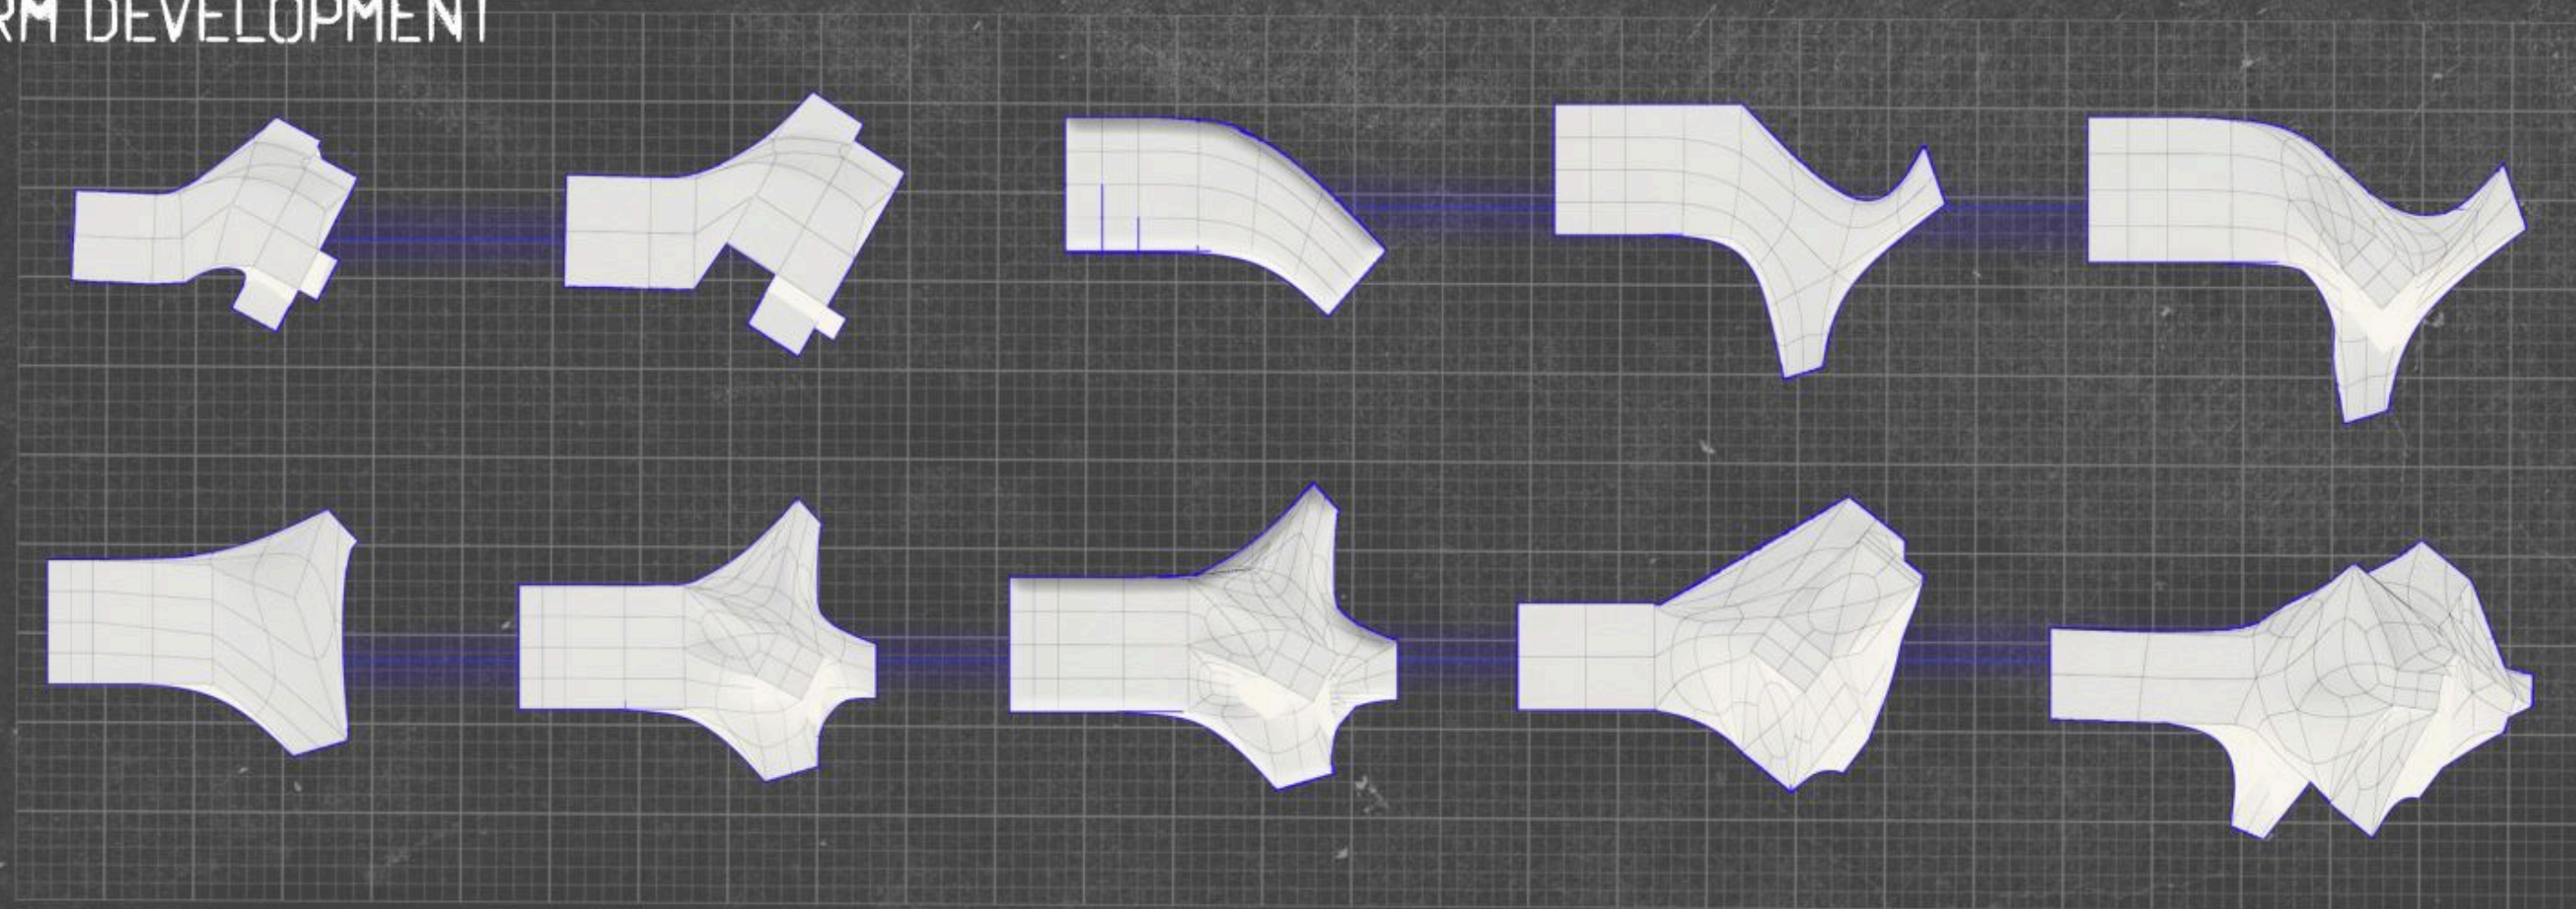


THE FORM GREW FROM EXPERIMENTS IN PULLING, COLLISION, AND TENSION. I TESTED HOW THE BUILDING COULD STRETCH ACROSS THE SITE WHILE STILL RESPECTING THE NARROW PASSAGES AROUND IT. THE SUBD STUDIES HELPED ARTICULATE A FORM THAT FEELS BOTH ANCHORED AND LIFTED, SHAPED BY FORCES ACTING FROM MULTIPLE DIRECTIONS. THESE ITERATIONS SET THE GROUNDWORK FOR A BUILDING THAT BEHAVES LIKE AN INTERSTITIAL ORGANISM, REACTIVE, LAYERED, AND CONTINUOUSLY NEGOTIATING ITS BOUNDARIES.



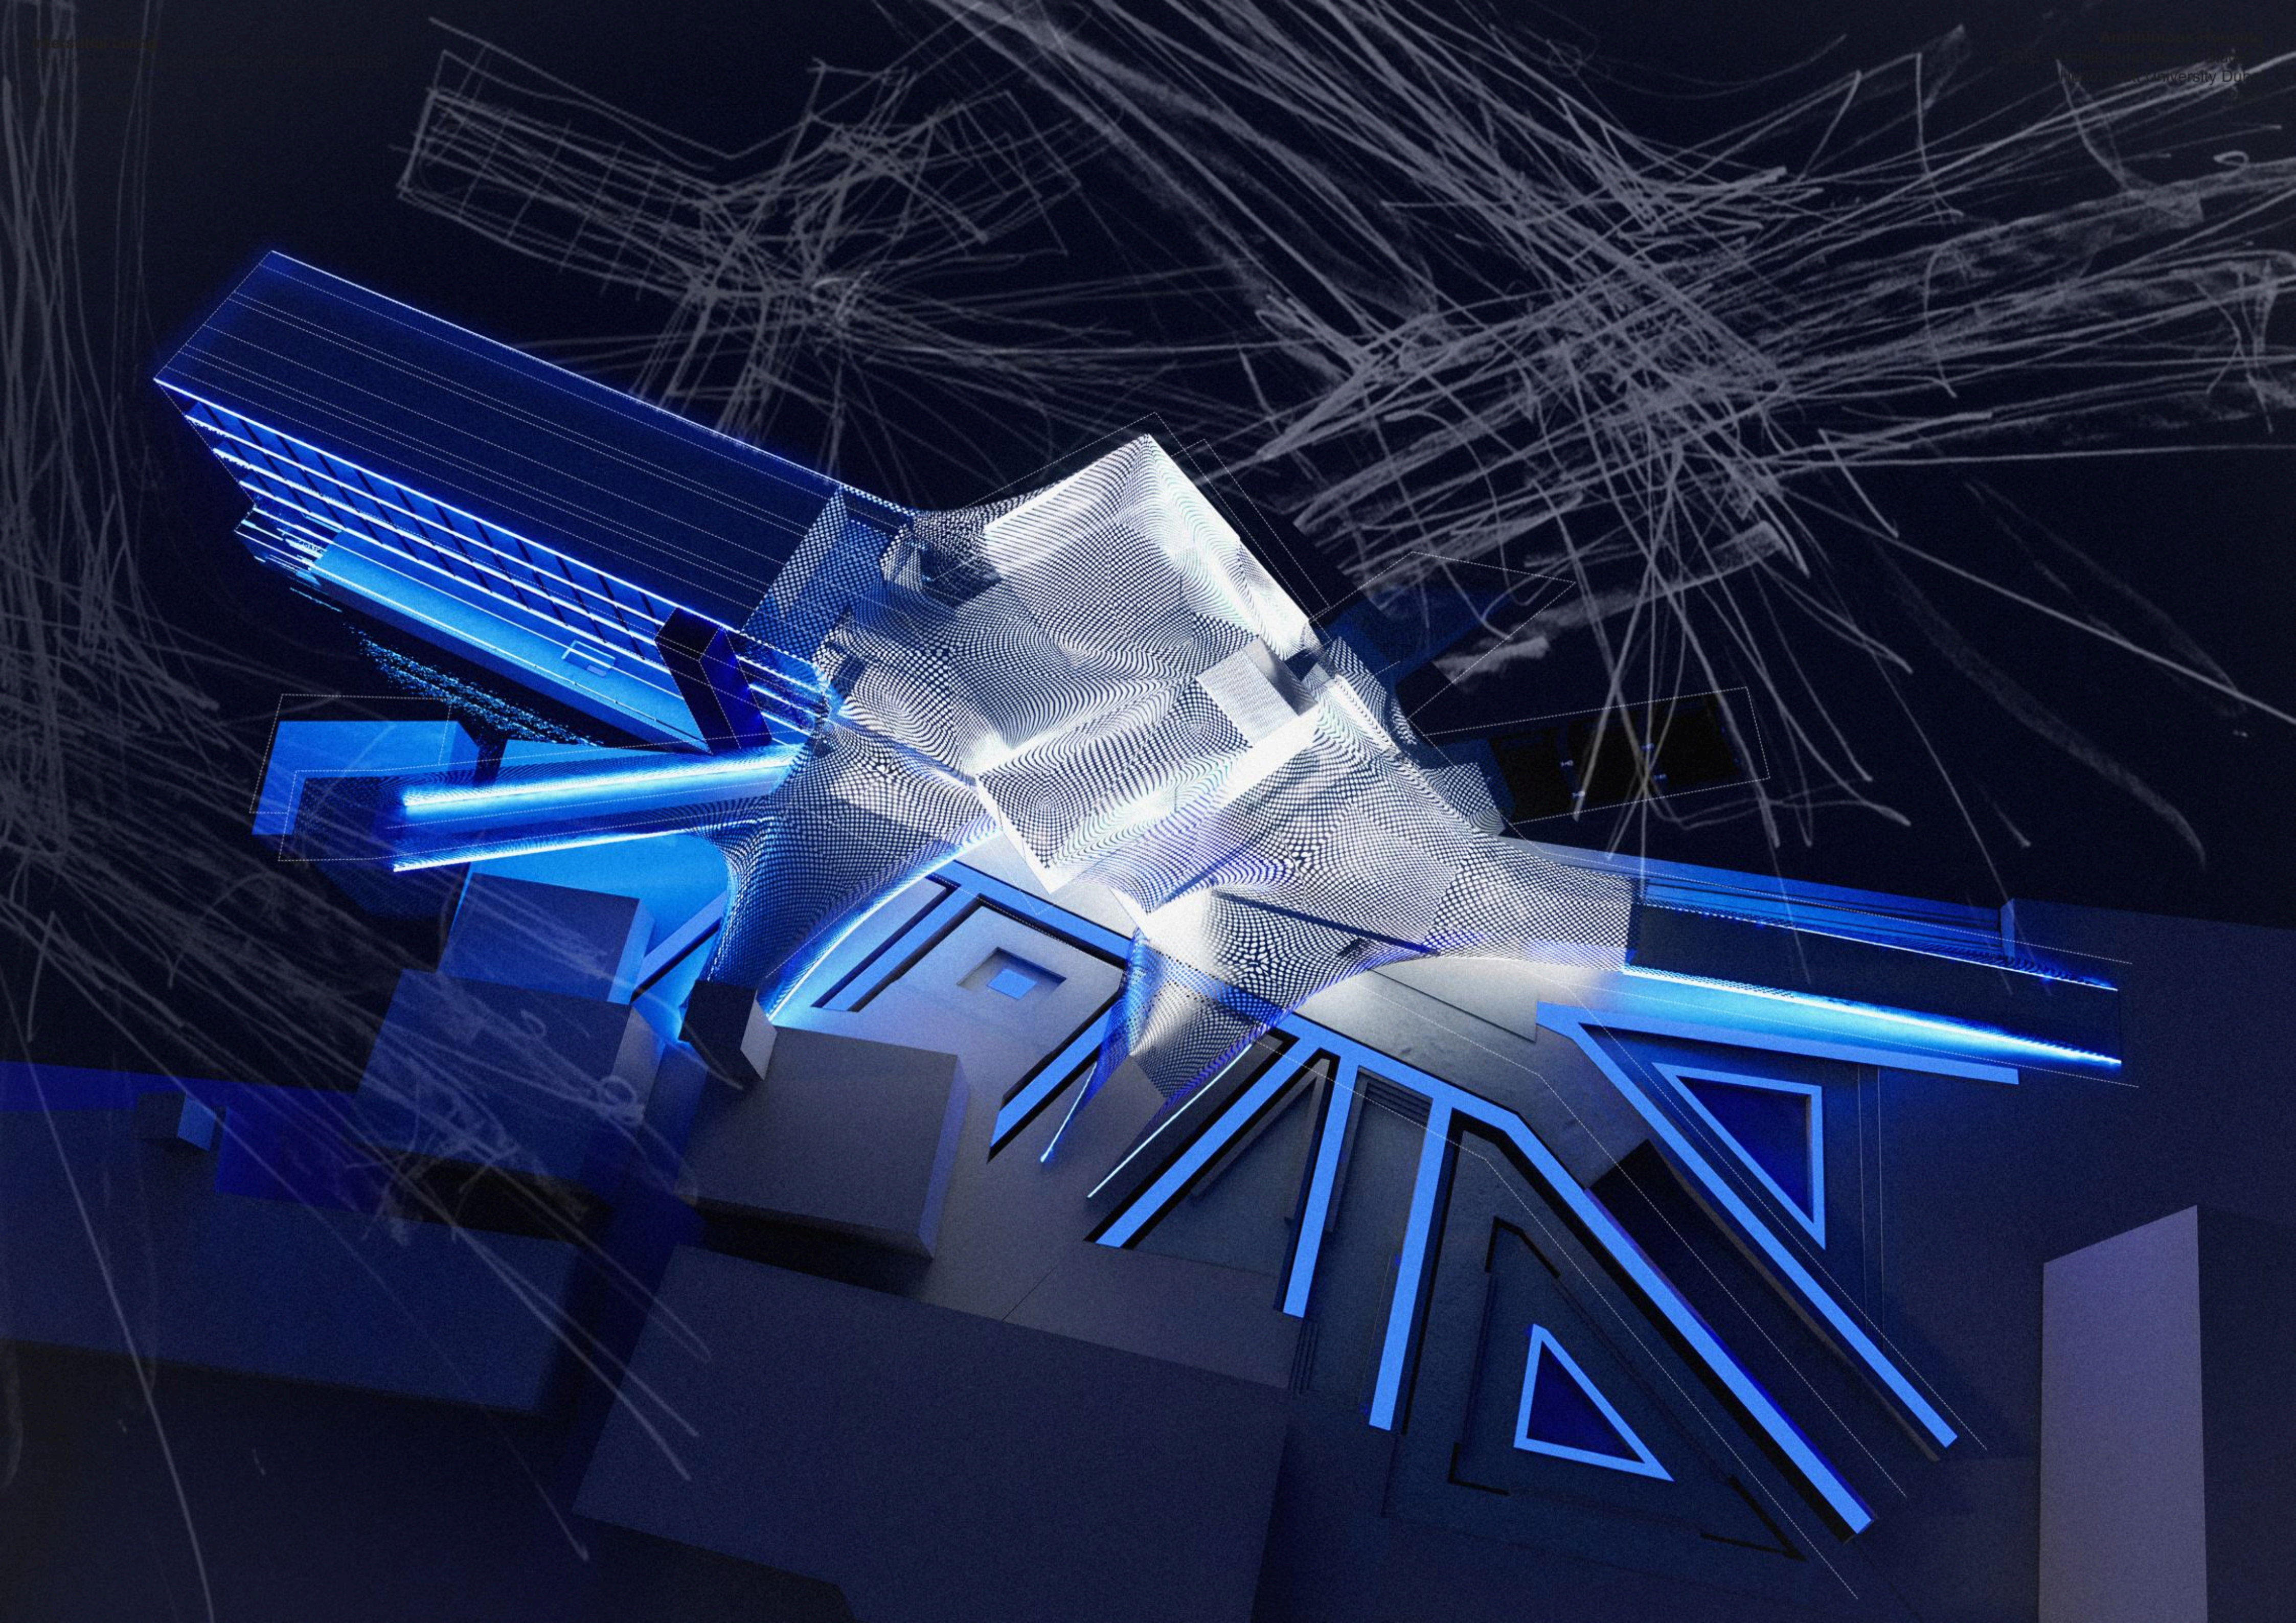


HOUSING UNITS ZONING
SW

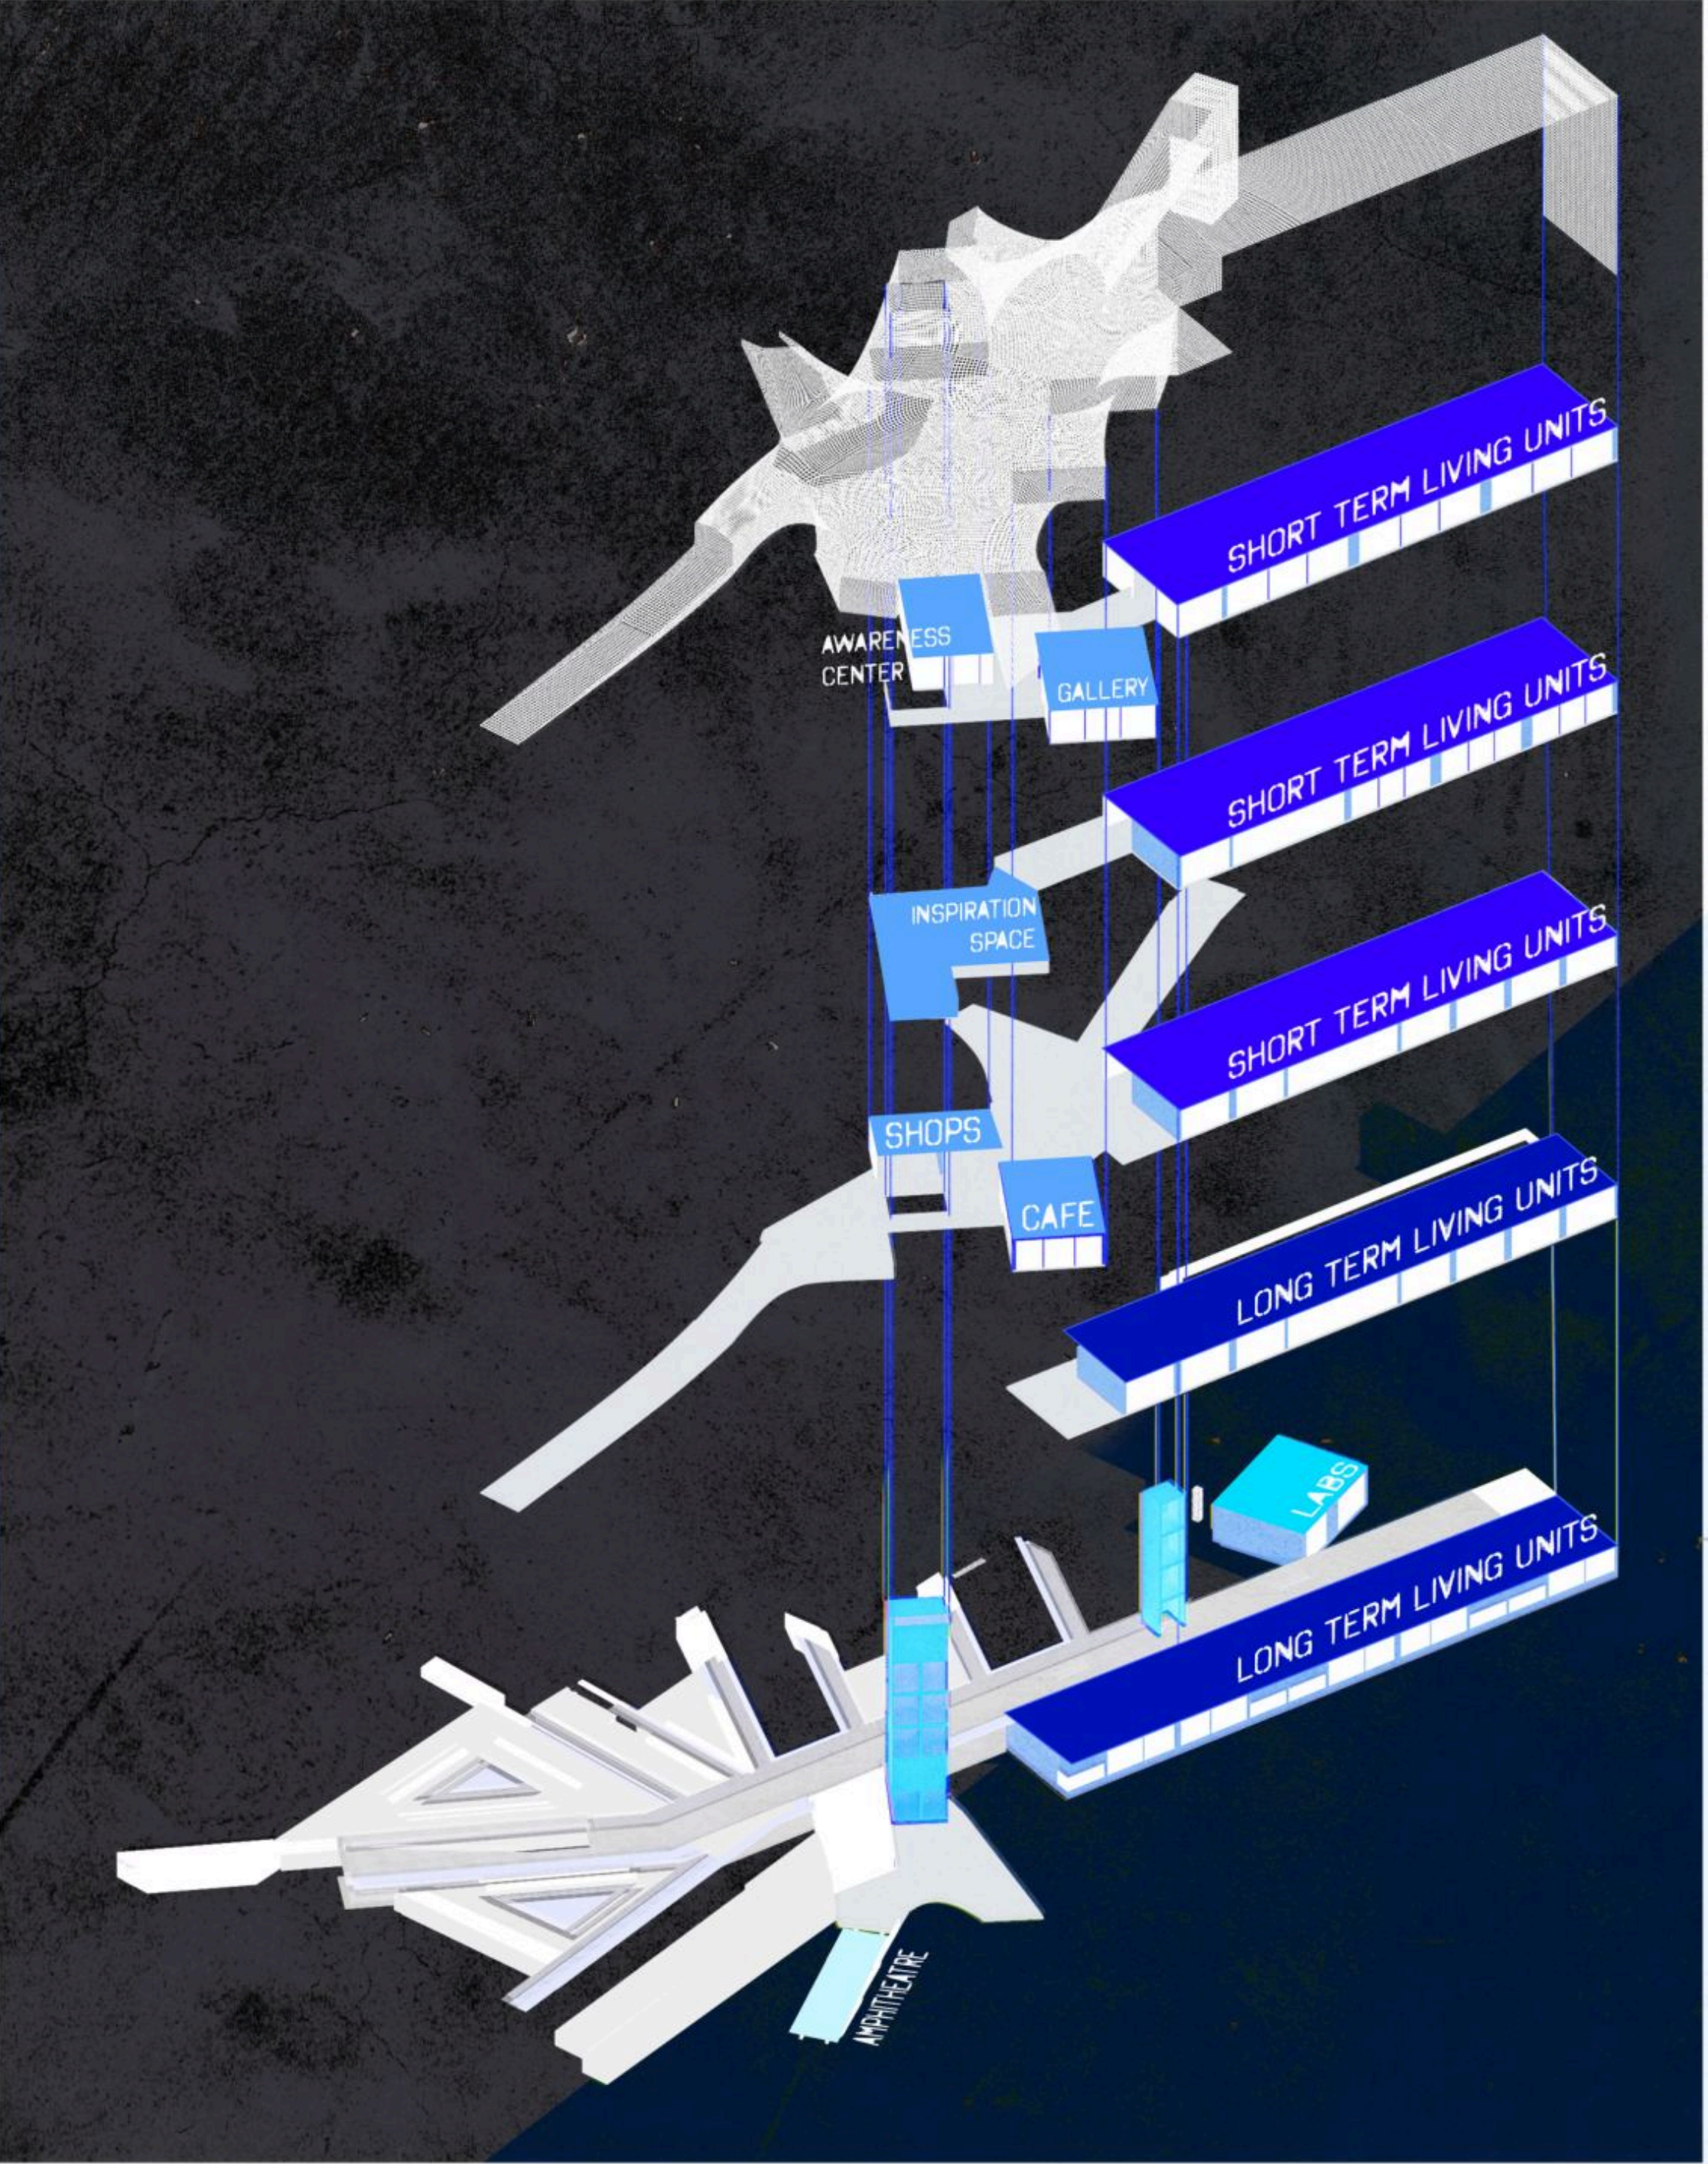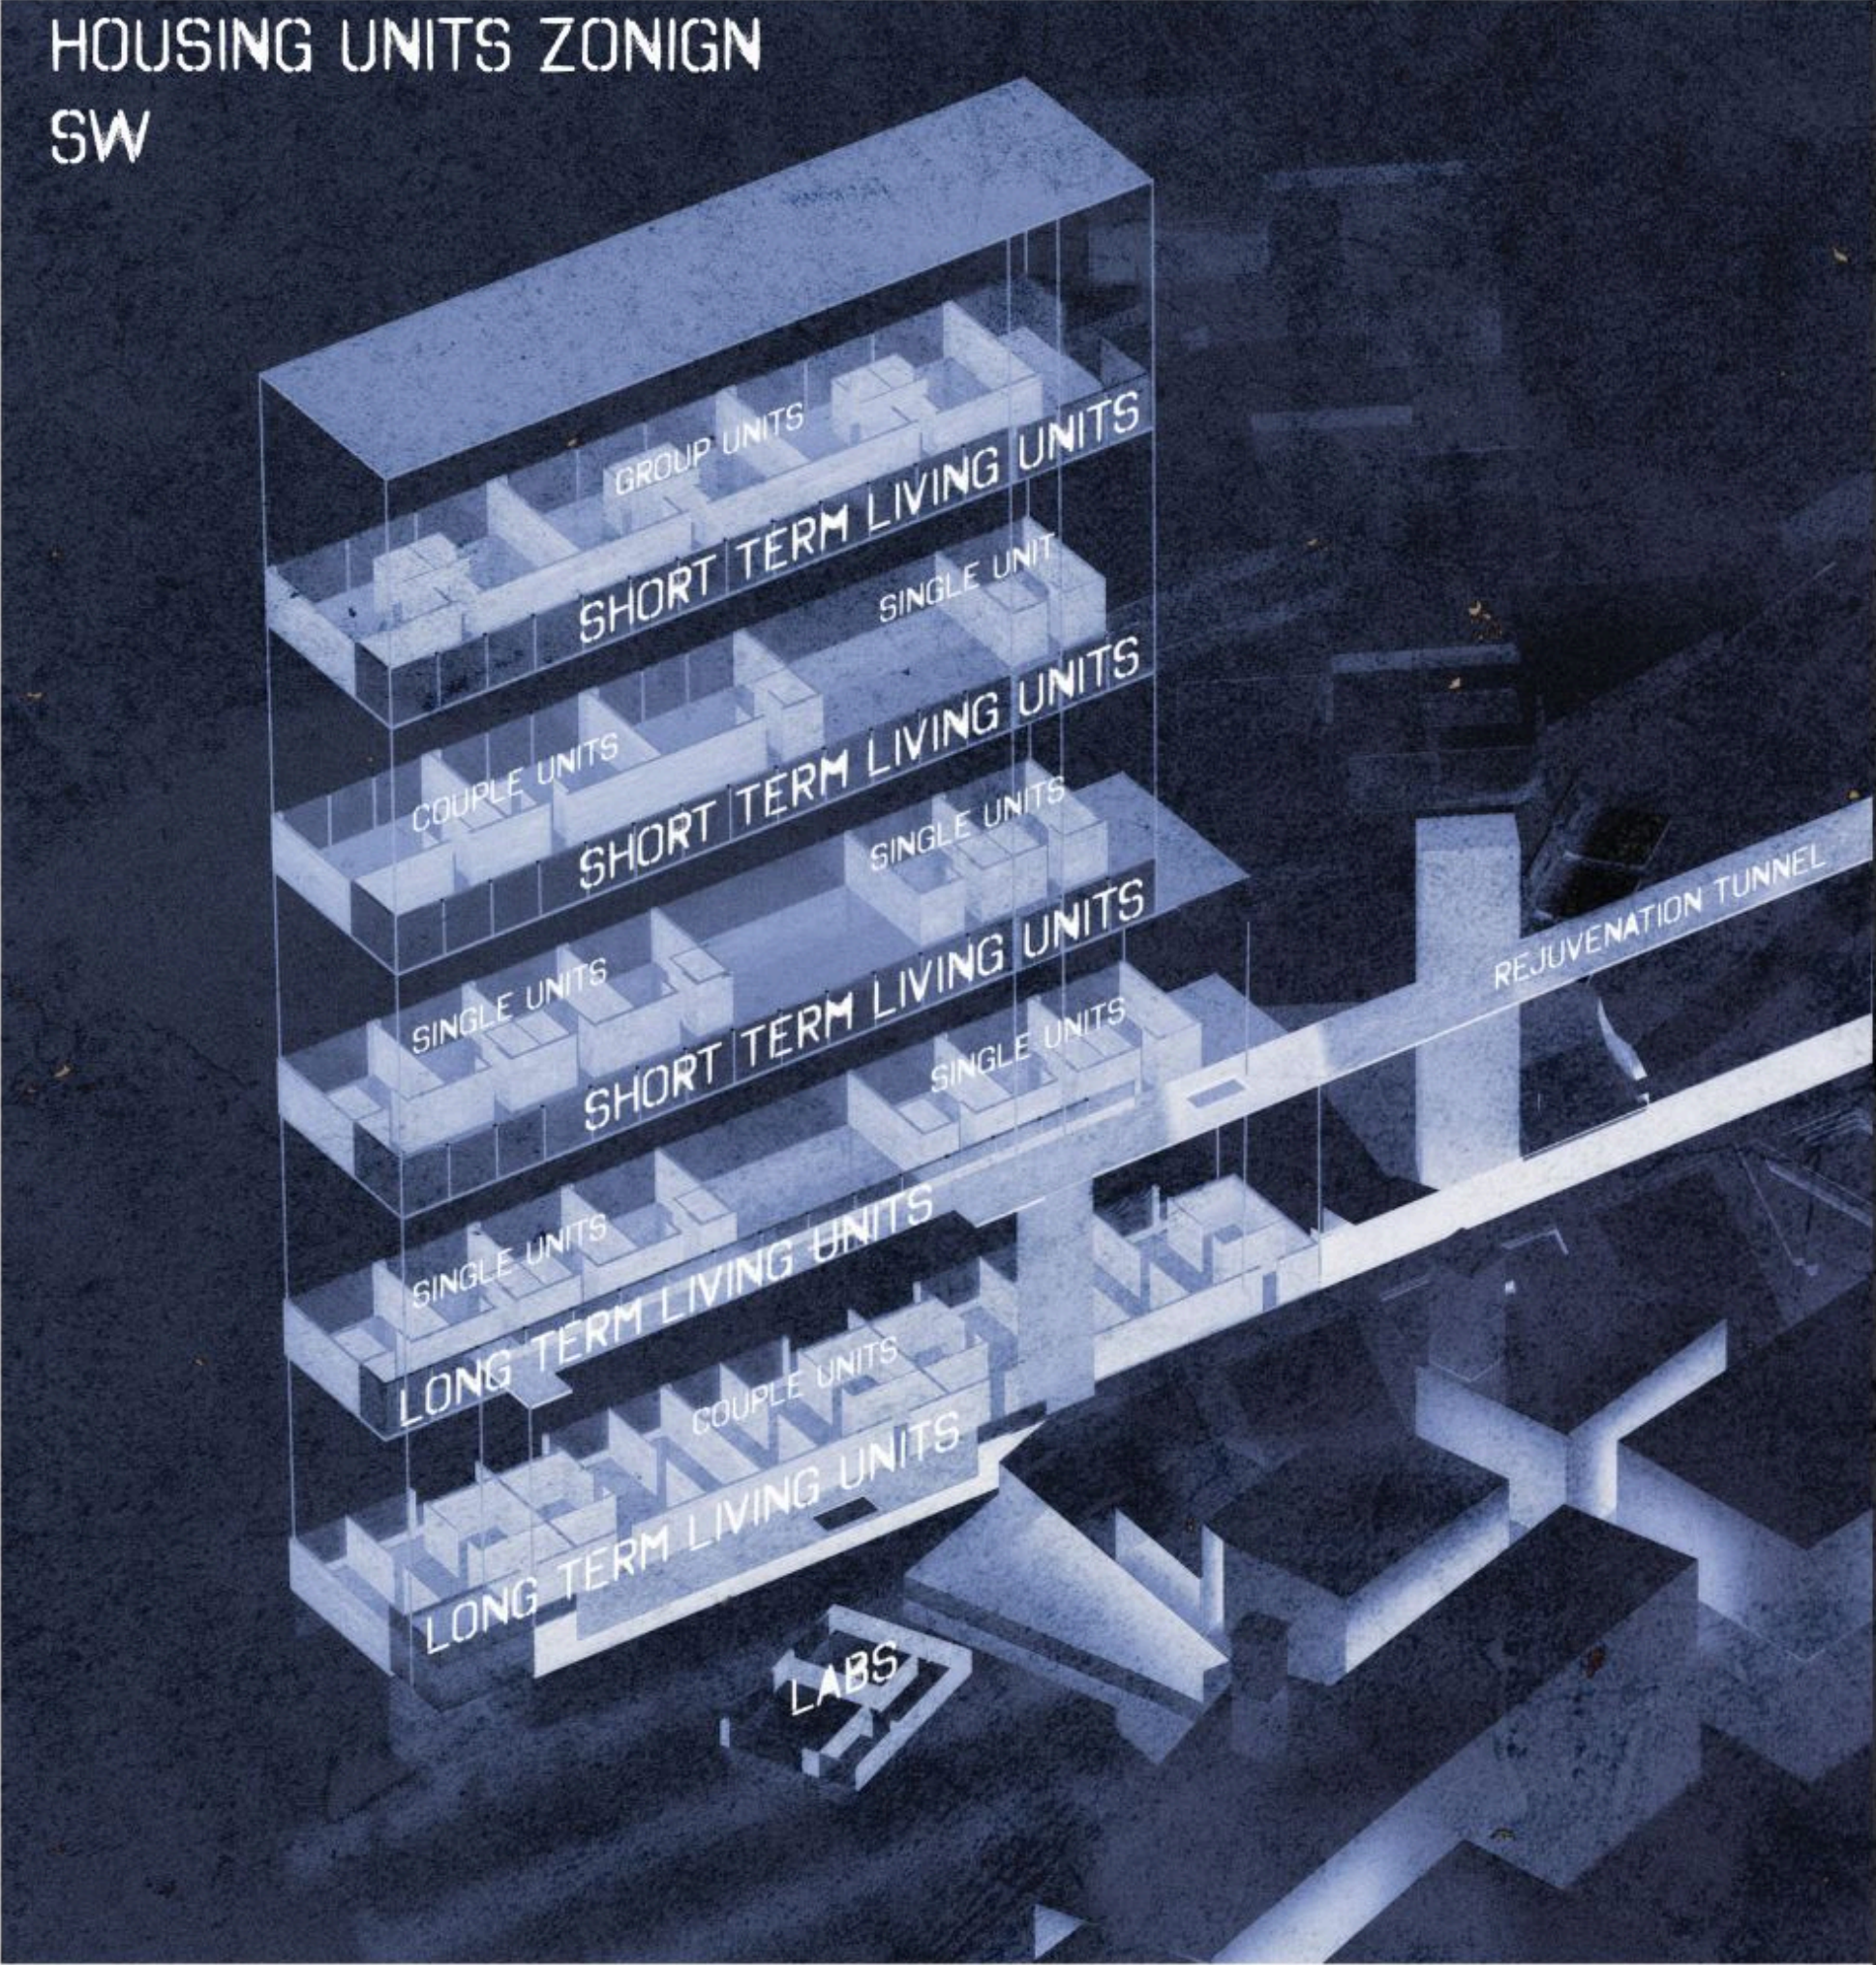


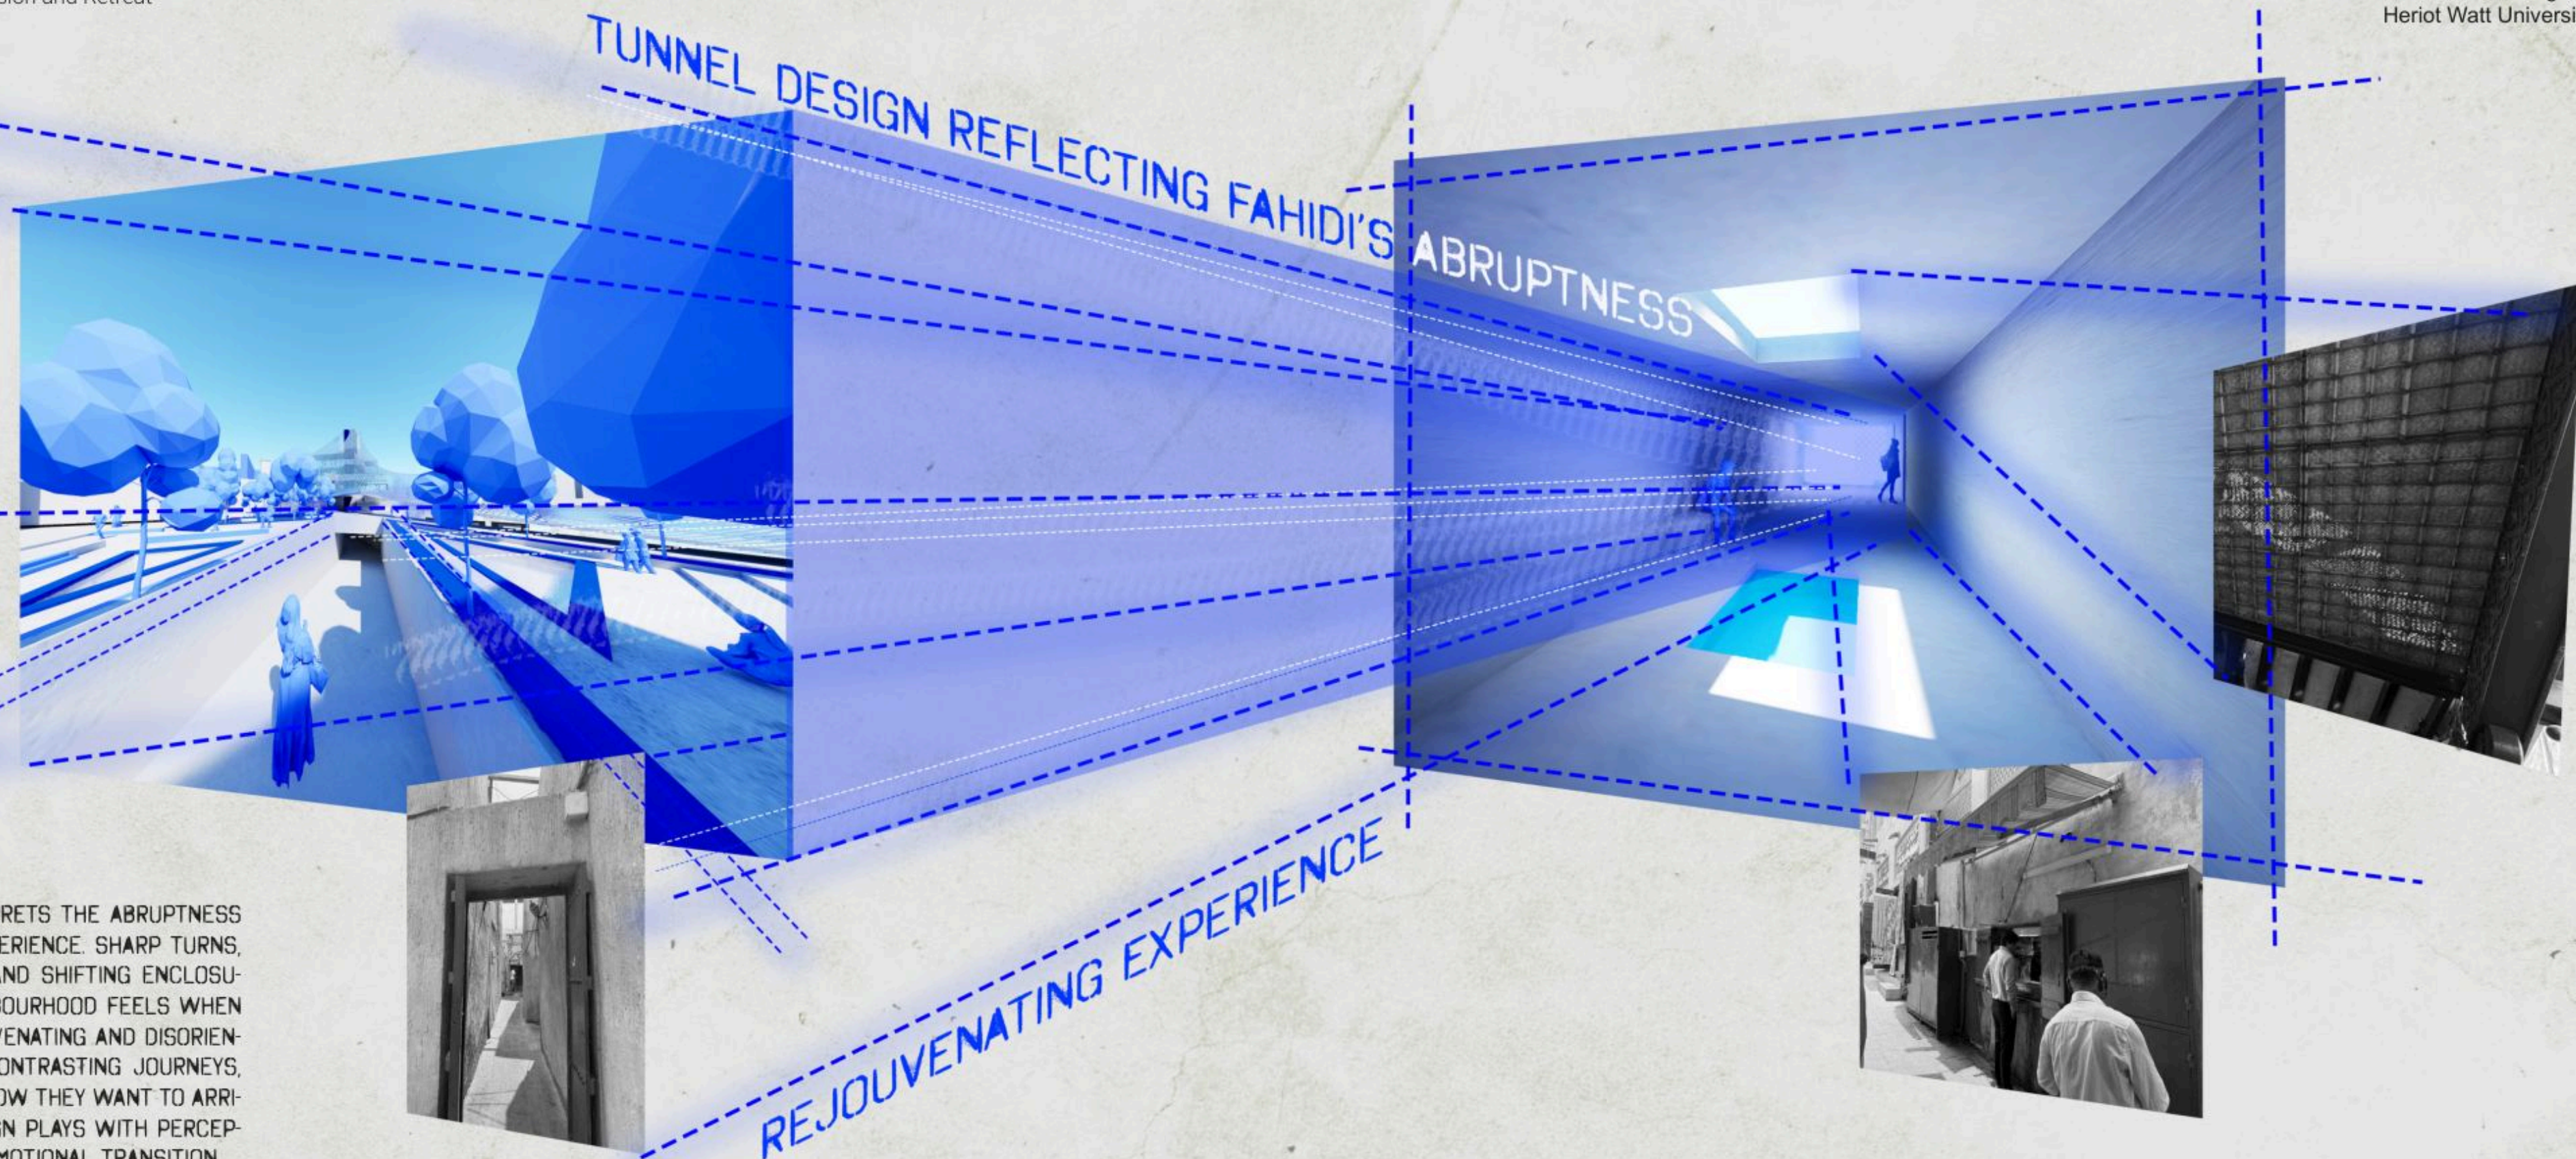


THE TUNNEL SEQUENCE INTERPRETS THE ABRUPTNESS OF AL FAHIDI AS A SPATIAL EXPERIENCE. SHARP TURNS, CHANGING LIGHT CONDITIONS, AND SHIFTING ENCLOSURES REFLECT HOW THE NEIGHBOURHOOD FEELS WHEN MOVING THROUGH IT. THE REJUVENATING AND DISORIENTING PATHWAYS OFFER TWO CONTRASTING JOURNEYS, ALLOWING USERS TO CHOOSE HOW THEY WANT TO ARRIVE AT THE BUILDING. THE DESIGN PLAYS WITH PERCEPTION, FRAMING ARRIVAL AS AN EMOTIONAL TRANSITION.

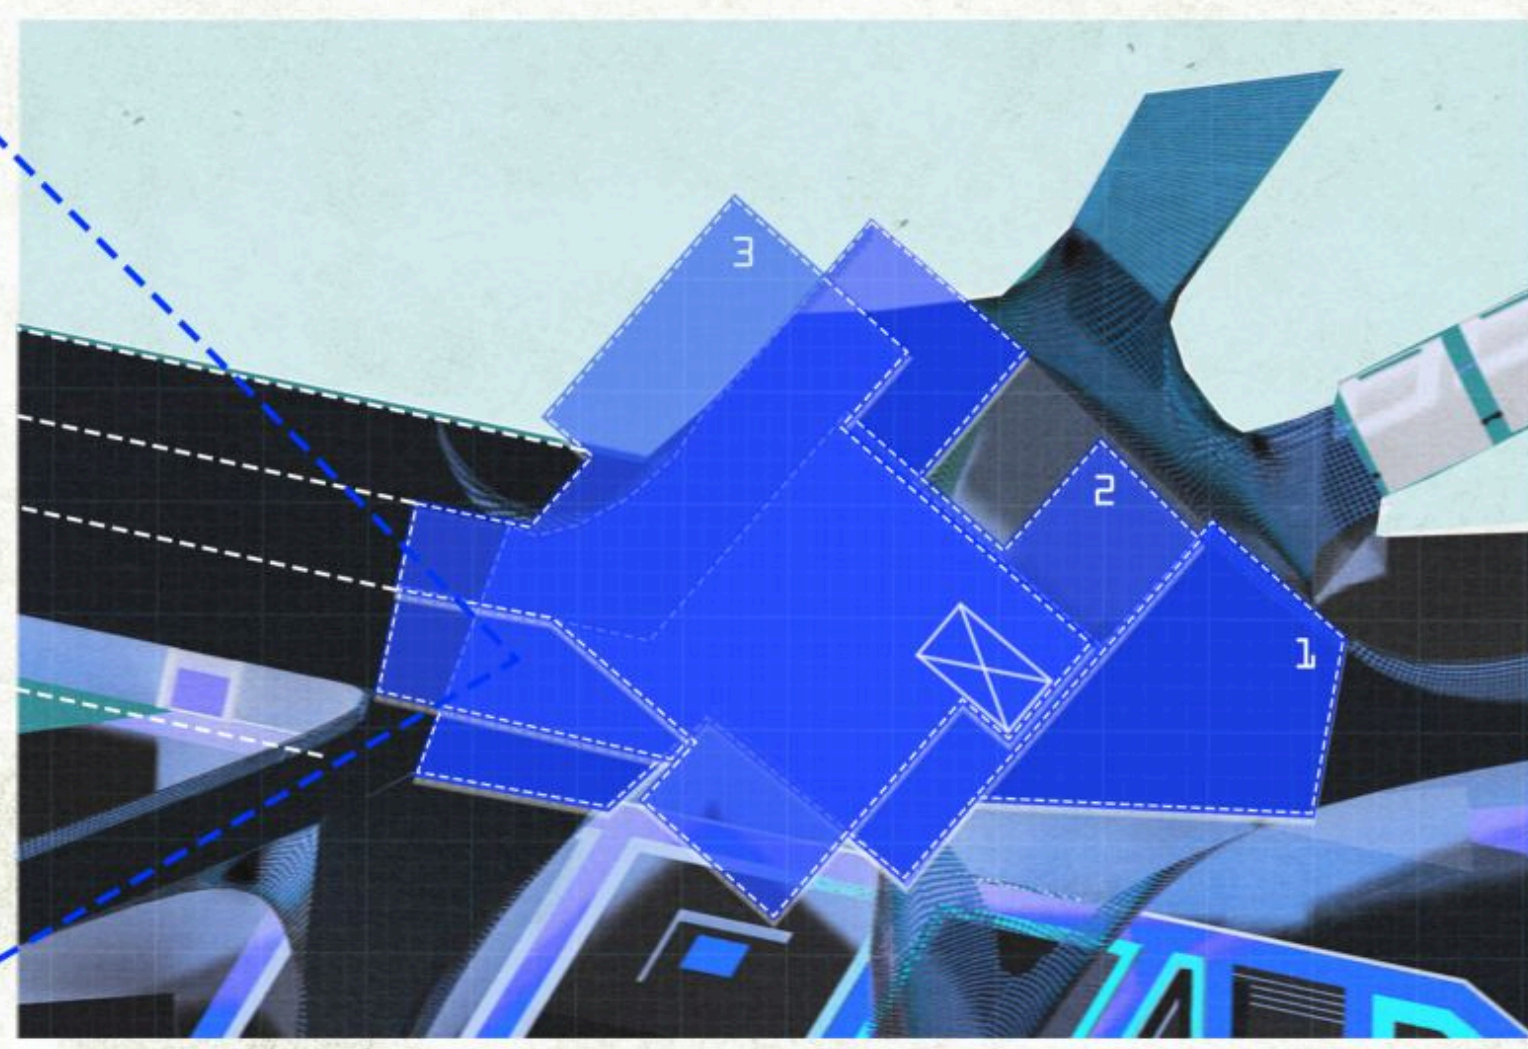
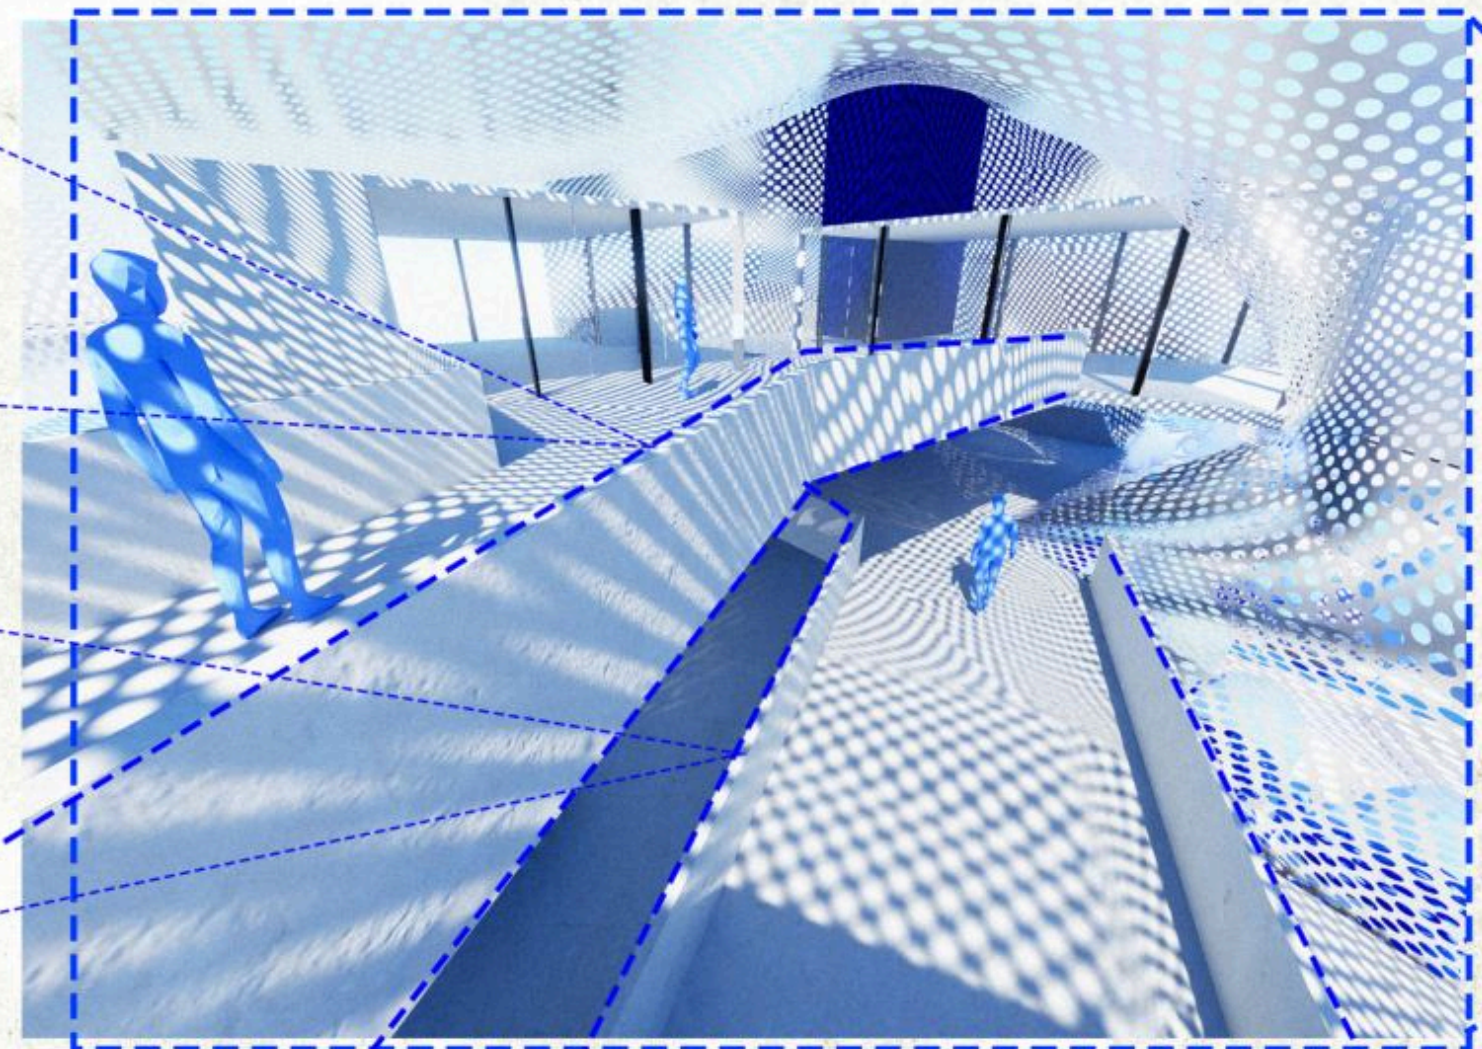
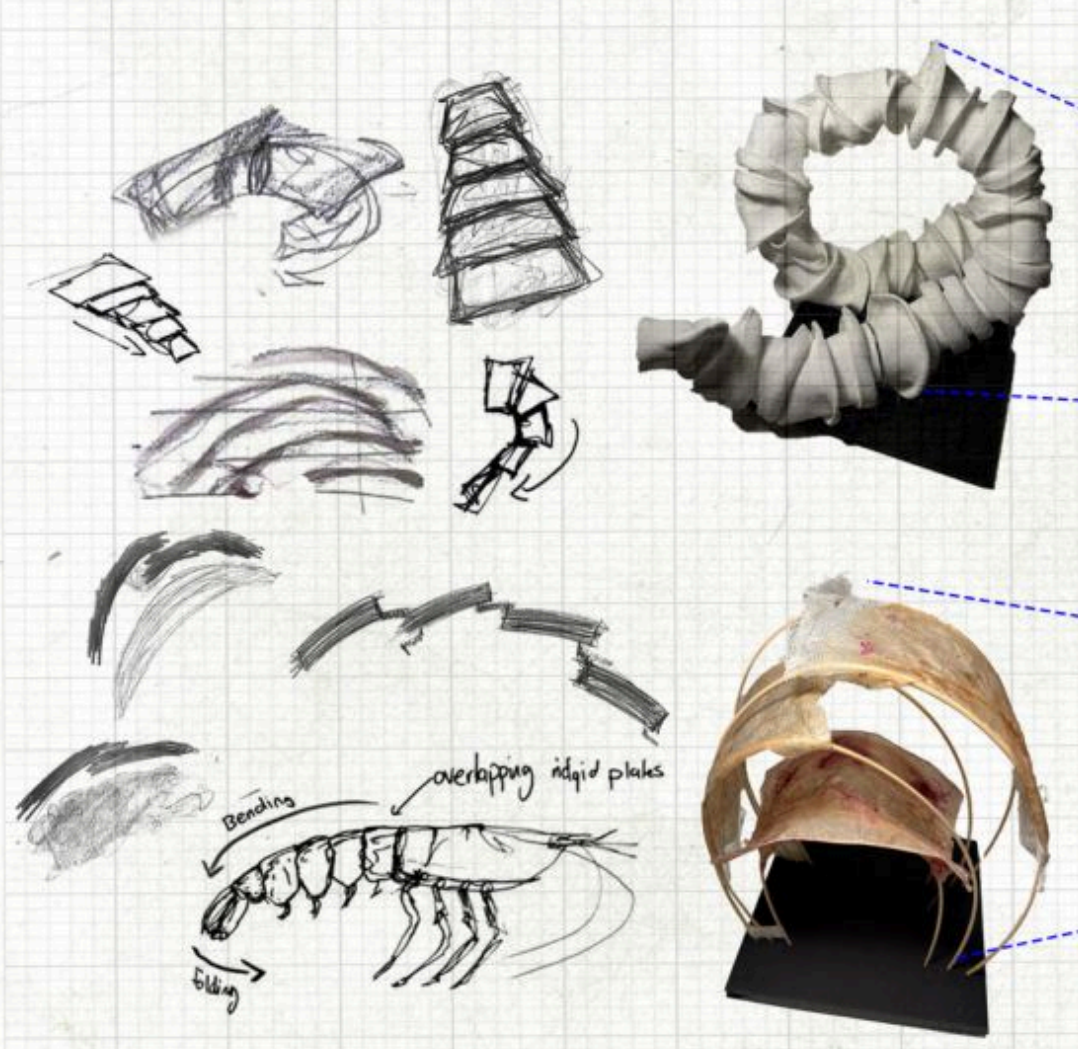


DISORIENTATING EXPERIENCE

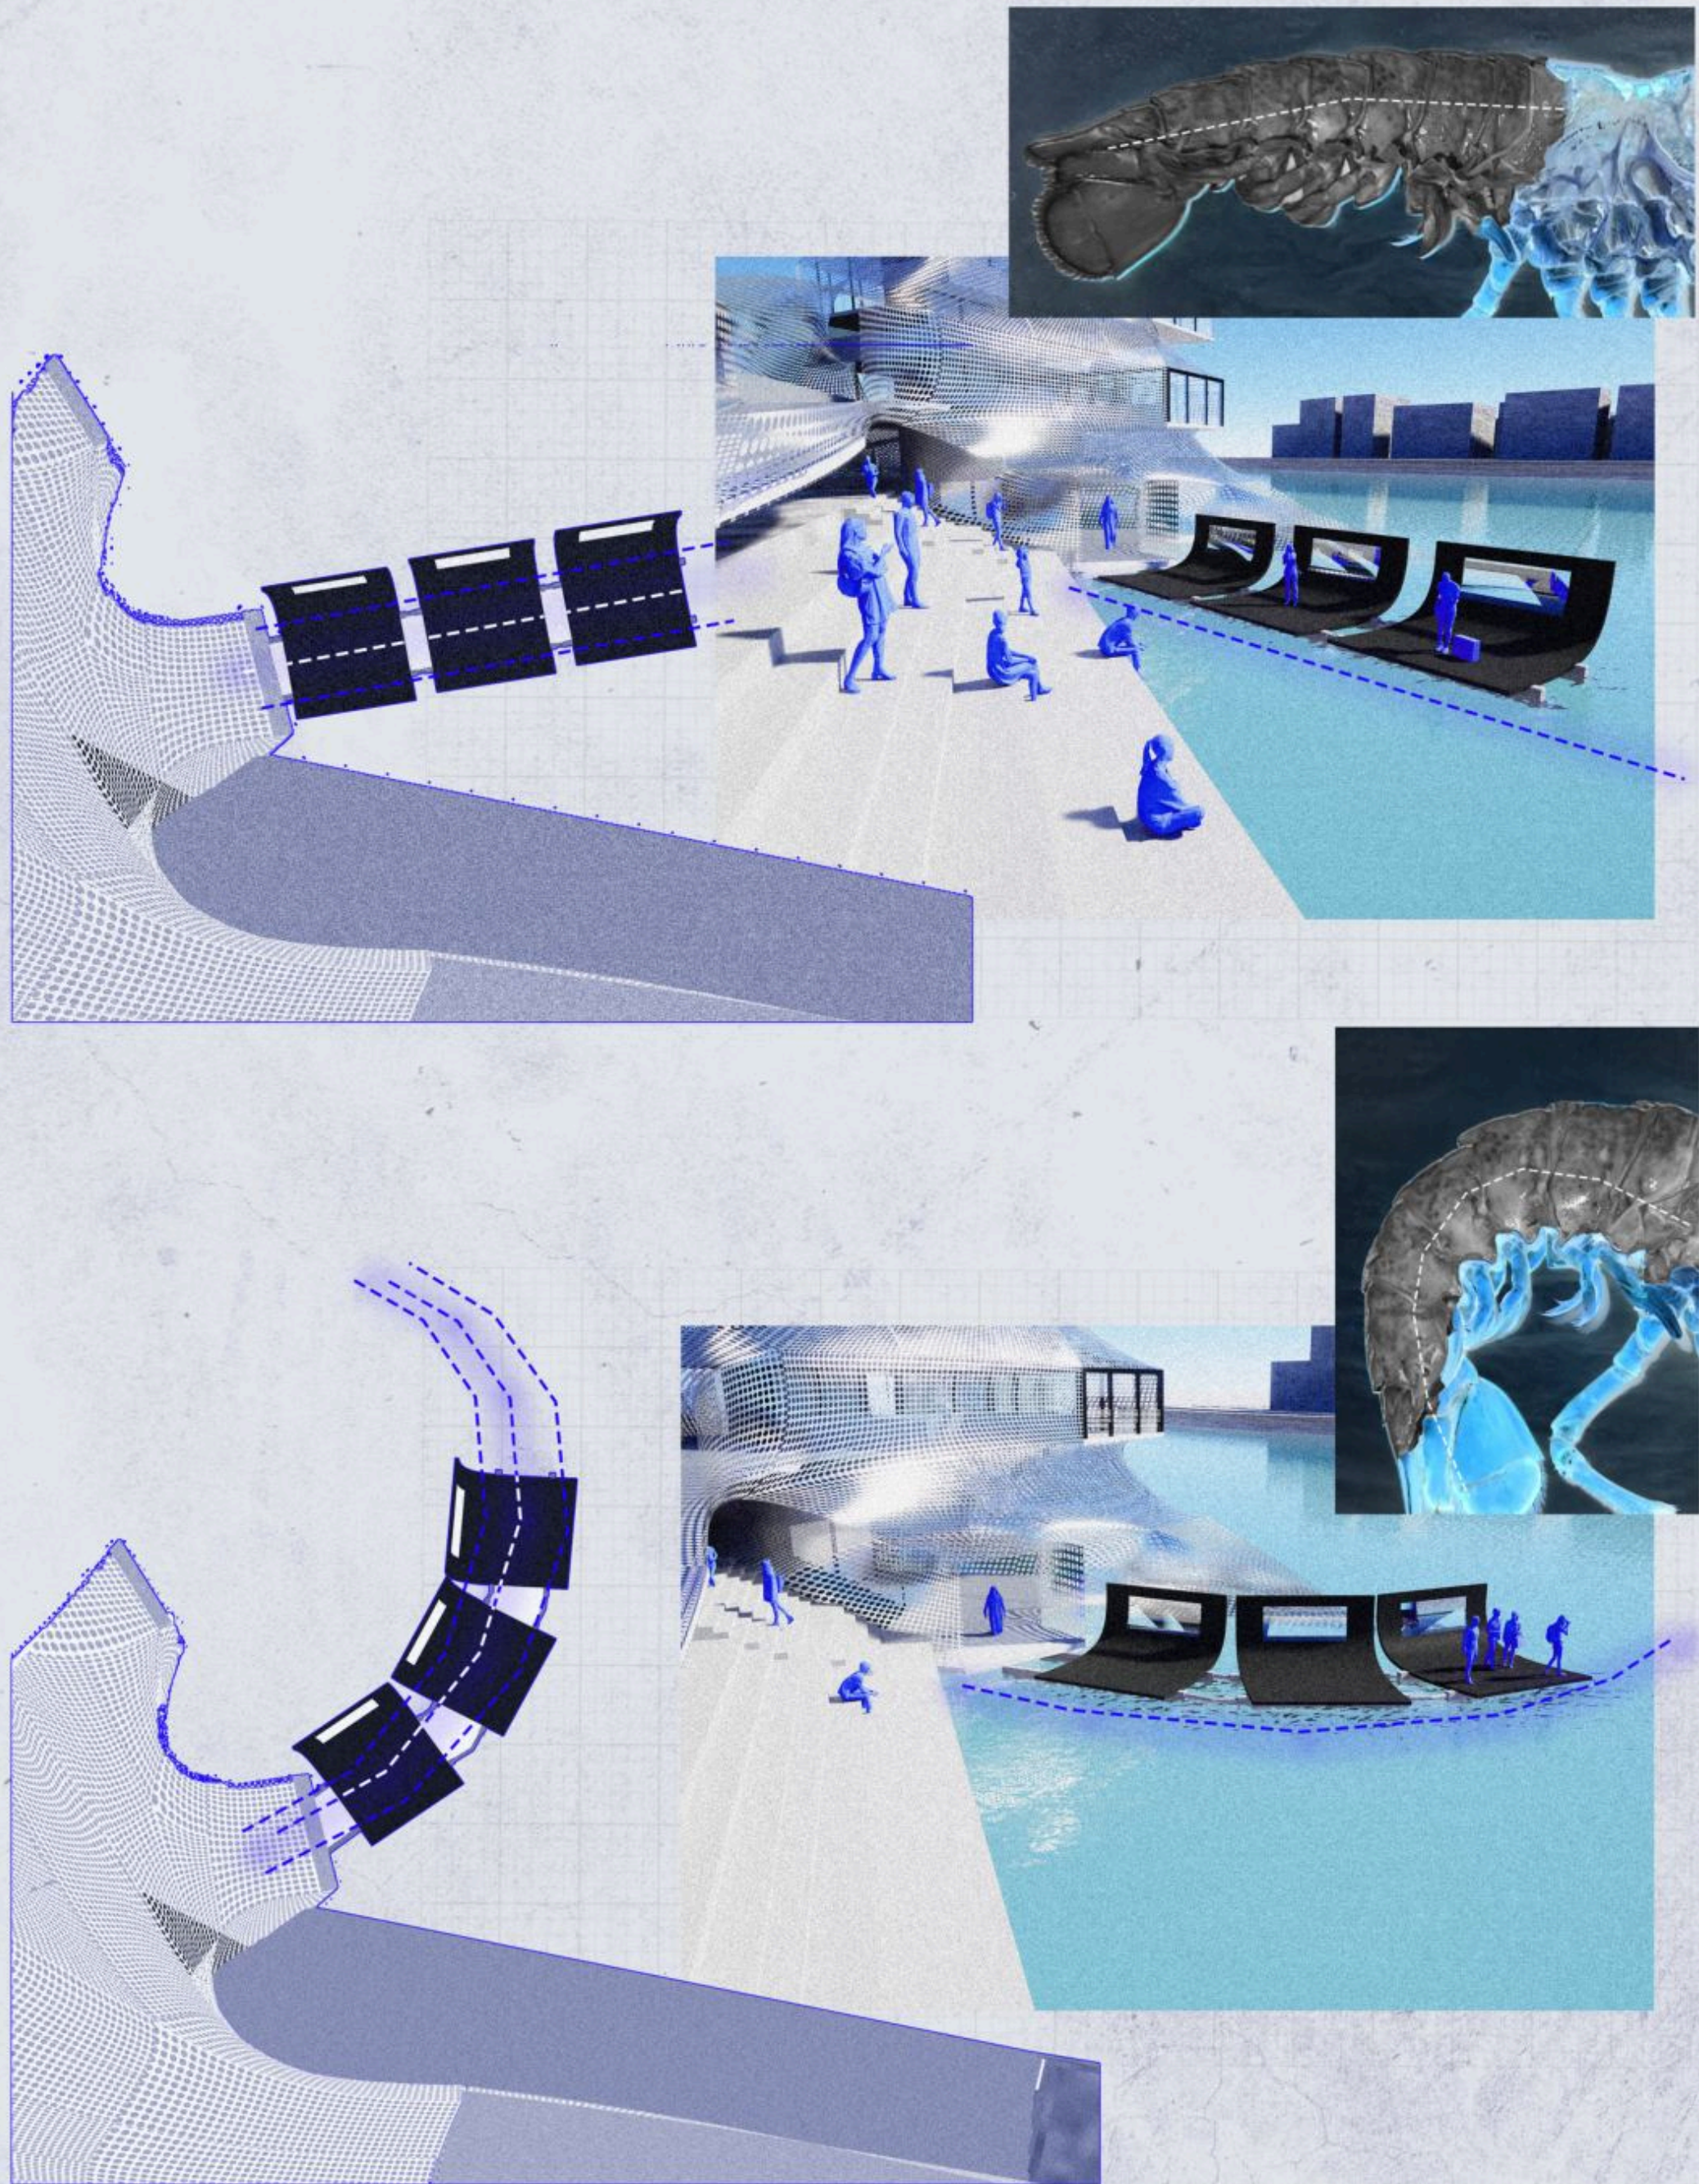


THE AMPHITHEATER TAKES ITS FORM FROM THE LOBSTER'S SEGMENTED MOVEMENT. EACH STEP SHIFTS SLIGHTLY, AS IF THE GROUND ITSELF IS BENDING AND ADJUSTING, CREATING A LANDSCAPE THAT FEELS ACTIVE RATHER THAN STATIC. THESE SEGMENTS PULL VISITORS TOWARD THE CENTRE, WHERE THE FEELING OF AMBIVALENT BELONGING BECOMES STRONGEST, CAUGHT BETWEEN BEING PART OF THE NEIGHBOURHOOD AND MOMENTARILY APART FROM IT. THE LANDSCAPE MIRRORS THE BUILDING'S OWN PULLED AND PINCHED GEOMETRY, GUIDING PEOPLE INTO A SHARED MIDDLE GROUND SHAPED BY BOTH MOTION AND PAUSE.

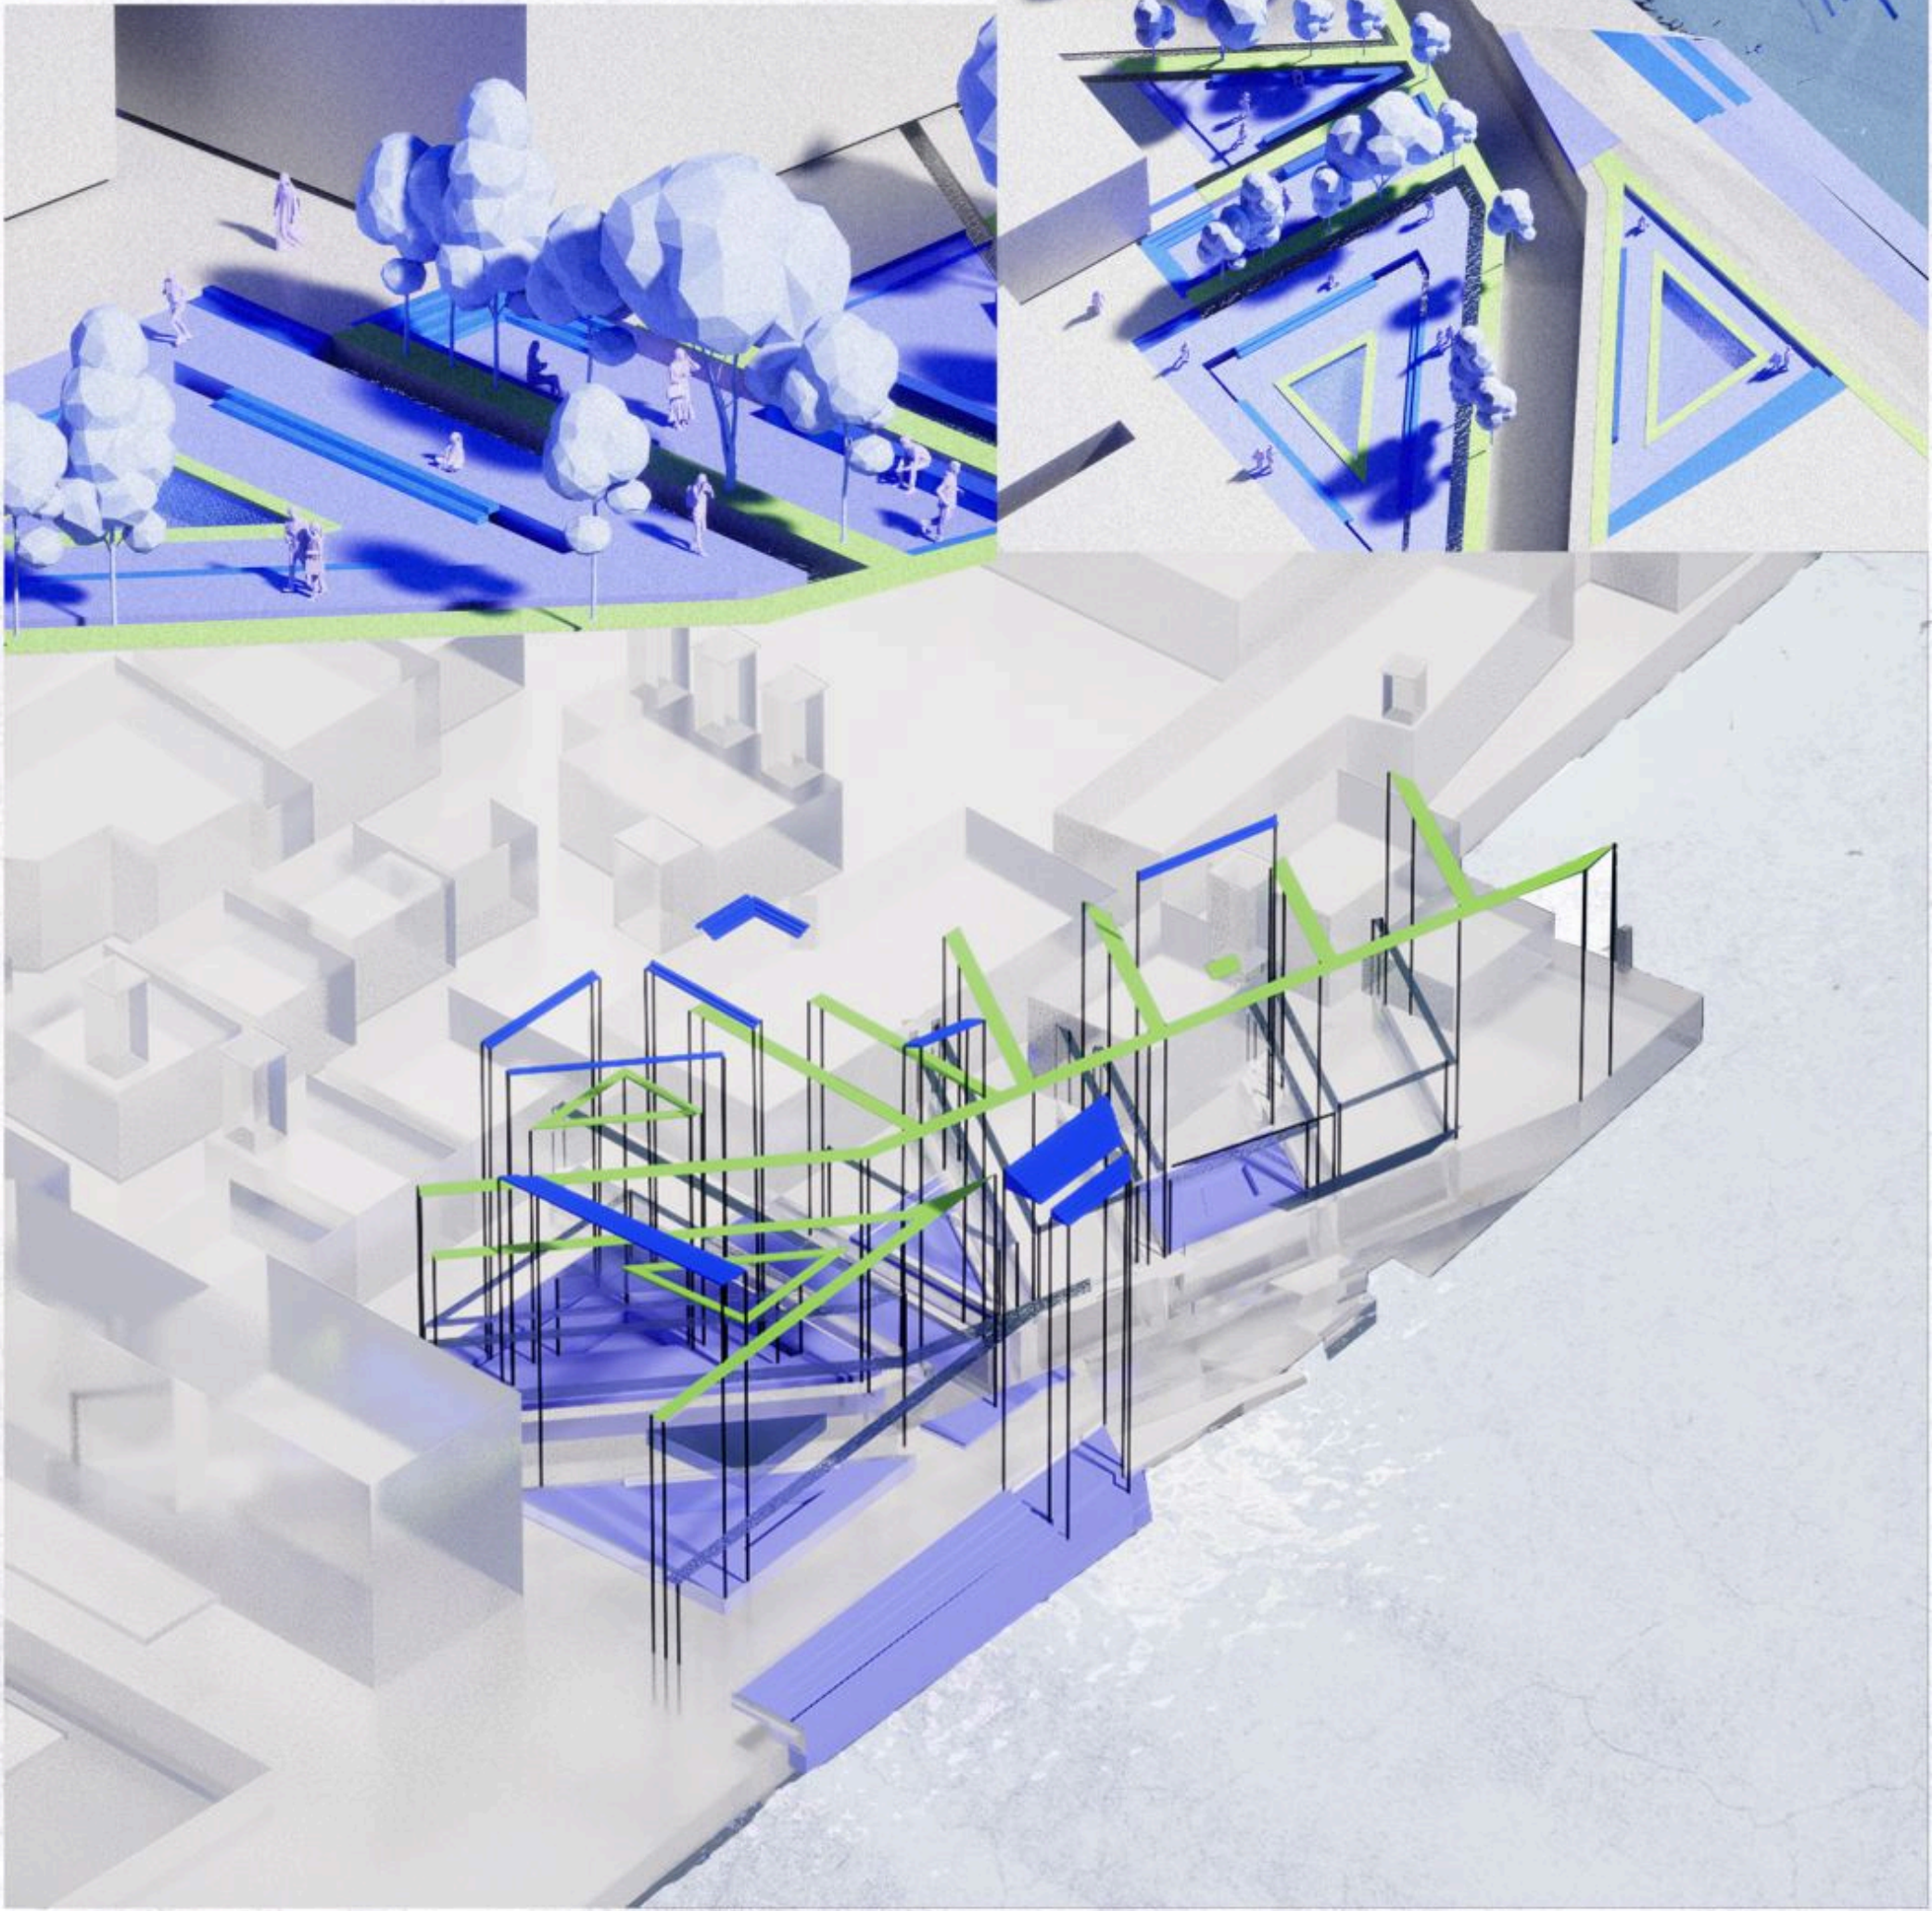

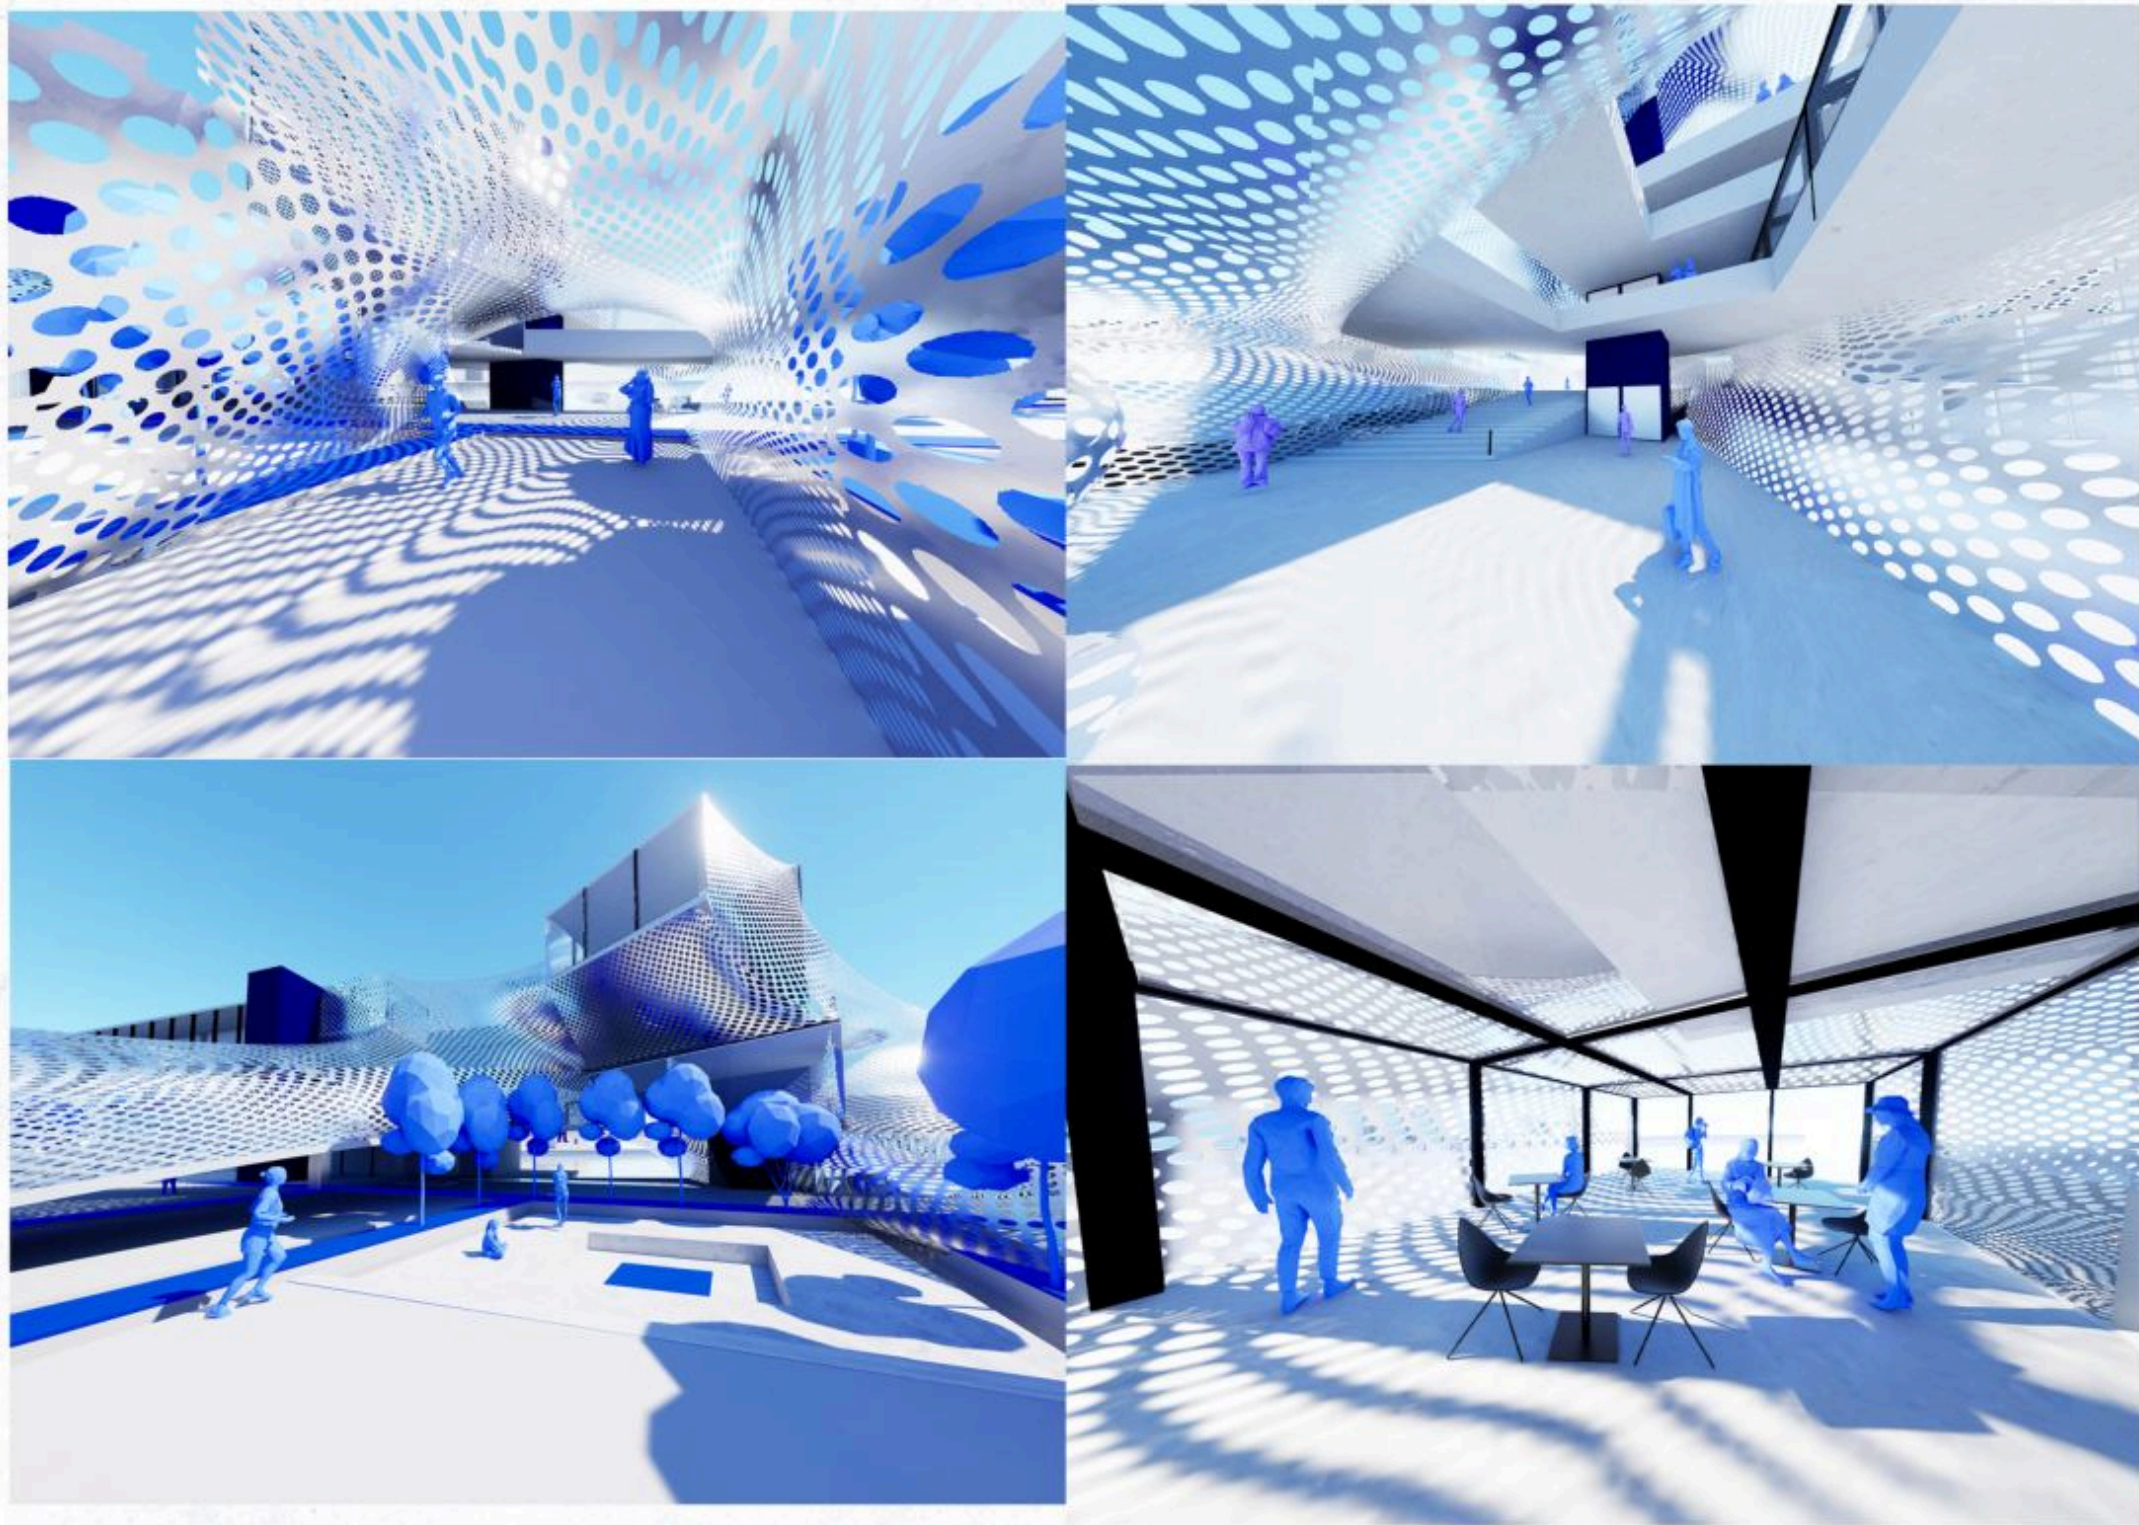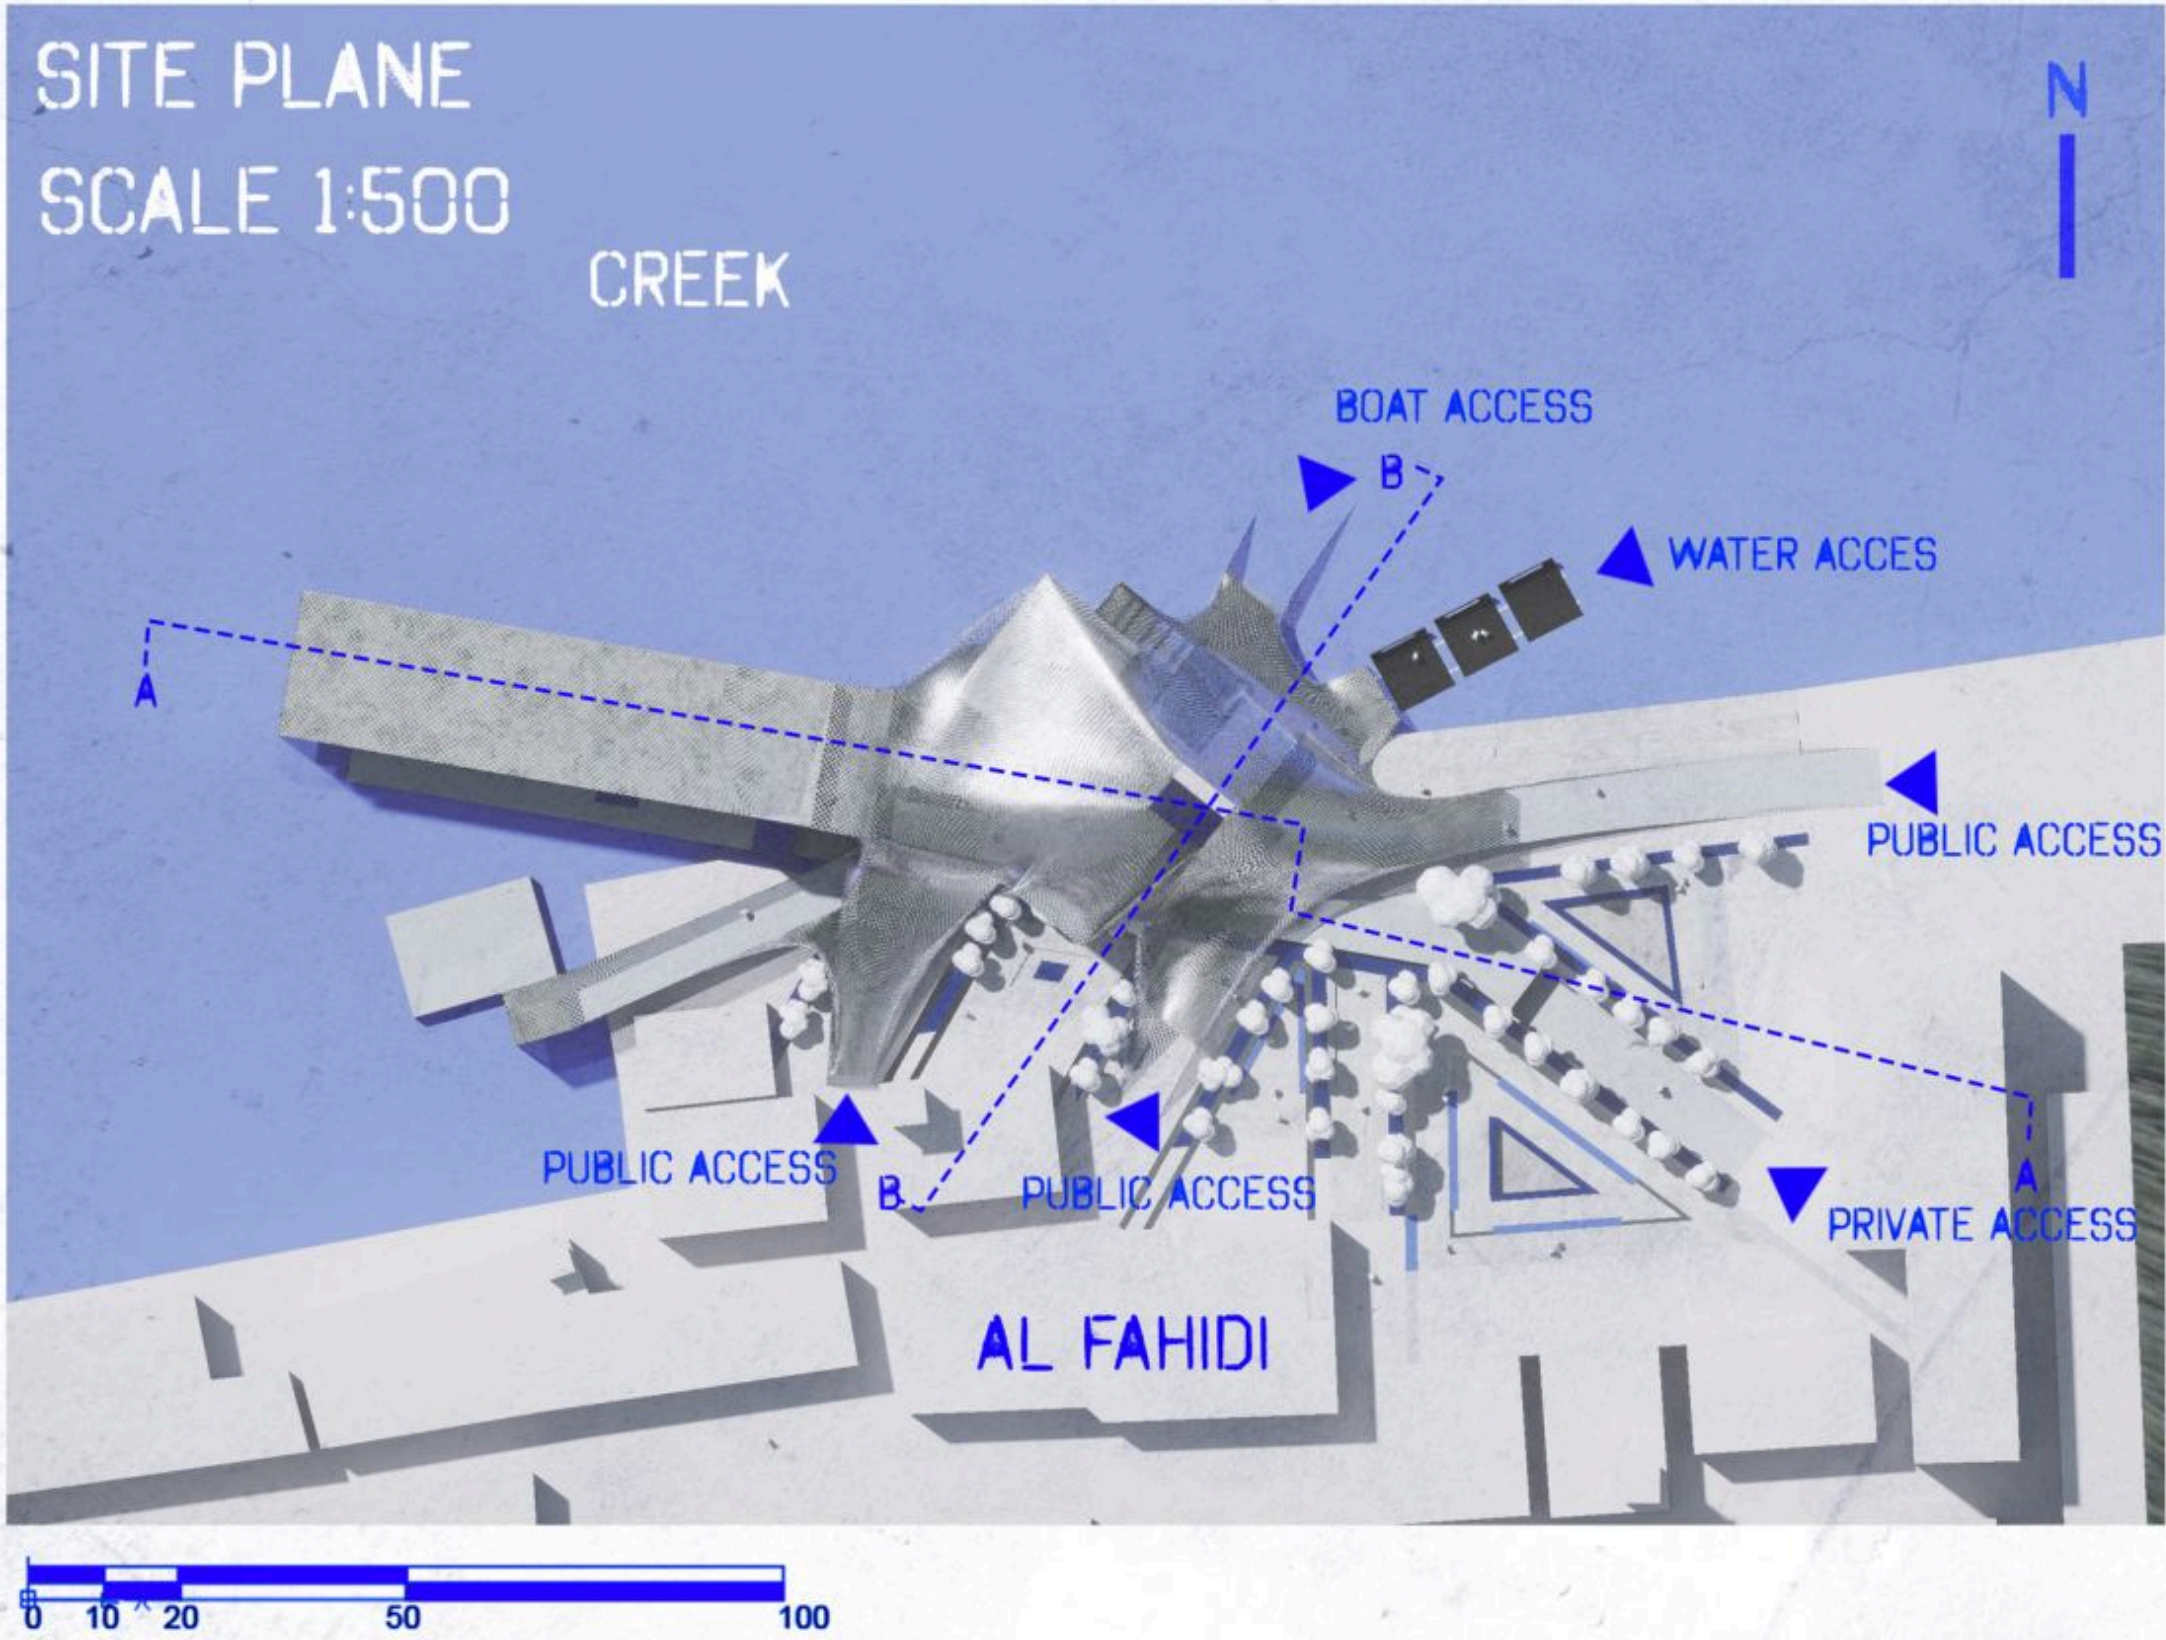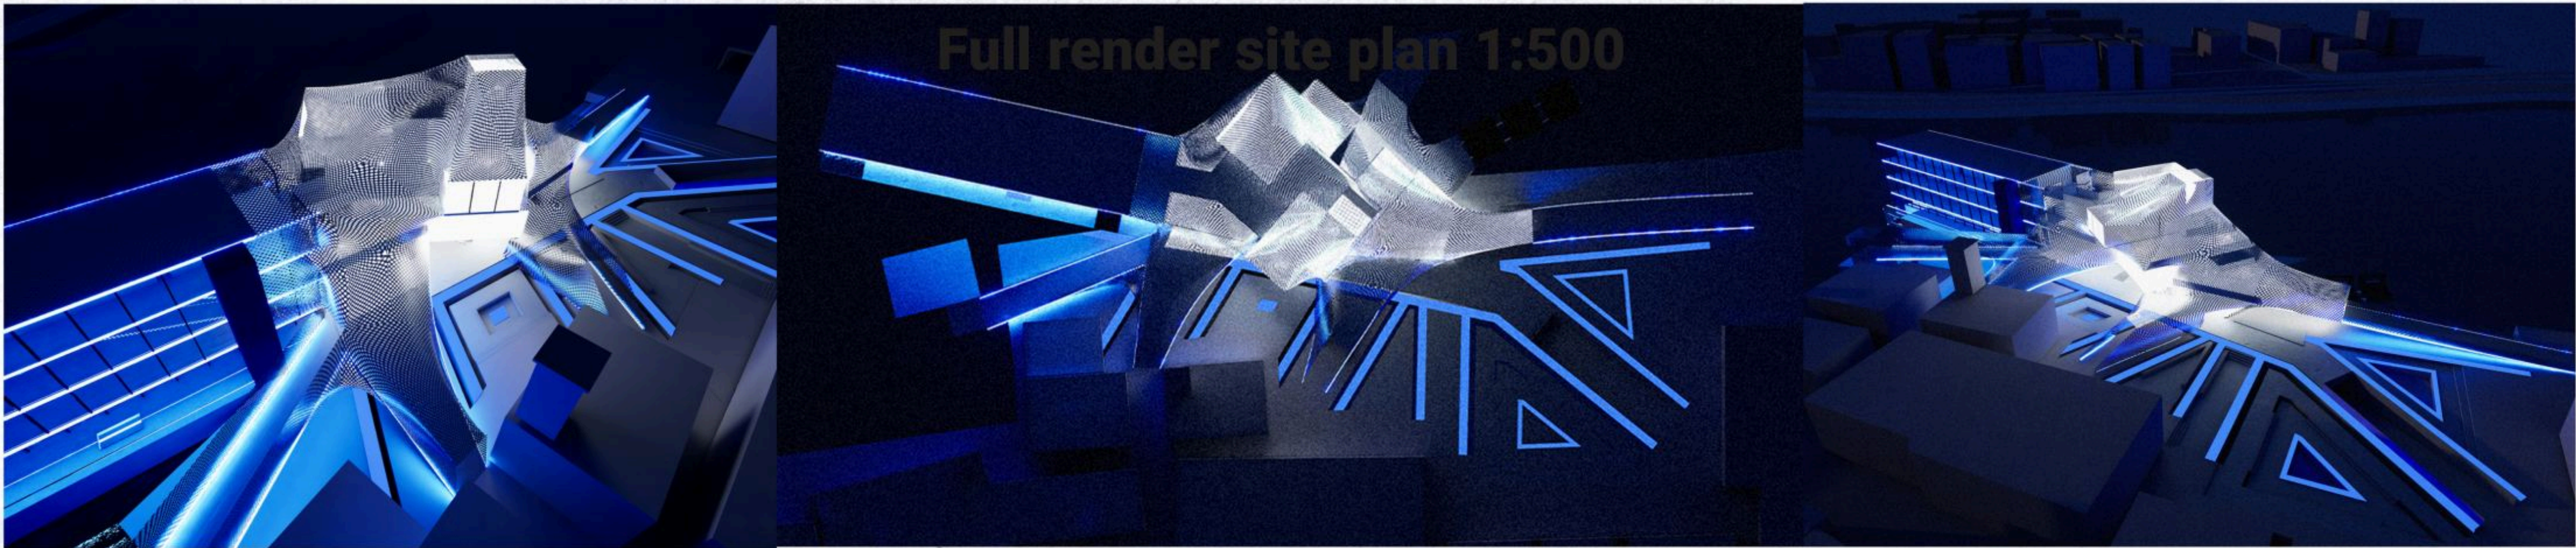

CIRCULATION

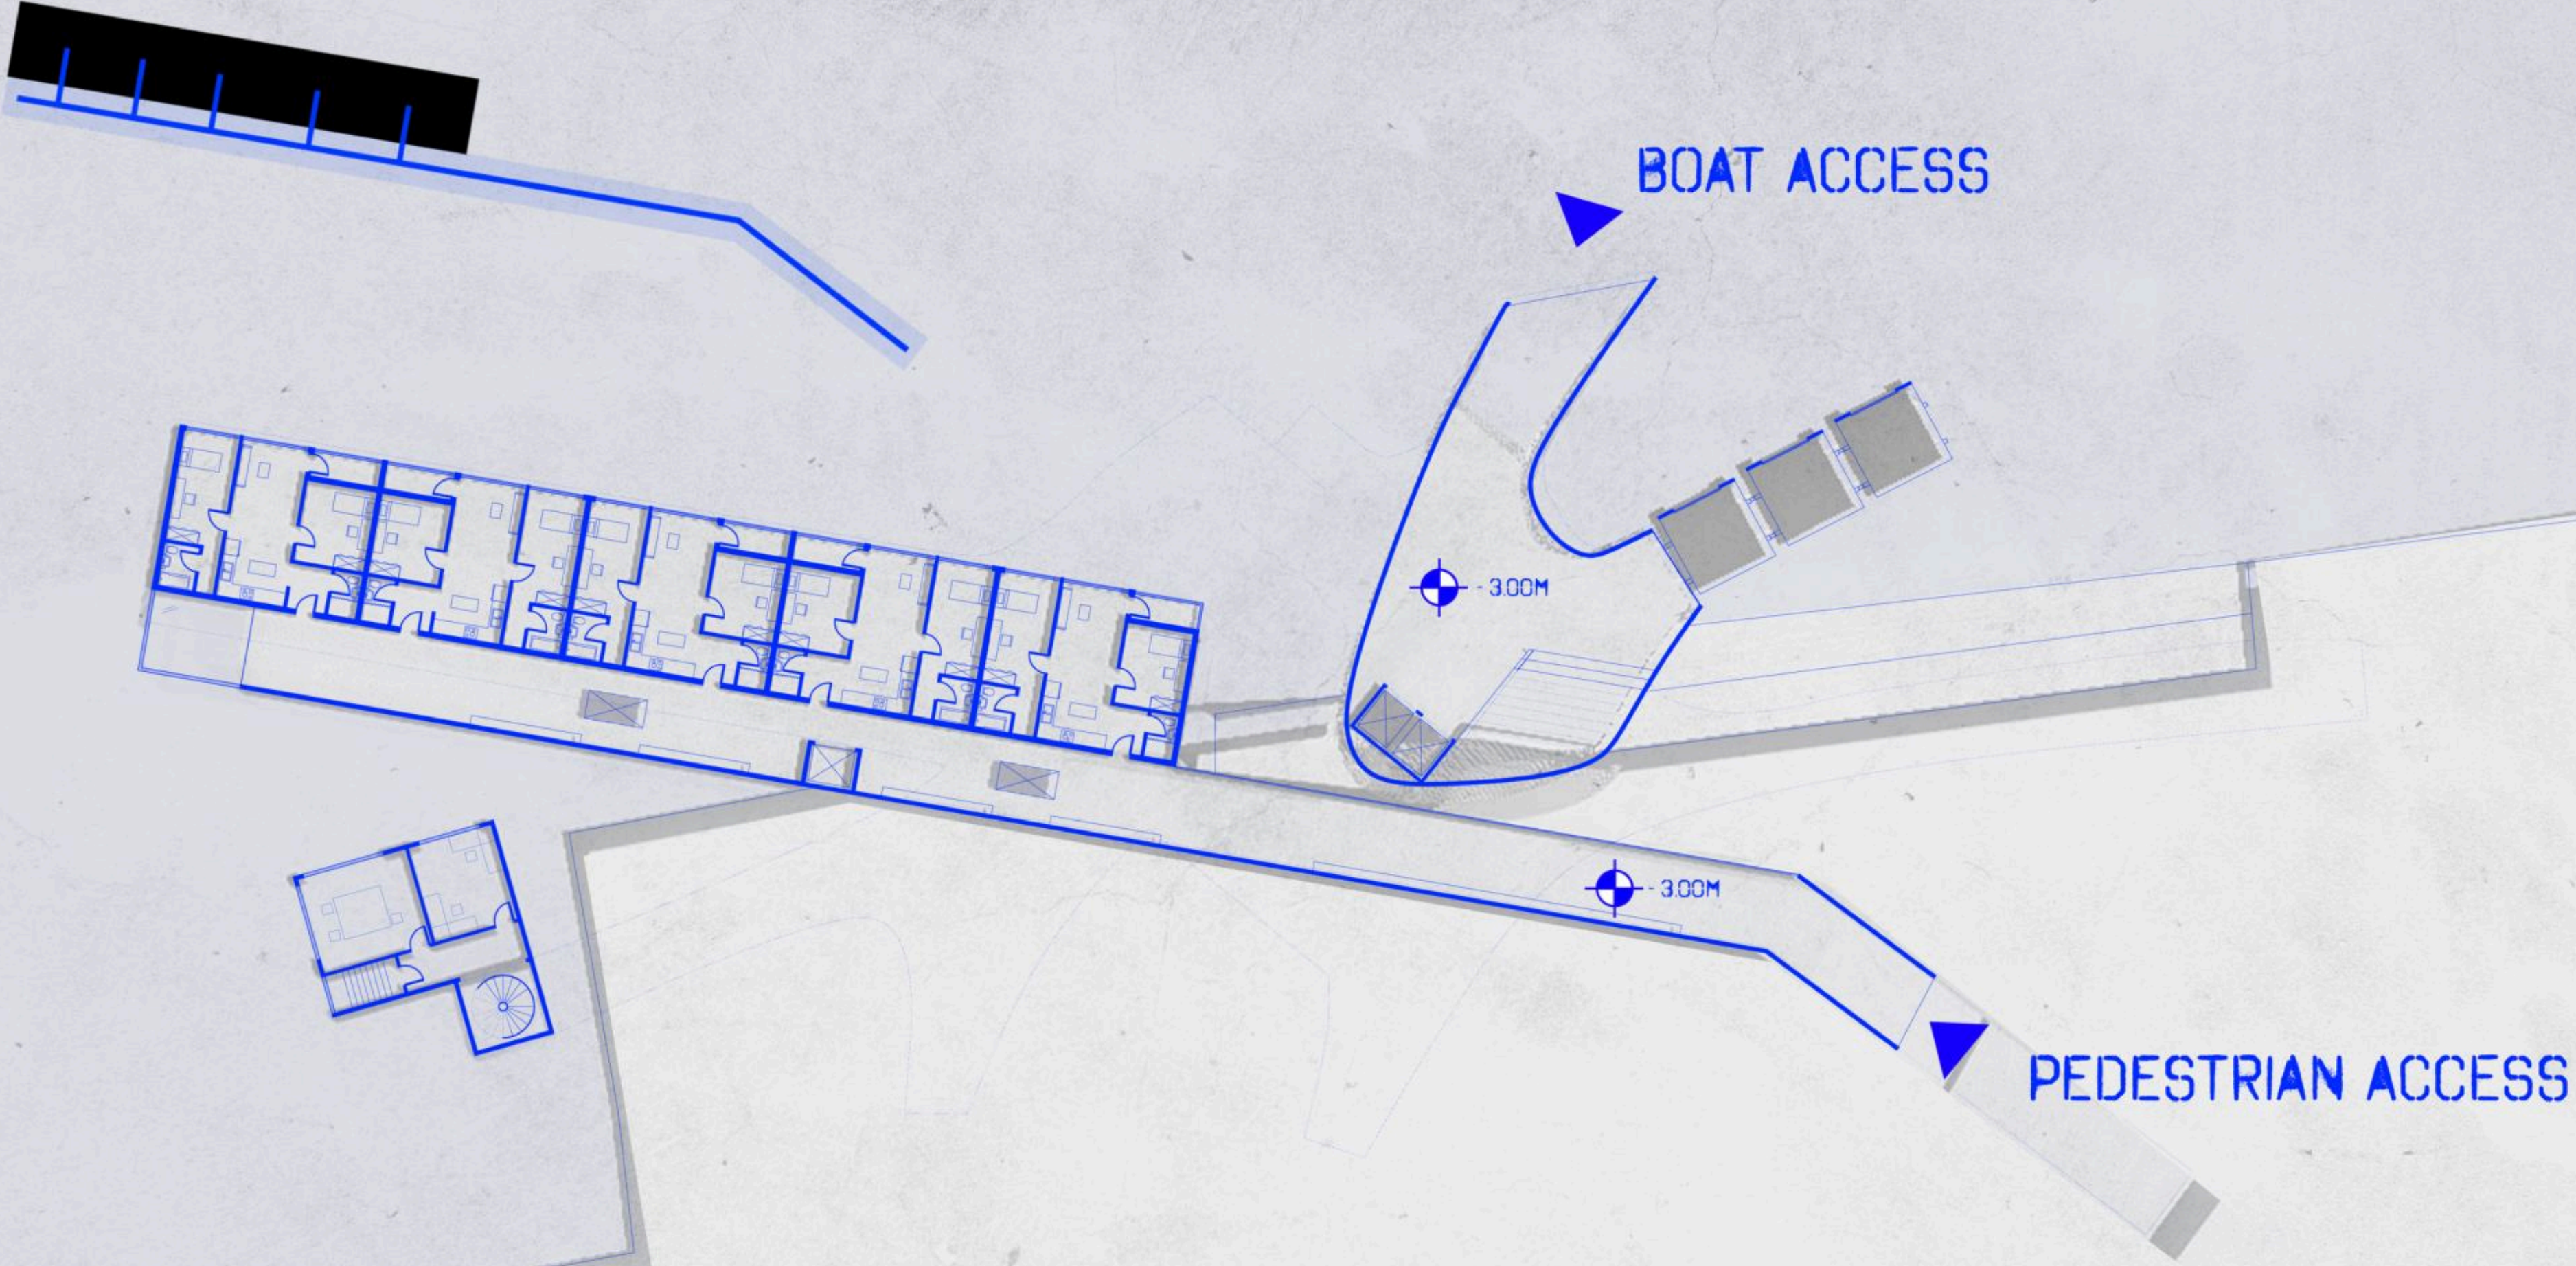

BASEMENT LEVEL FLOOR PLAN
SCALE 1:250



CIRCULATION


BOAT ACCESS

N


GROUND LEVEL FLOOR PLAN

SCALE 1:250

+0.00M

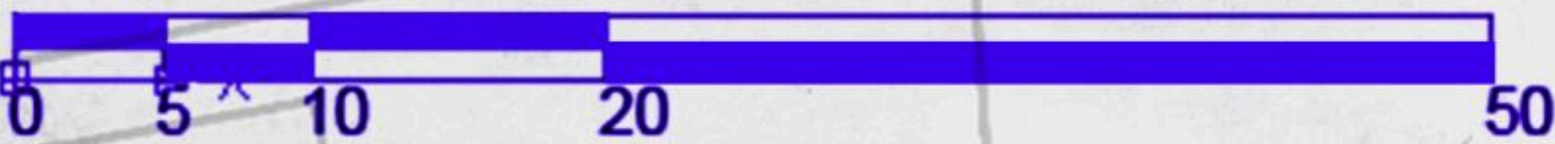


CIRCULATION

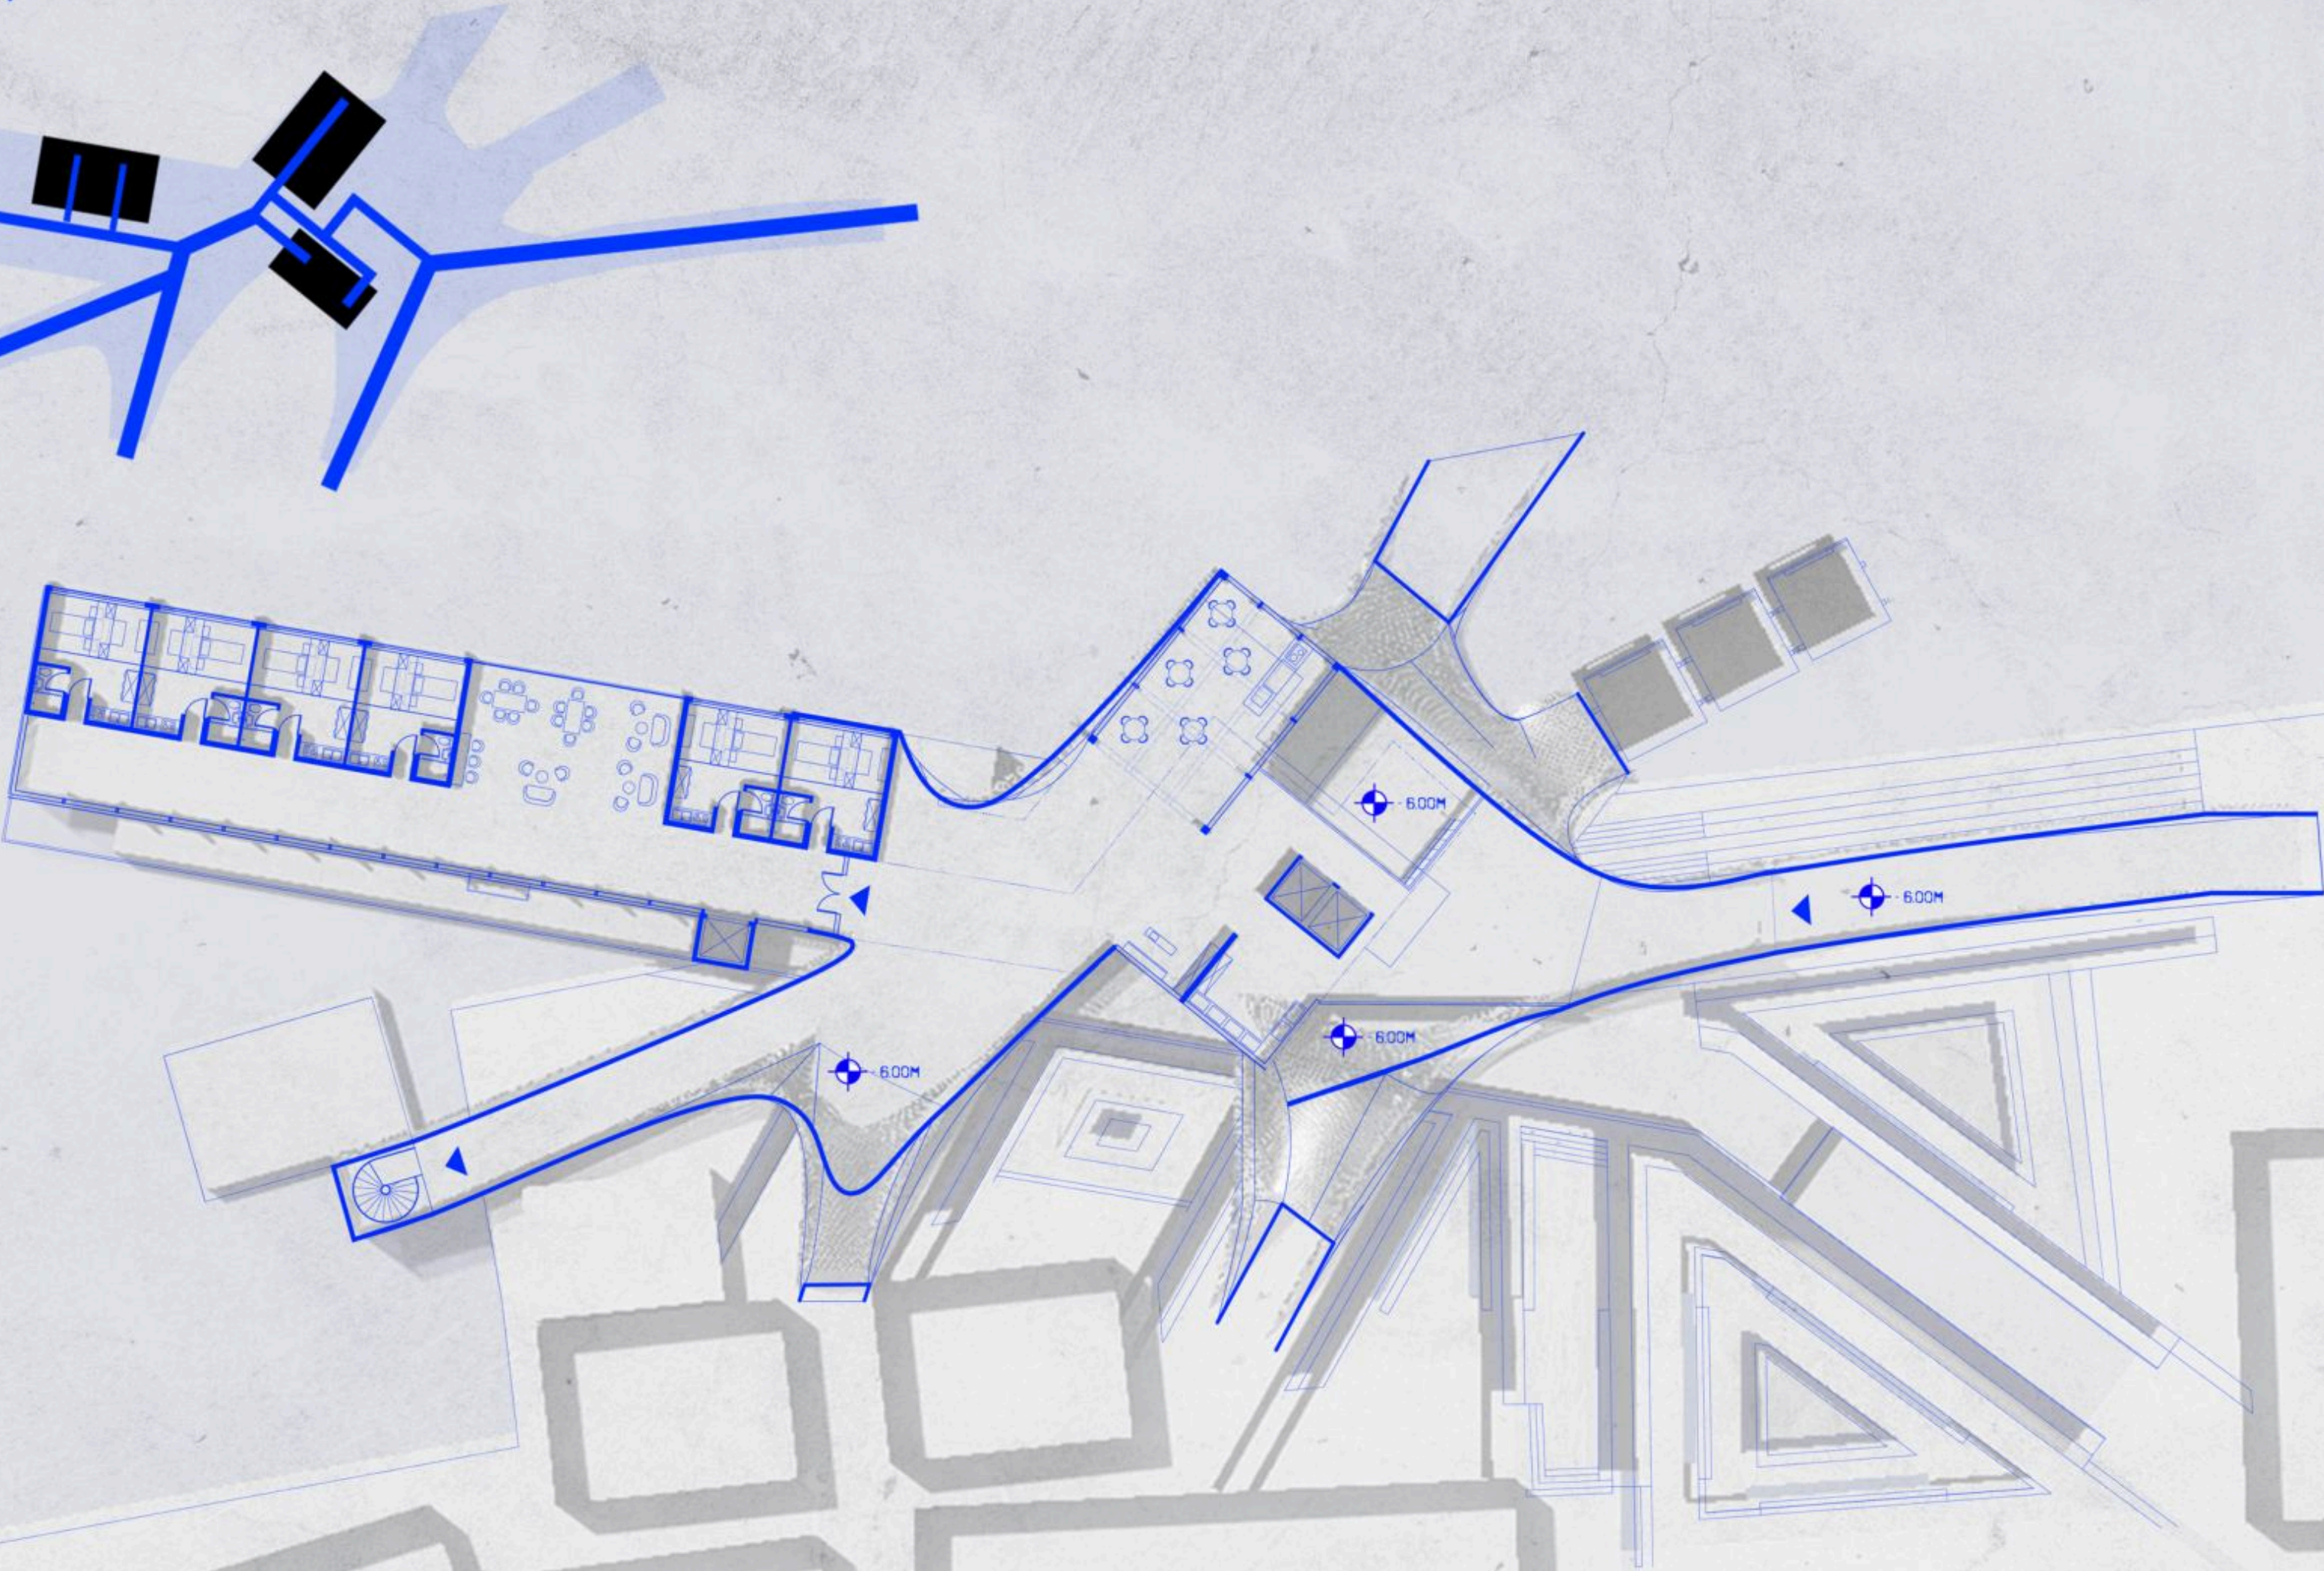

FIRST LEVEL FLOOR PLAN

SCALE 1:250

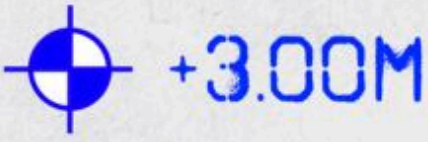


CIRCULATION




SECOND LEVEL FLOOR PLAN

SCALE 1:250

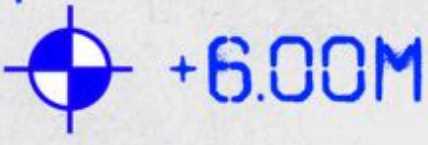



CIRCULATION

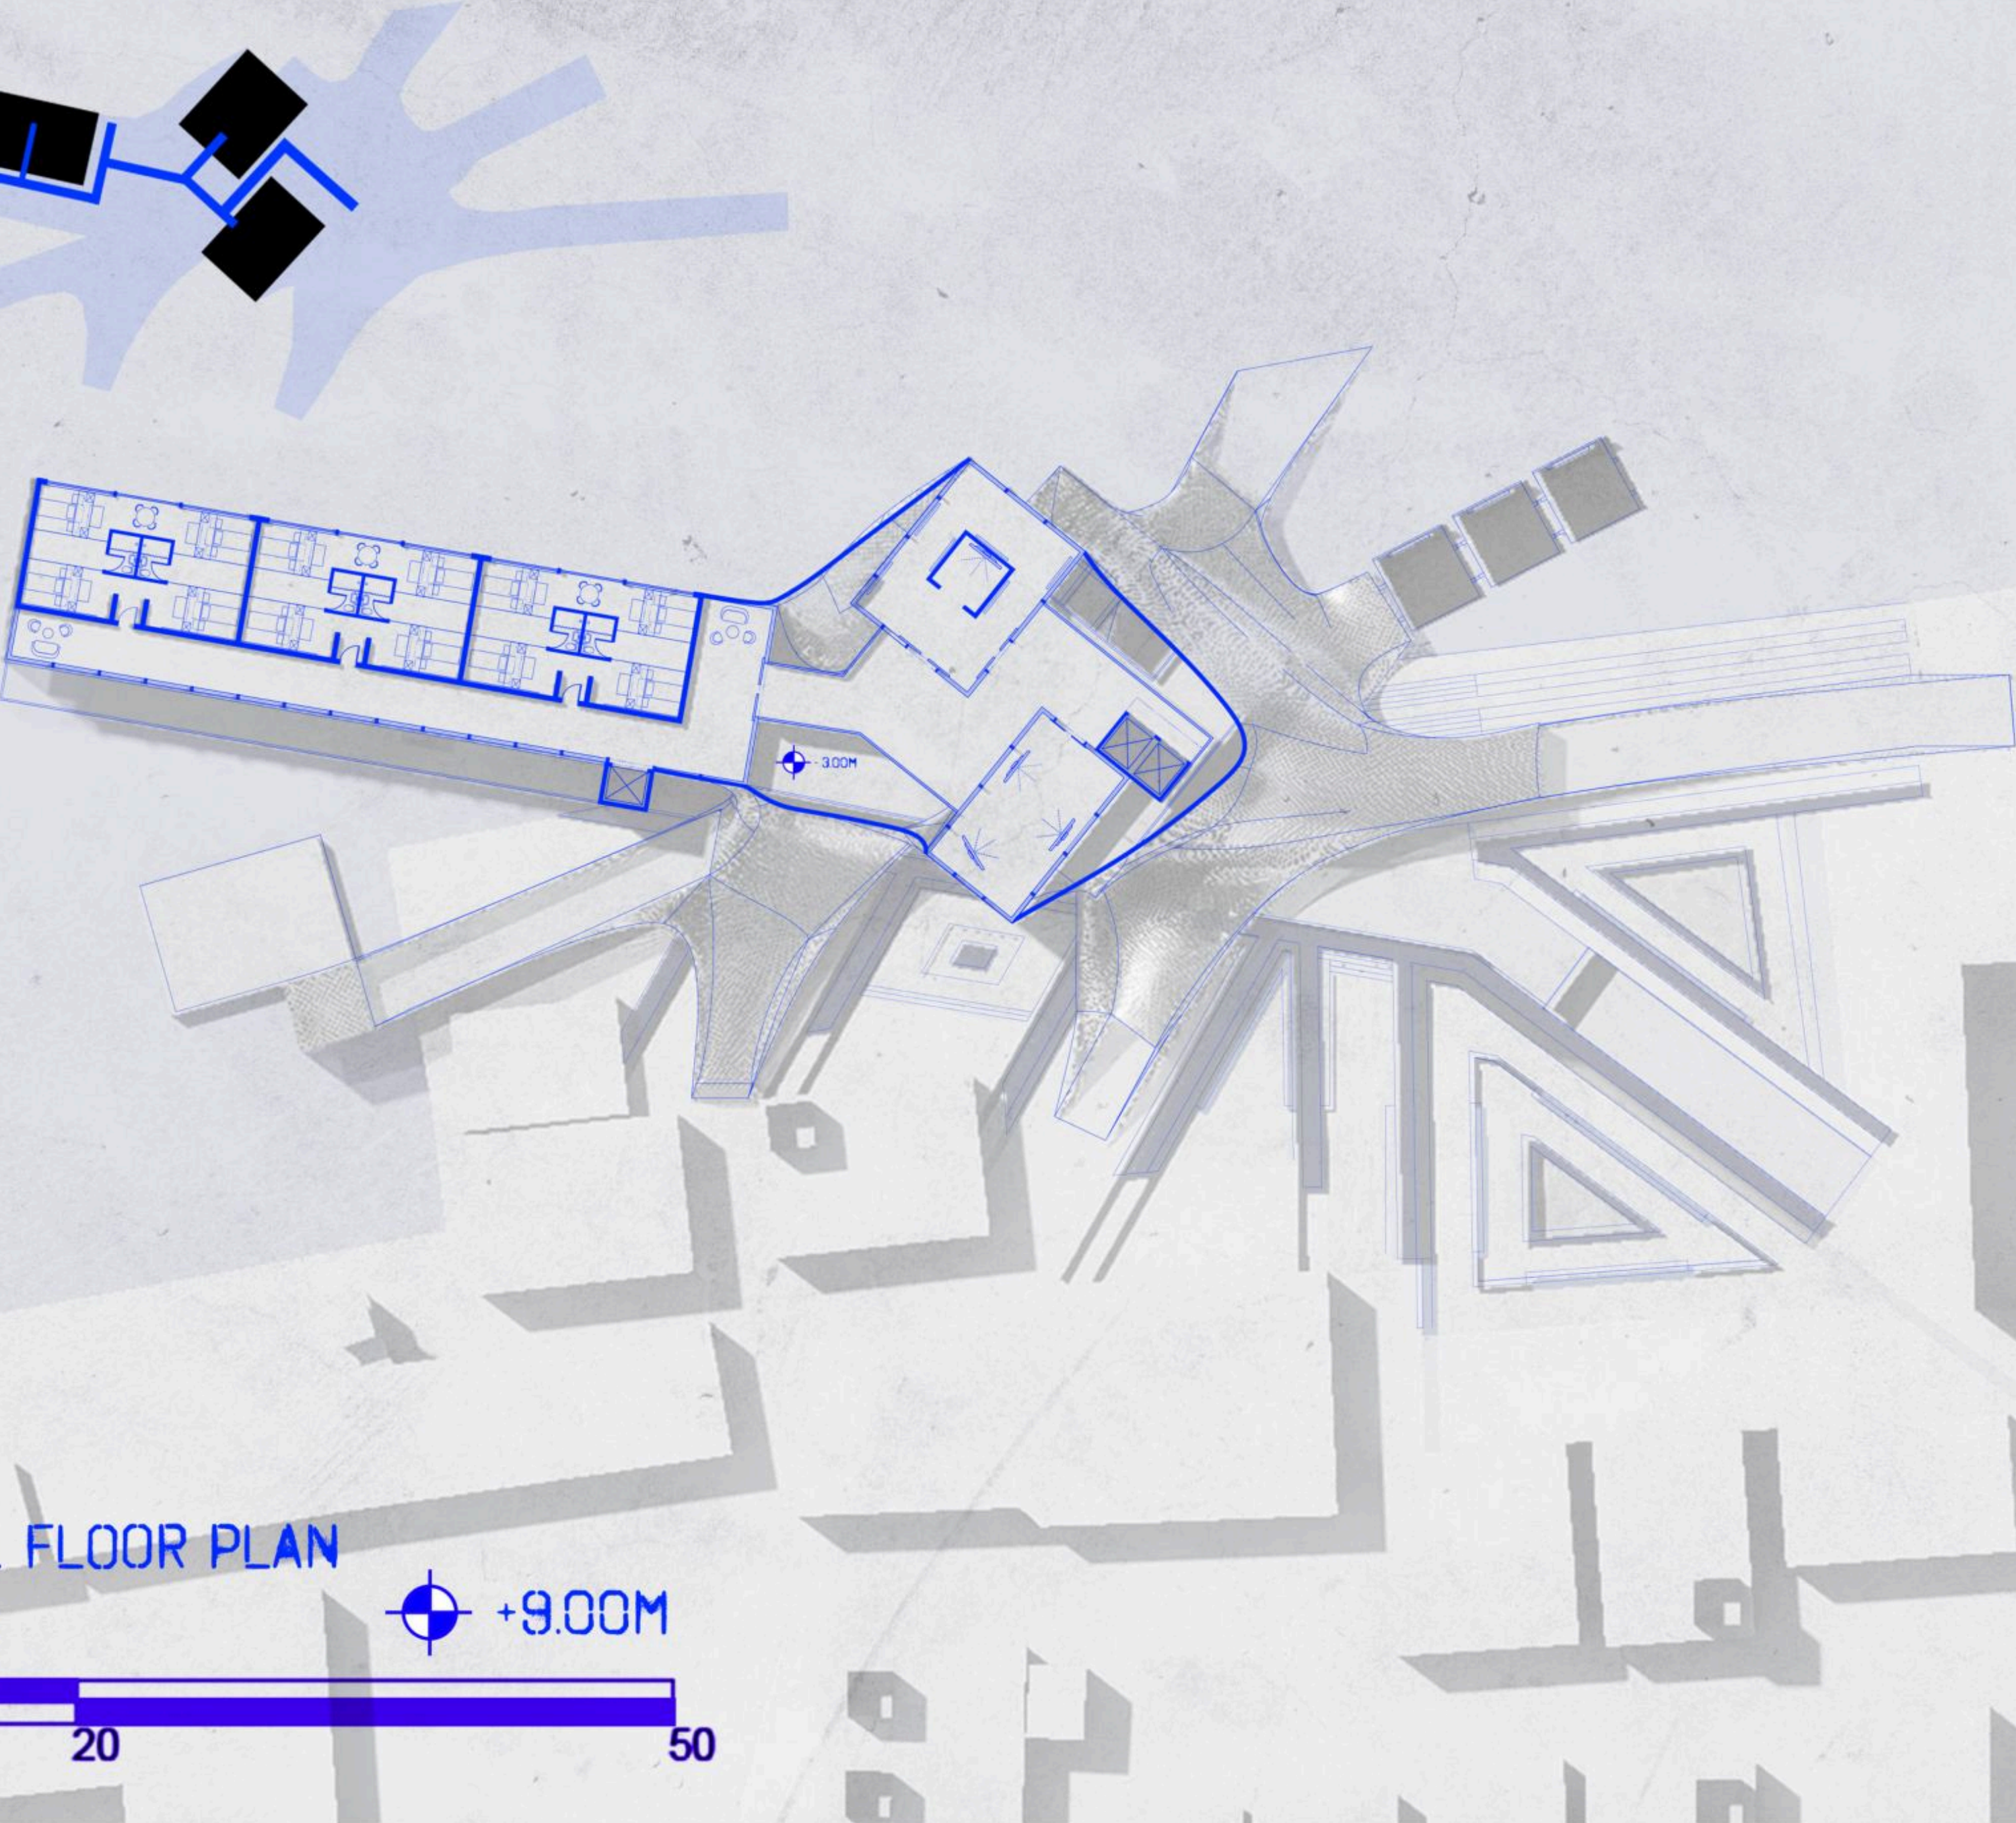

THIRD LEVEL FLOOR PLAN


SCALE 1:250

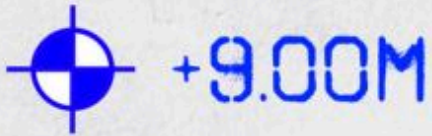

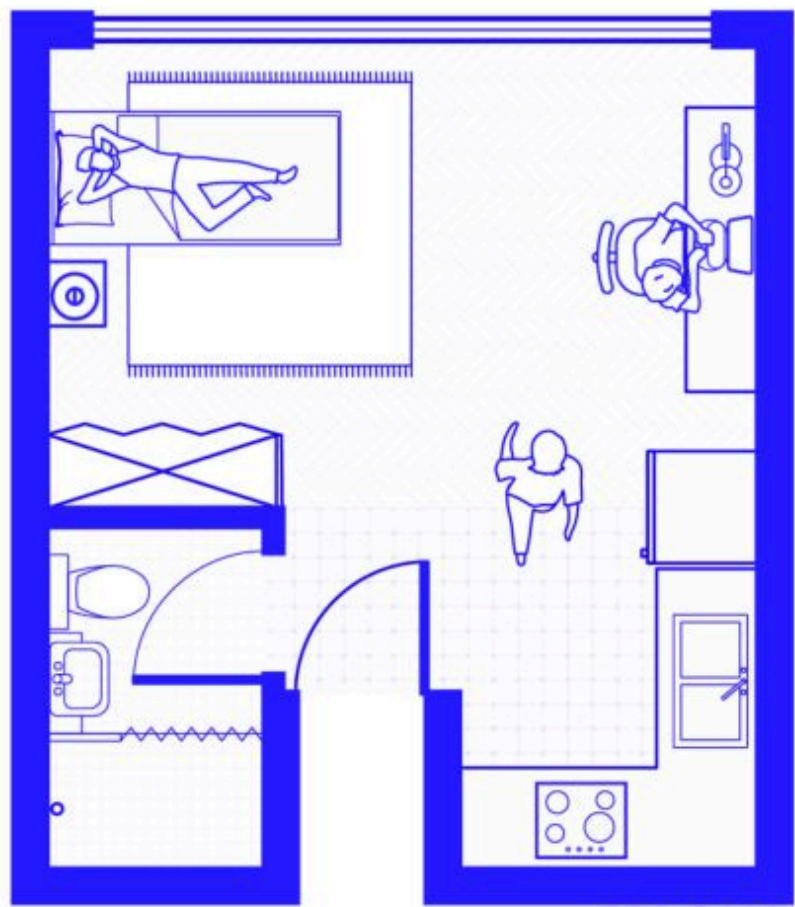

LONG TERM
SINGLE UNIT


SCALE 1:50

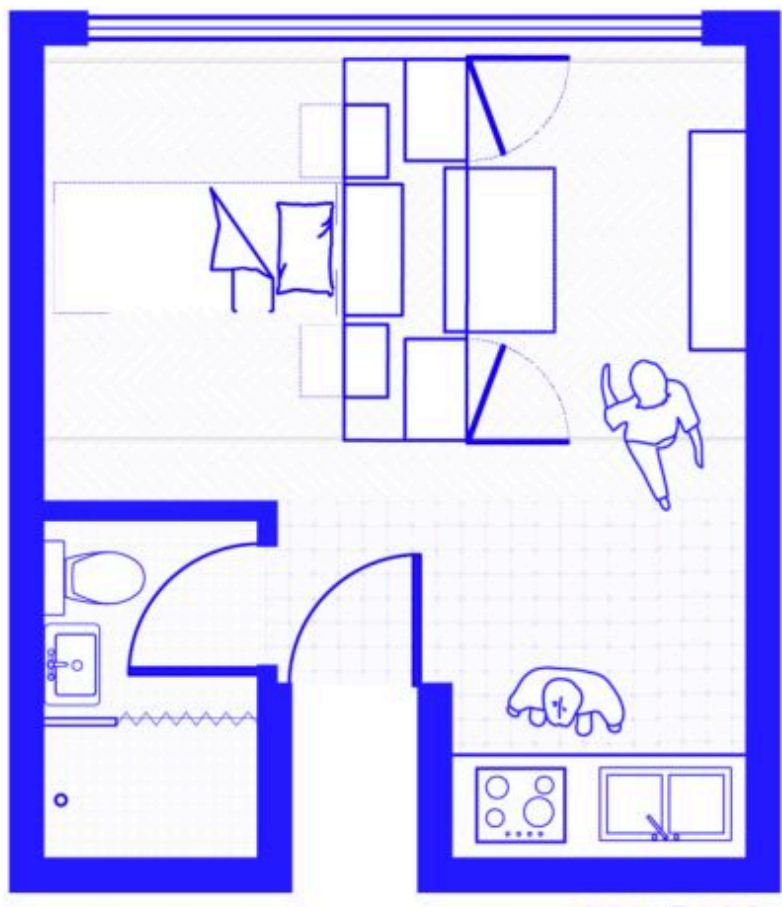

SHORT TERM
SINGLE UNIT


SCALE 1:50

ADAPTIVE UNITS

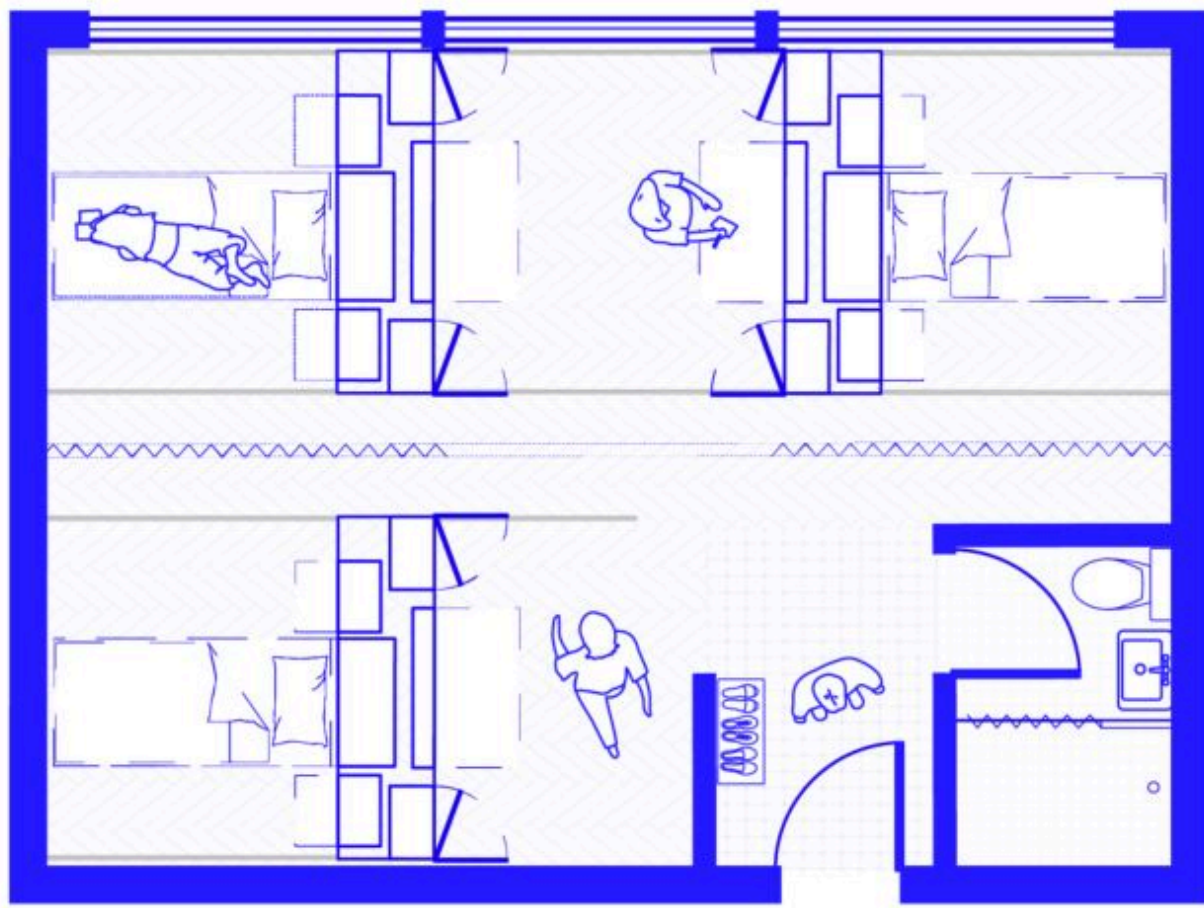


SHORT TERM
3 BED UNIT

SCALE 1:50

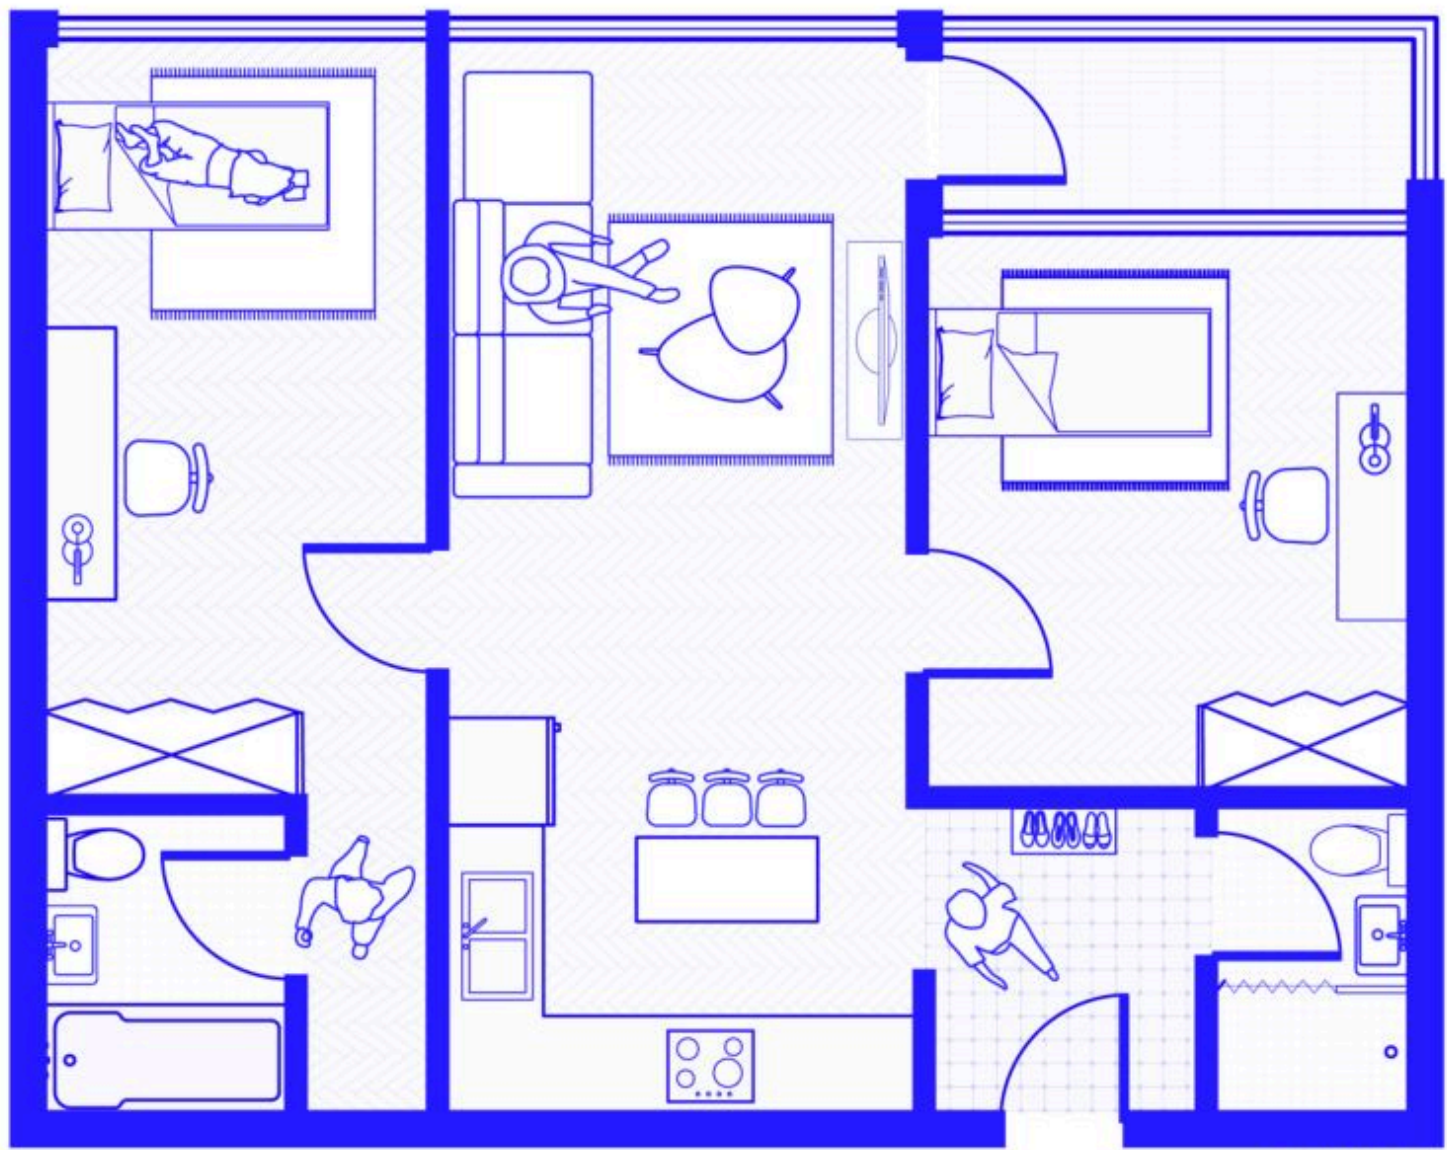


LONG TERM
COUPLE UNIT



SCALE 1:50


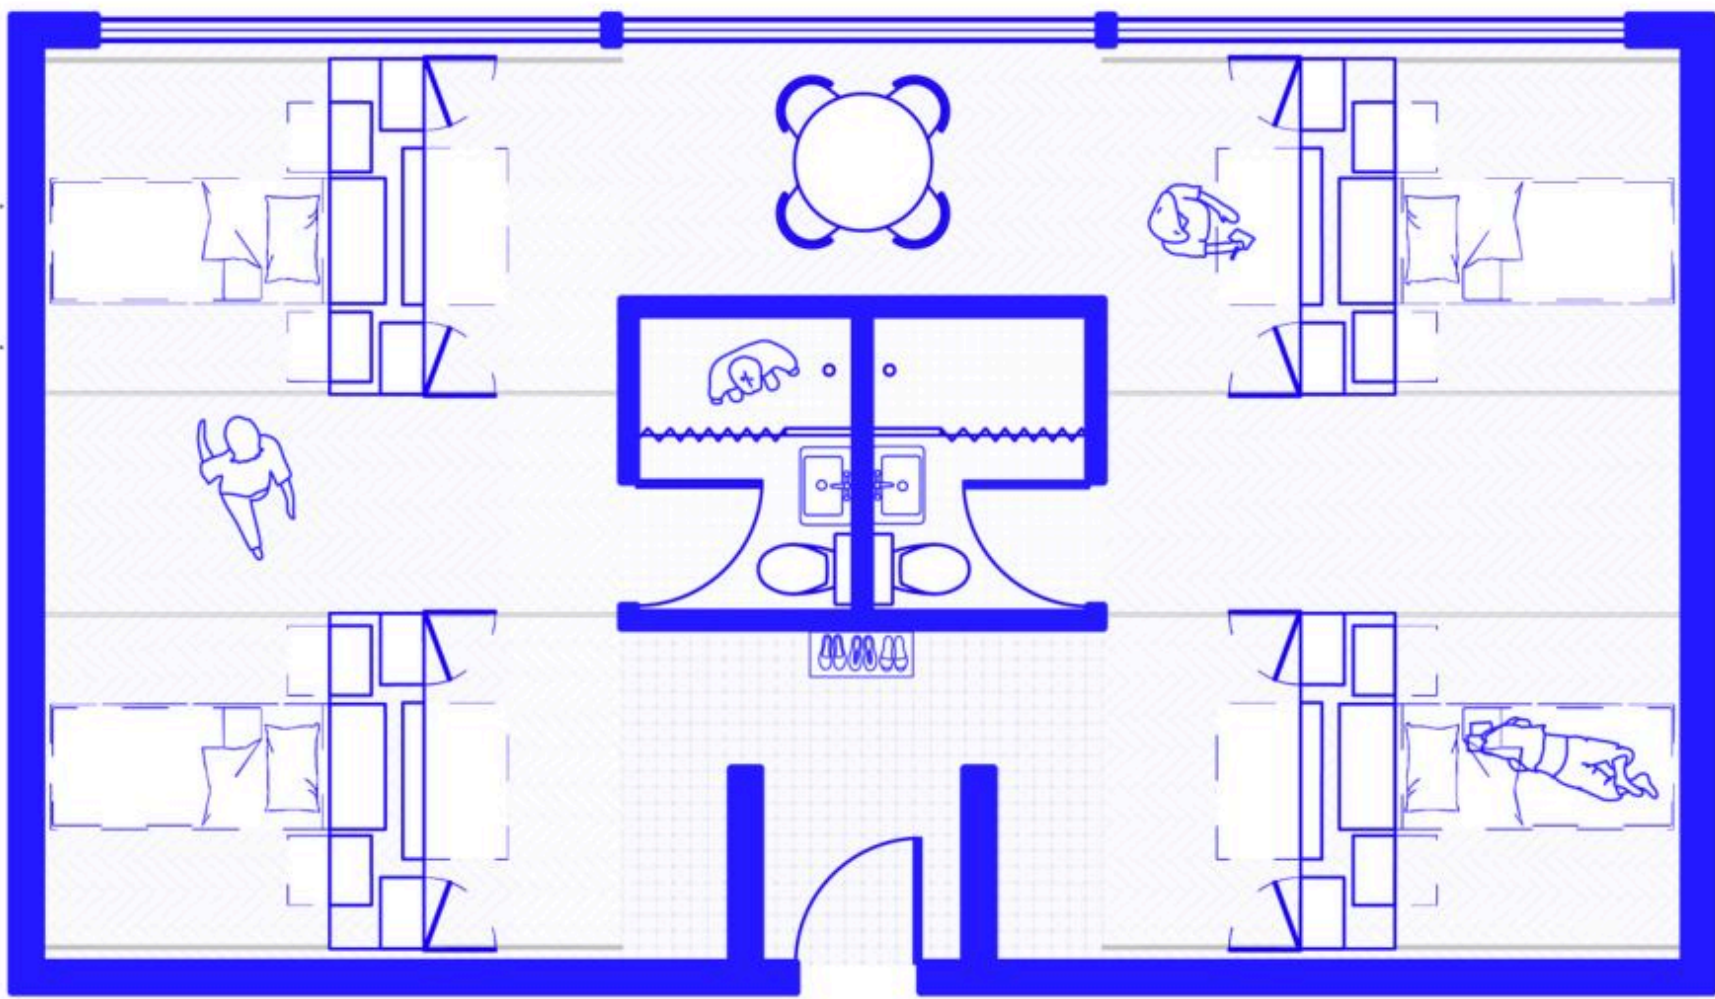


SHORT TERM
GROUP UNIT

SCALE 1:50

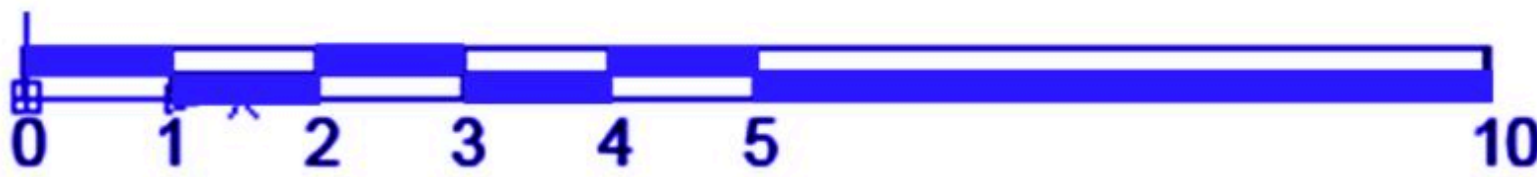

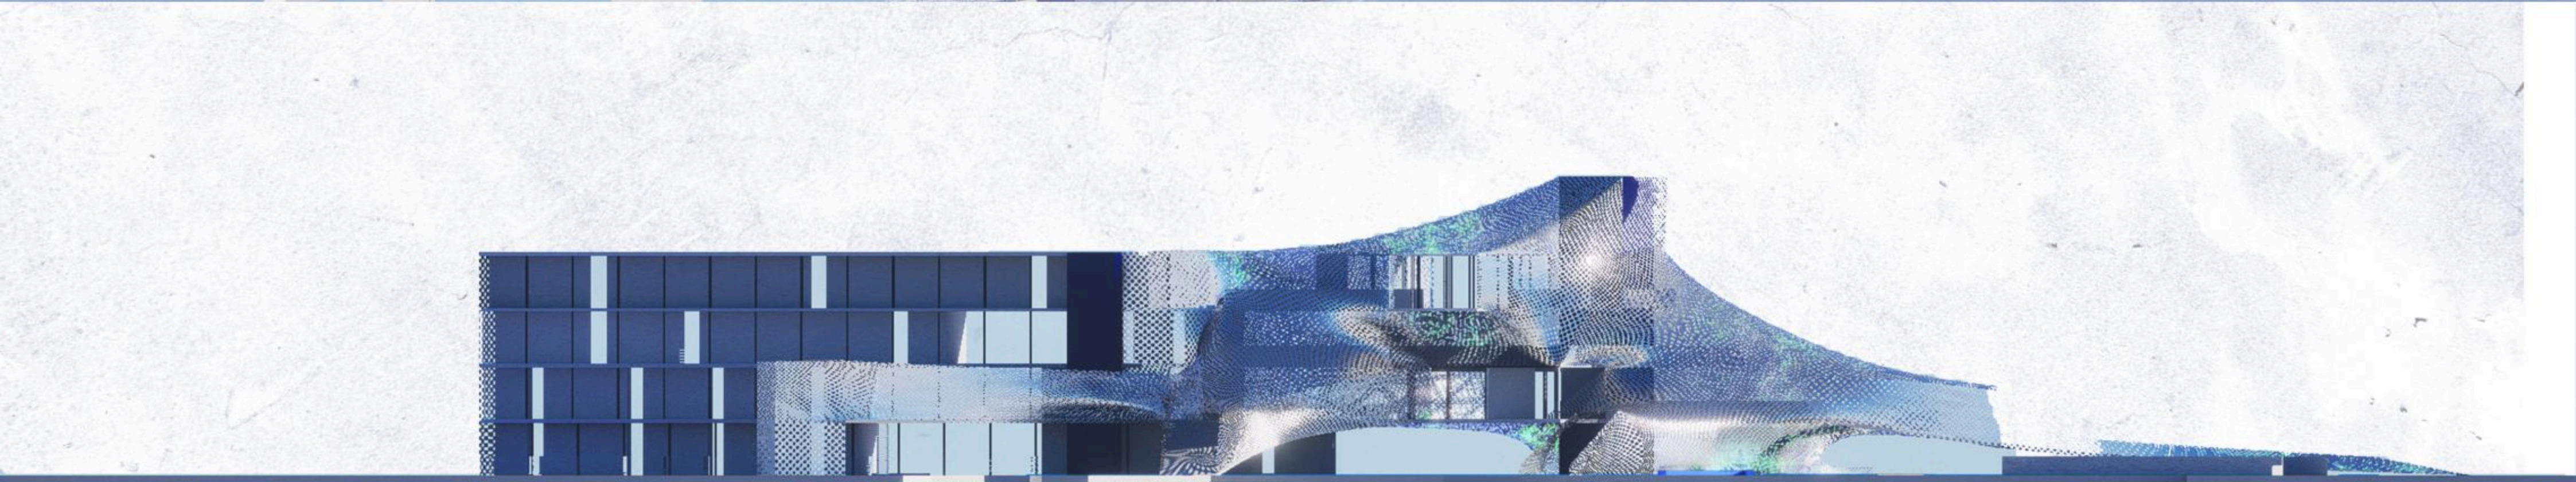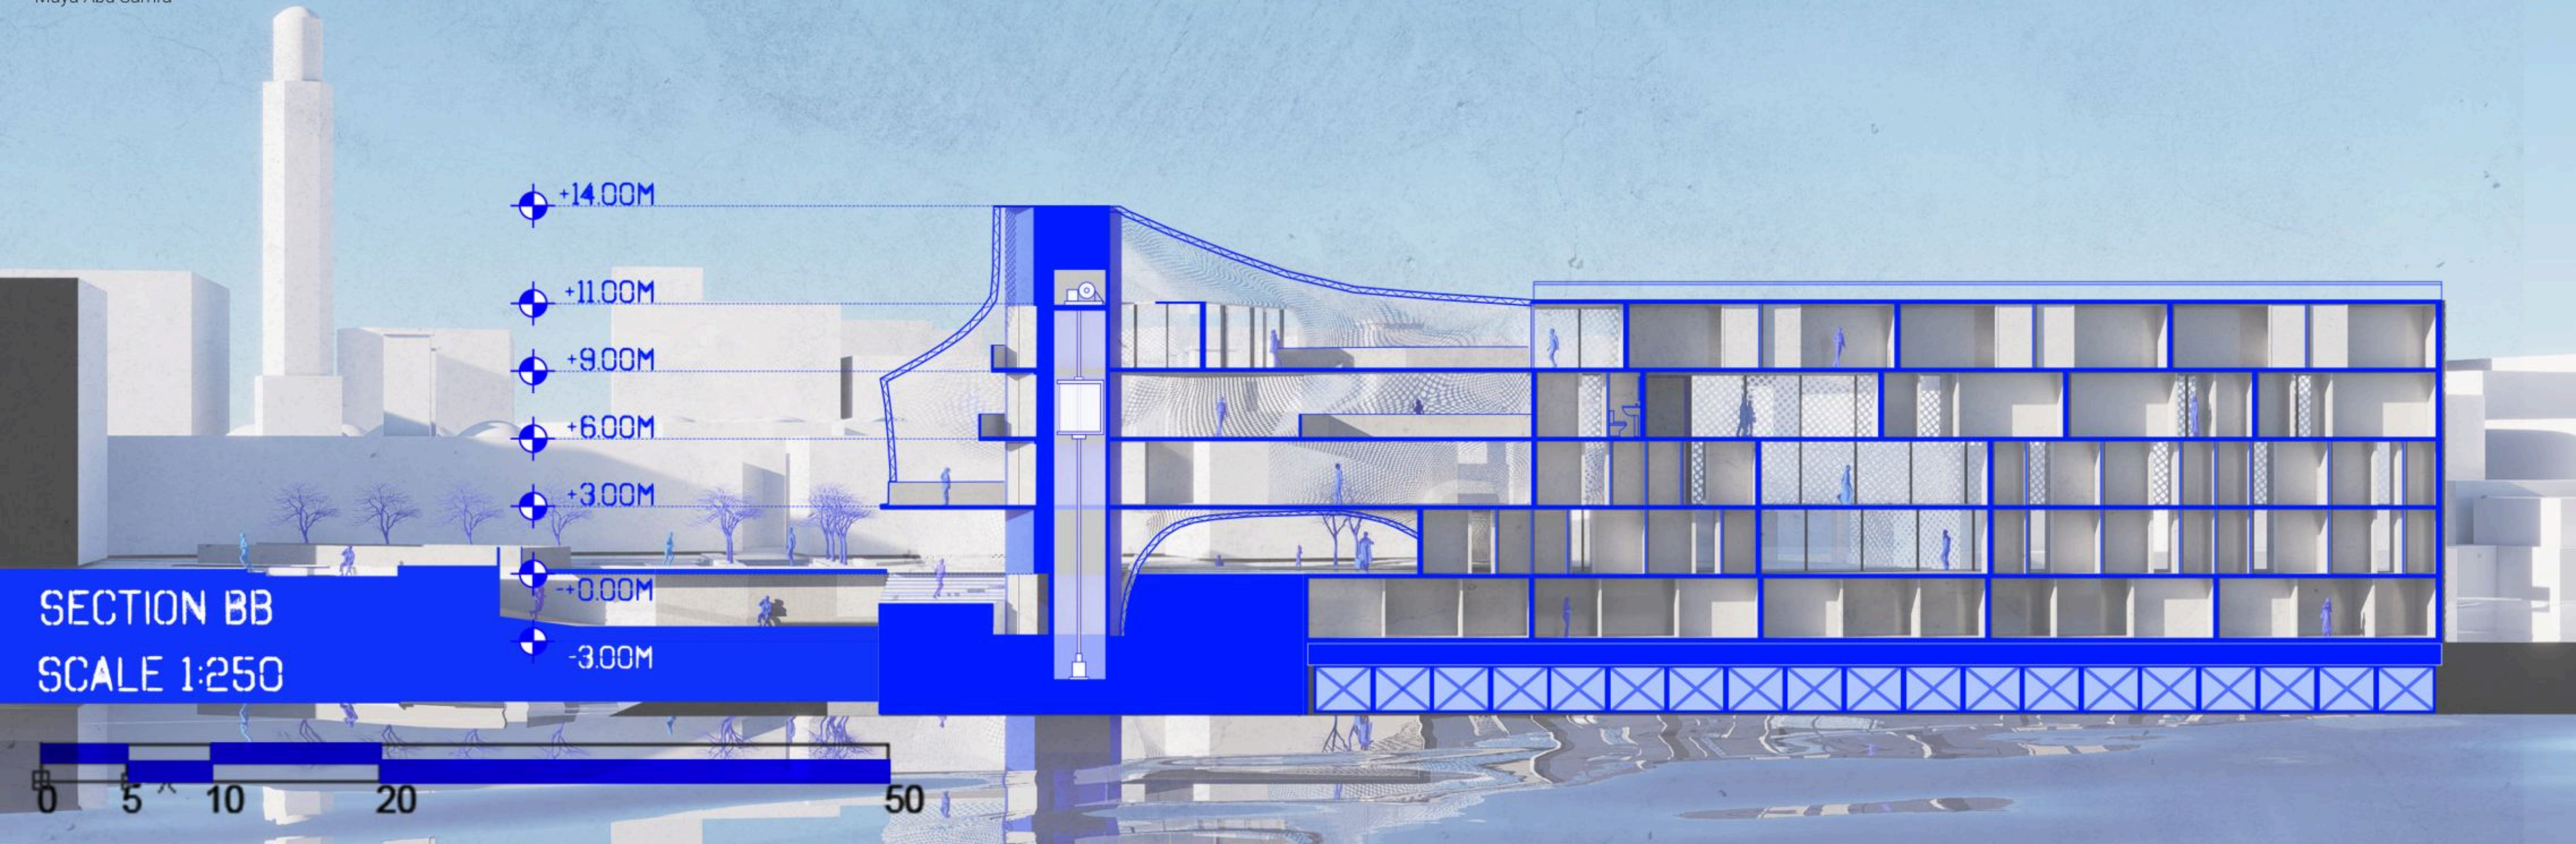

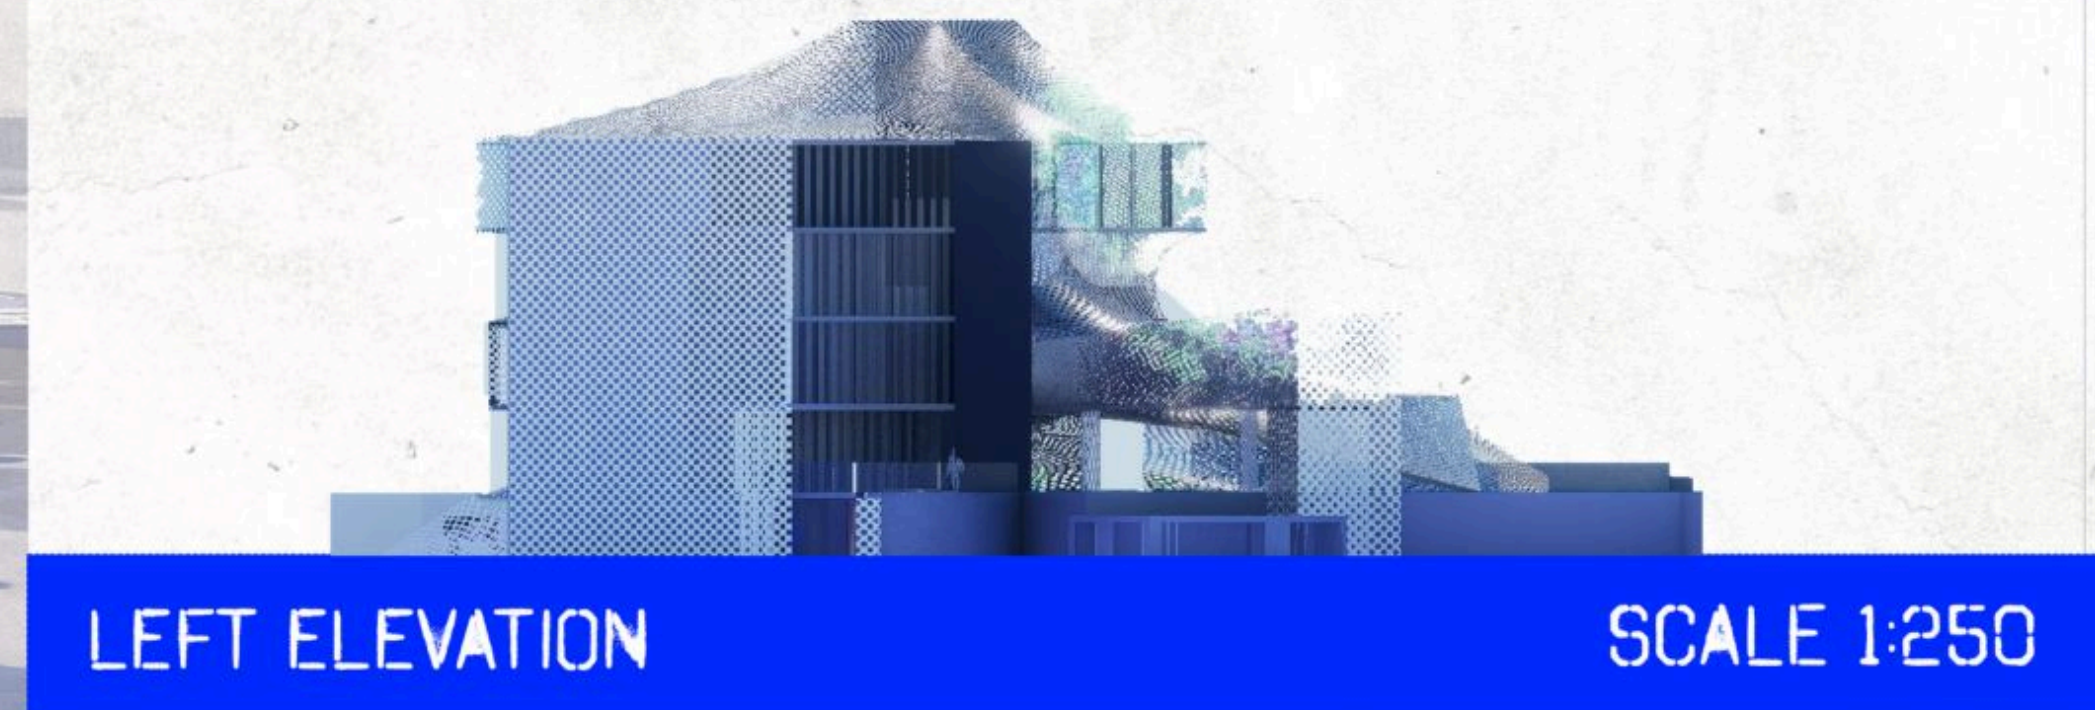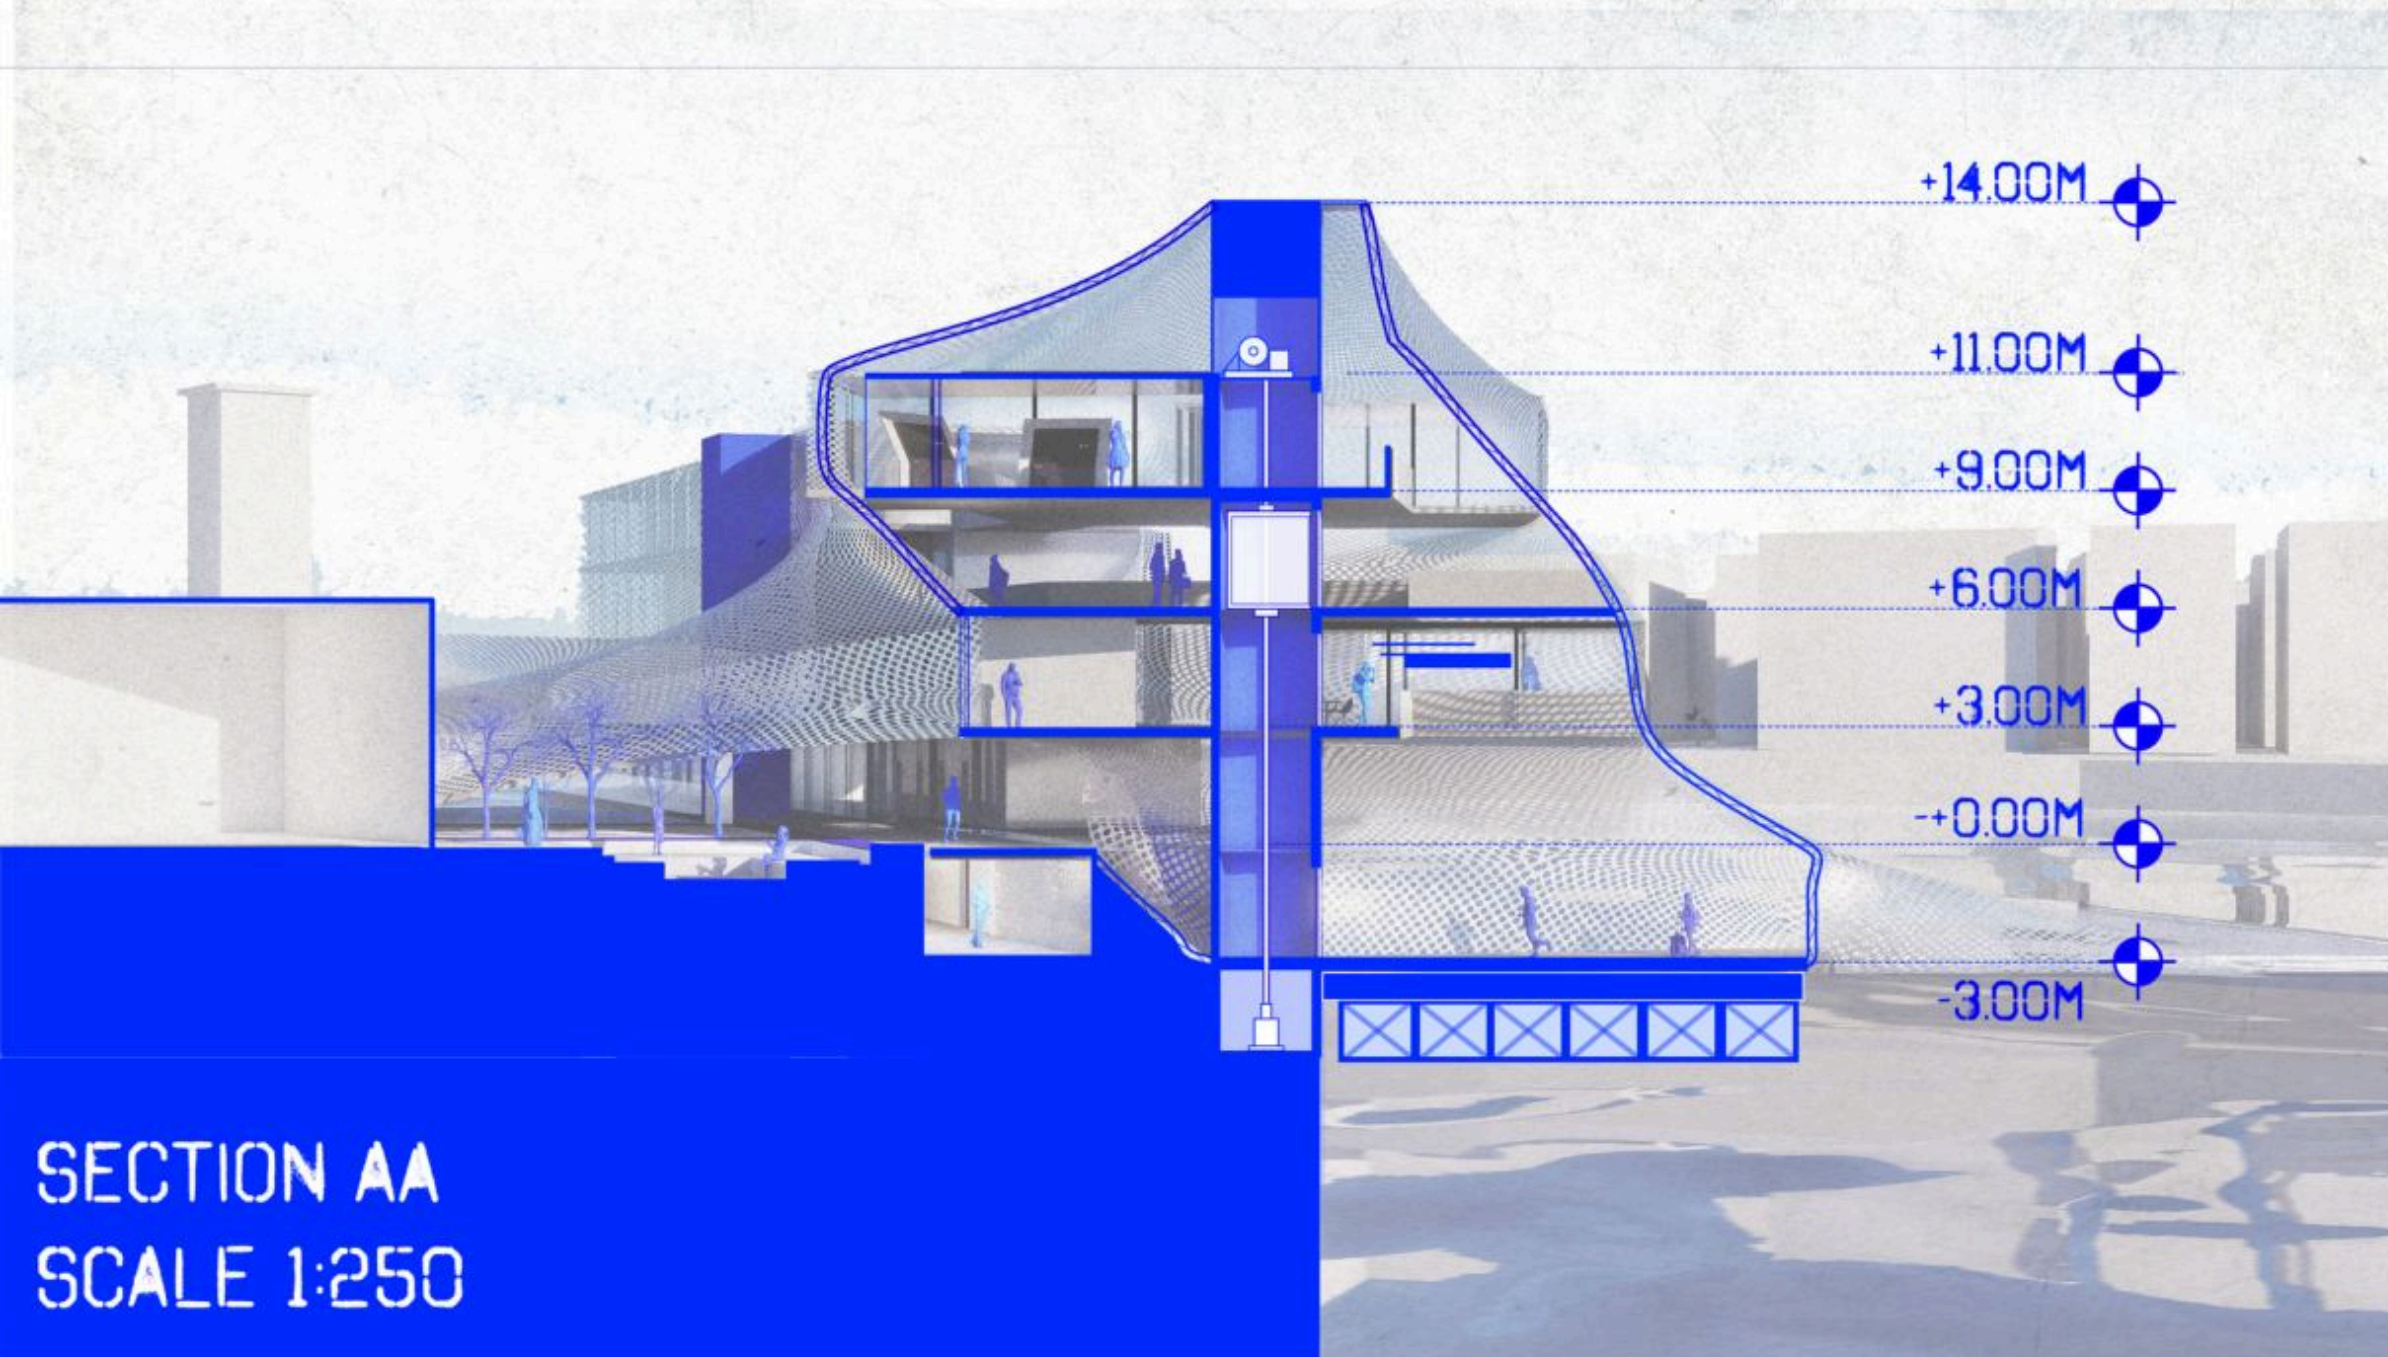

reflections - diagram



THE PLUSE

MOTION AND STILLNESS

MAYA ABU SAMRA

AL FAHIDI ISN'T A PLACE THAT FLOWS IN ONE DIRECTION IT MOVES, STOPS, AND CHANGES RHYTHM. ONE MOMENT YOU'RE WALKING THROUGH A QUIET ALLEY, AND THE NEXT YOU'RE CAUGHT IN A BURST OF SOUND AND COLOUR. SHADE TURNS INTO GLARE, STILL AIR INTO BREEZE. LIFE HERE DOESN'T FOLLOW A PATTERN. IT SHIFTS ABRUPTLY, IN A BEAUTIFUL MANNER THAT CONSTANT TENSION BETWEEN CALM AND CHAOS IS WHAT I WANTED TO CAPTURE.

THE FELT COLLAGE CAME FIRST. IT WAS ABOUT TOUCH, THE FEELING OF THREADS PULLING AGAINST EACH OTHER, SOME STRETCHED TIGHT, OTHERS RELAXED. THE ACT OF WEAVING BECAME A WAY TO UNDERSTAND HOW AL FAHIDI LIVES. EVERYTHING CONNECTED BUT NEVER IDENTICAL. EACH THREAD HELD A RHYTHM, A FRAGMENT OF THE CITY'S PULSE. TOGETHER THEY BECAME A LANDSCAPE OF COEXISTENCE - SOFTNESS MEETING STRUCTURE, STILLNESS MEETING MOVEMENT.

THEN CAME THE LIVED COLLAGE. THE CYAN BLUE SPREAD ACROSS THE SURFACE LIKE THE ECHO OF WATER. EACH FRAGMENT PINNED TOGETHER WITH DIFFERENT SIZED SAFETY PINS. THE PINS BECAME SYMBOLS OF CONNECTION, THE DELICATE TIES BETWEEN PEOPLE, MOMENTS, AND MEMORY. THE RIPPLES REFLECT THE CONVERSATIONS OVERLAPPING, STORIES WASHING INTO EACH OTHER LIKE TIDES. THROUGH THE BLUE, I SAW THE CALM OF THE CREEK, THE IMPRINT OF HEAT, THE RHYTHM OF FOOTSTEPS.

ACROSS THE SITE, I KEPT FEELING THREE EMOTIONS REPEATING THEMSELVES: **DISORIENTATION, REJUVENATION, AND AMBIVALENT BELONGING.**

DISORIENTATION IS PART OF THE EXPERIENCE. THE CONFUSION OF NARROW TURNS, THE SENSORY OVERLOAD OF SOUND AND MOVEMENT. REJUVENATION APPEARS IN SMALL PAUSES, THE COURTYARDS, THE SHADE. THE WATER AND AMBIVALENT BELONGING SITS QUIETLY BETWEEN THEM. WHERE LOCALS AND TOURISTS SHARE THE SAME SPACES IN DIFFERENT WAYS, BOTH INSIDE AND OUTSIDE AT ONCE.

THESE EMOTIONS BECAME MY LENS. I DIDN'T WANT TO ERASE THE CONTRADICTIONS IN THE SITE. I WANTED TO WORK WITH THEM. AL FAHIDI'S RHYTHM LIES IN ITS DISSONANCE — IN HOW PEOPLE ADAPT TO THE SUDDEN CHANGES. THE MOVEMENT THROUGH IT FEELS LIKE A KIND OF MUSIC, NOT SMOOTH BUT LAYERED. EVERY PAUSE, EVERY CLASH, ADDS TO THE COMPOSITION.

"THE PULSE" BECAME A WAY OF THINKING ABOUT THE CITY AS A LIVING SCORE. THE STREETS ACT AS NOTES, THE COURTYARDS AS RESTS, AND THE WATER AS A QUIET, CONTINUOUS SOUND IN THE BACKGROUND. THE RHYTHM OF AL FAHIDI TEACHES YOU TO SLOW DOWN AND TO LISTEN.

THIS PROJECT IS ABOUT THE COEXISTENCE OF MOTION AND STILLNESS. IT ASKS HOW DESIGN CAN RESPECT WHAT ALREADY EXISTS — THE RHYTHM, THE IMBALANCE, THE DIALOGUE BETWEEN THE TWO. IT'S NOT ABOUT FIXING OR PERFECTING THE SITE, BUT ABOUT LEARNING FROM ITS CONTRADICTIONS. THE PULSE OF AL FAHIDI DOESN'T COME FROM ORDER. IT COMES FROM EVERYTHING THAT REFUSES TO ALIGN, YET SOMEHOW STILL BELONGS.

SITE VIDEO QR CODE



FLOOR PLAN ARRANGEMENT AND INTERNAL

Key Plan

- LIVING
- BEDROOM
- OUTDOOR
- LOUNGE

3 BEDROOM LIVING UNIT

2 BEDROOM LIVING UNIT

1 BEDROOM LIVING UNIT

SHARED SPACES

This individual unit is spatially split by the living space in the middle. The master bedroom is on the left, whilst the two 1 beds are on the right. The living space in the middle allows for public entry, instead of direct entry to the private zones. The outdoor terraces are accessible from the living area and the master. The entry to the living unit welcomes the user with an outdoor terrace with seating, which is reflected on the other side of the living unit. Through the sections I can see a clear division between the public and private, where the living/ public splits the private.

This housing project divides 3 bedroom units, 2 bedroom units and 1 bedroom units. The three bedroom units are the edge of the building, possibly for better views to be spread across the bedrooms and terrace. There are shared spaces such as lounge areas, a shared kitchen and workspaces in between the units. This teaches me that its crucial to have shared spaces within proximity to all units to encourage community building at all corners.

CIRCULATION & FLOATING MECHANISM

Water Pavilion for the Yeosu EXPO 2012

SHIFT IN EXPERIENCE AND FUNCTION

IDEAS FOR MY PROJECT

CIRCULATION GUIDE TO UNDERWATER

BOUNDARY

CHOOSING PATH

SPATIAL EXPERIENCE

FLUID CIRCULATION

Circulation starts on land and gradually moves to the water place that allows for the underwater exhibition hall.

Paths split and recombine like currents, with triangular islands of water allowing visual and physical connections between above and below levels.

Visitors can choose different routes, emphasizing freedom of movement and self-directed experience - Freedom of choice.

Experience shifts as position changes and water level rises. Water level is fixed in water tank. The still known surroundings are floating on water, which is my concept of freedom of choice.

LOBSTER EXOSKELETON - LAYERED CHITIN FIBERS + PROTEIN MATRIX

Exocuticle (hard) unidirectional fibres + for directional load.

Endocuticle (soft) helicoidal fibre pattern + isotropic strength.

STRUCTURE

SOFT VS. HARD GLASS FIBER & CARBON FIBER

SYNTAX DEVELOPMENT

FABRICATION

DOUBLE LAYERED CONSTRUCTION

36 UNITS

MODULAR ASSEMBLY

WIRE FRAME

FIBER OUTERSHELL

UNIDIRECTIONAL FIBERS

HELICOIDAL FIBERS

SOFT & HARD → SPATIAL EXPERIENCE

ICD/ITKE RESEARCH PAVILLION

FIBER REINFORCED COMPOSITE SHELL EXTRA LOADING FACADE SYSTEM INSULATION coreless robotic winding → no molds or waste.

LOBSTER EXOSKELETON MATERIAL EFFICIENCY AND LOCAL ADAPTATION

SOFT VS. HARD GLASS FIBER & CARBON FIBER

SYNTAX DEVELOPMENT

FABRICATION

DOUBLE LAYERED CONSTRUCTION

36 UNITS

MODULAR ASSEMBLY

WIRE FRAME

FIBER OUTERSHELL

UNIDIRECTIONAL FIBERS

HELICOIDAL FIBERS

SOFT & HARD → SPATIAL EXPERIENCE

RHYTHMIC DISSONANCE


NEGOTIATING CHAOS AND
STILLNESS WITHIN
THE CITY

AL FAHIDI




ONCE THE CITY'S LIFE LINE, THE CREEK SHAPED DUBAI'S EARLIEST SETTLEMENTS, TRADE, AND CULTURE. OVER TIME, ITS EDGE TRANSFORMED FROM SAND AND SALT TO CONCRETE AND SKYLINE. YET ITS ESSENCE REMAINS: THE CREEK REMAINS A THRESHOLD BETWEEN PAST AND PRESENT, STILL CARRYING THE RHYTHM OF EXCHANGE, MOVEMENT, AND BELONGING THAT BUILT THE CITY.




MAPPING AL FAHIDI

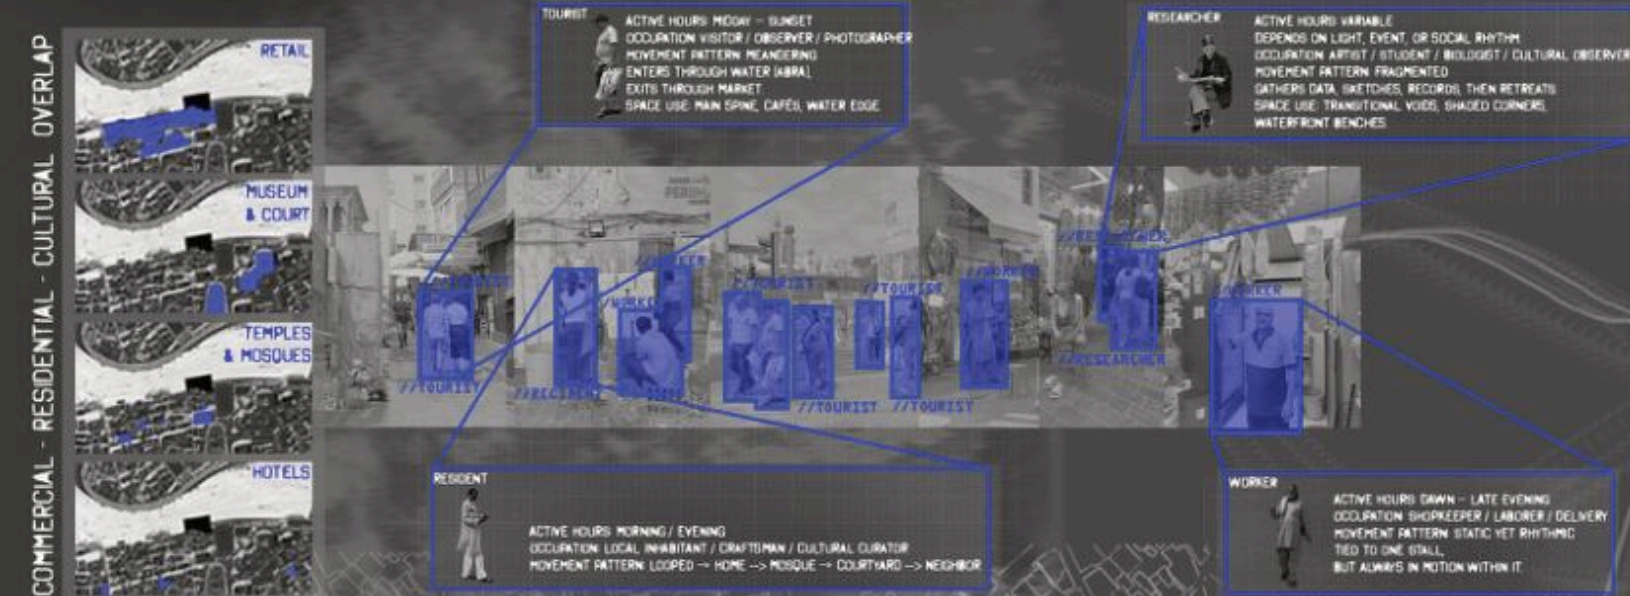


THE LOBSTER A PIECE OF CONTRADICTION

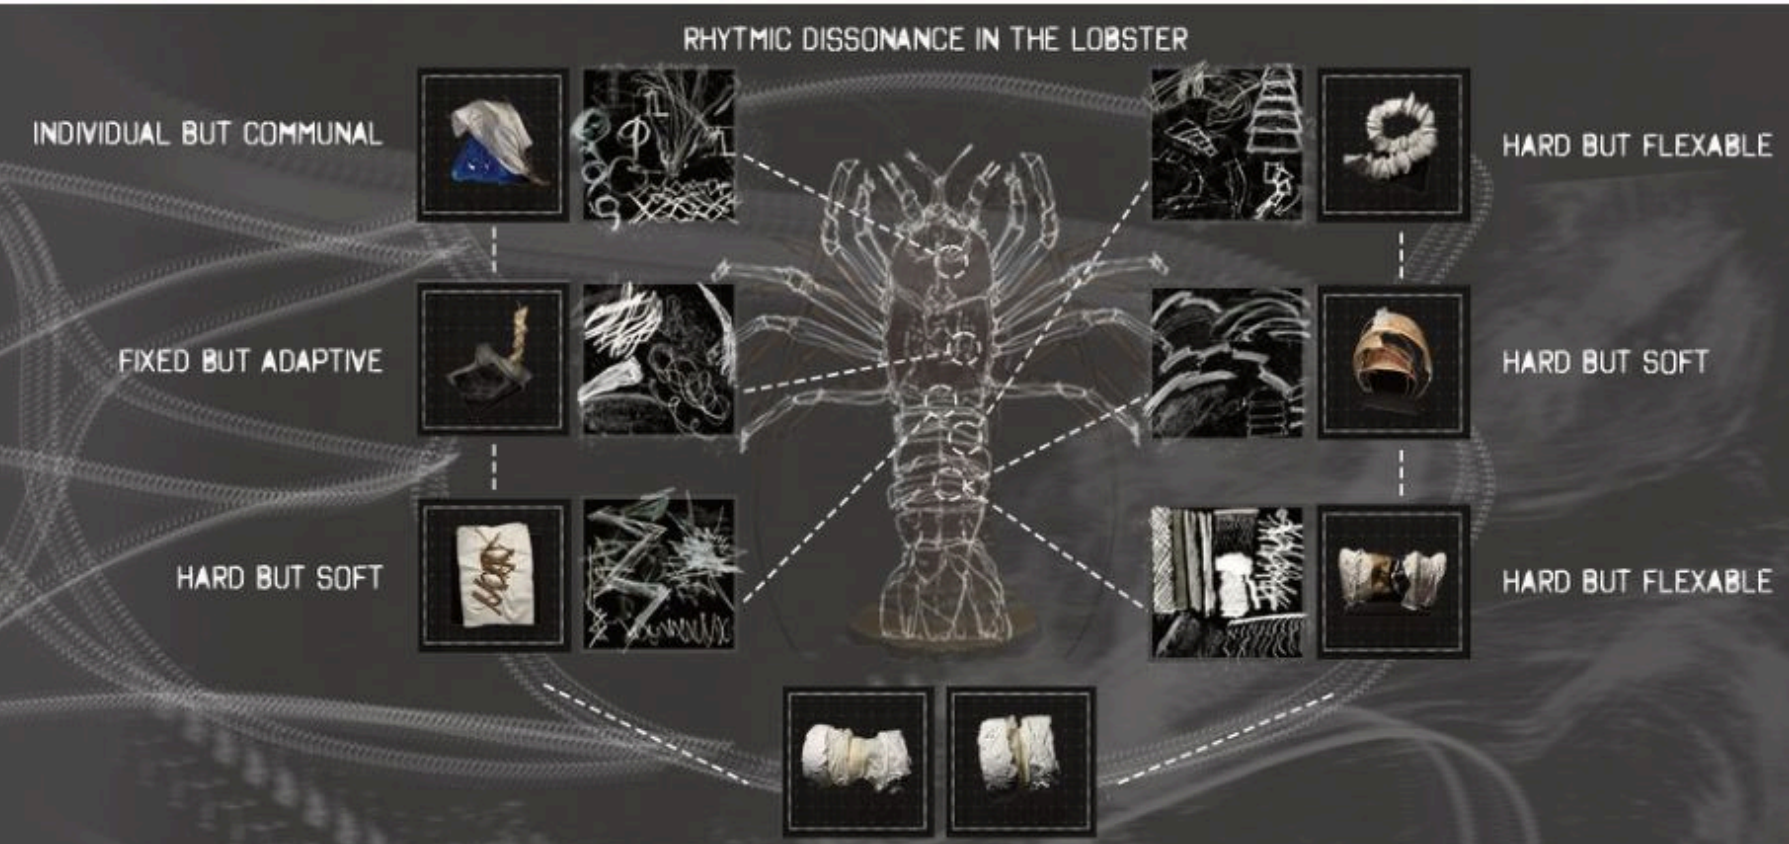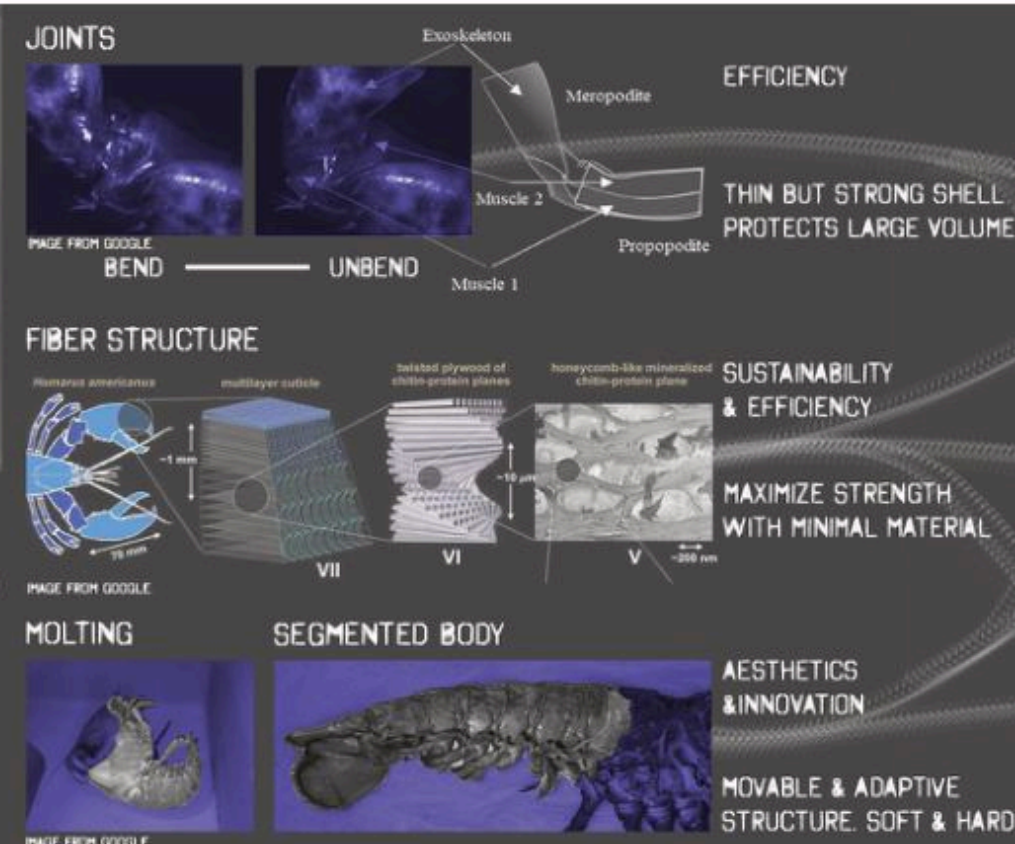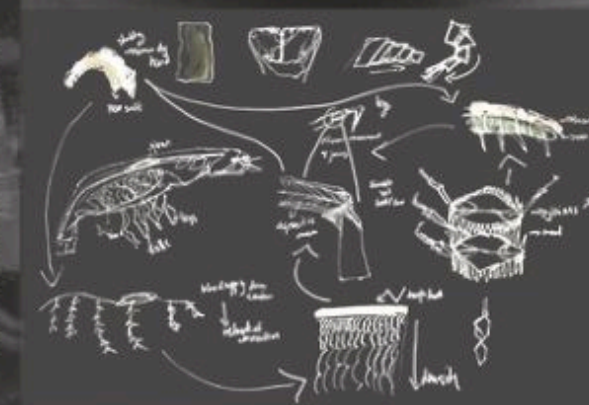


HYBRID USE OF SPACE

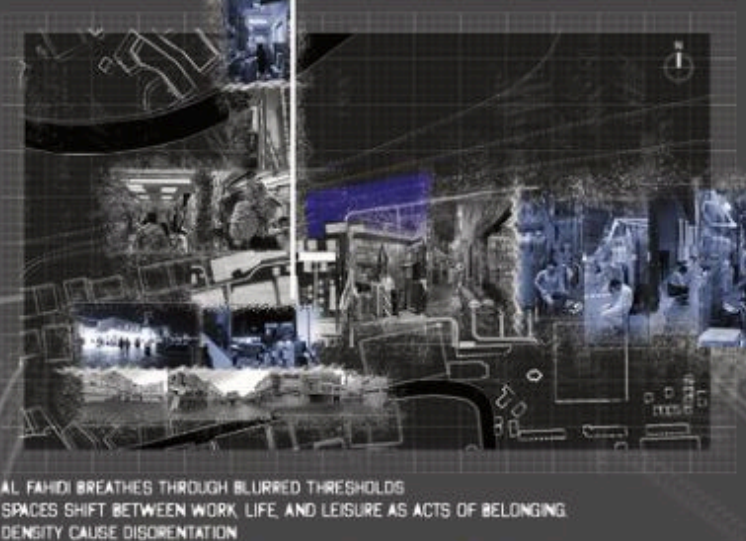

SENSORY OVERLOAD

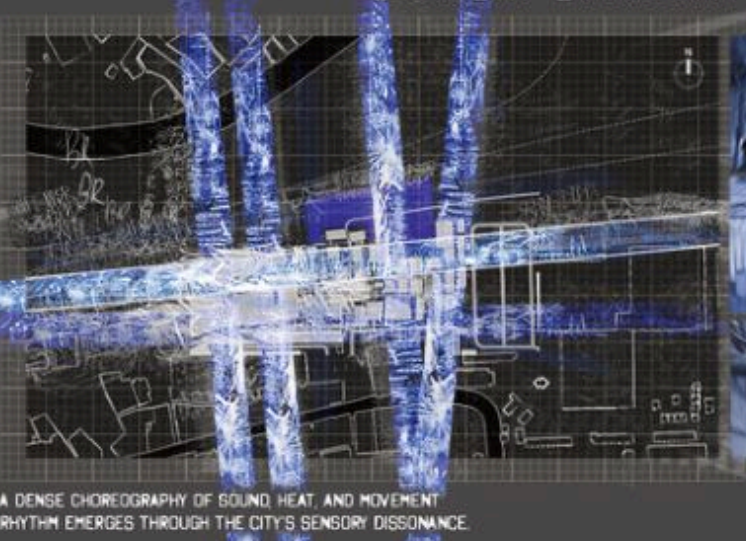

RESTORATIVE ZONES

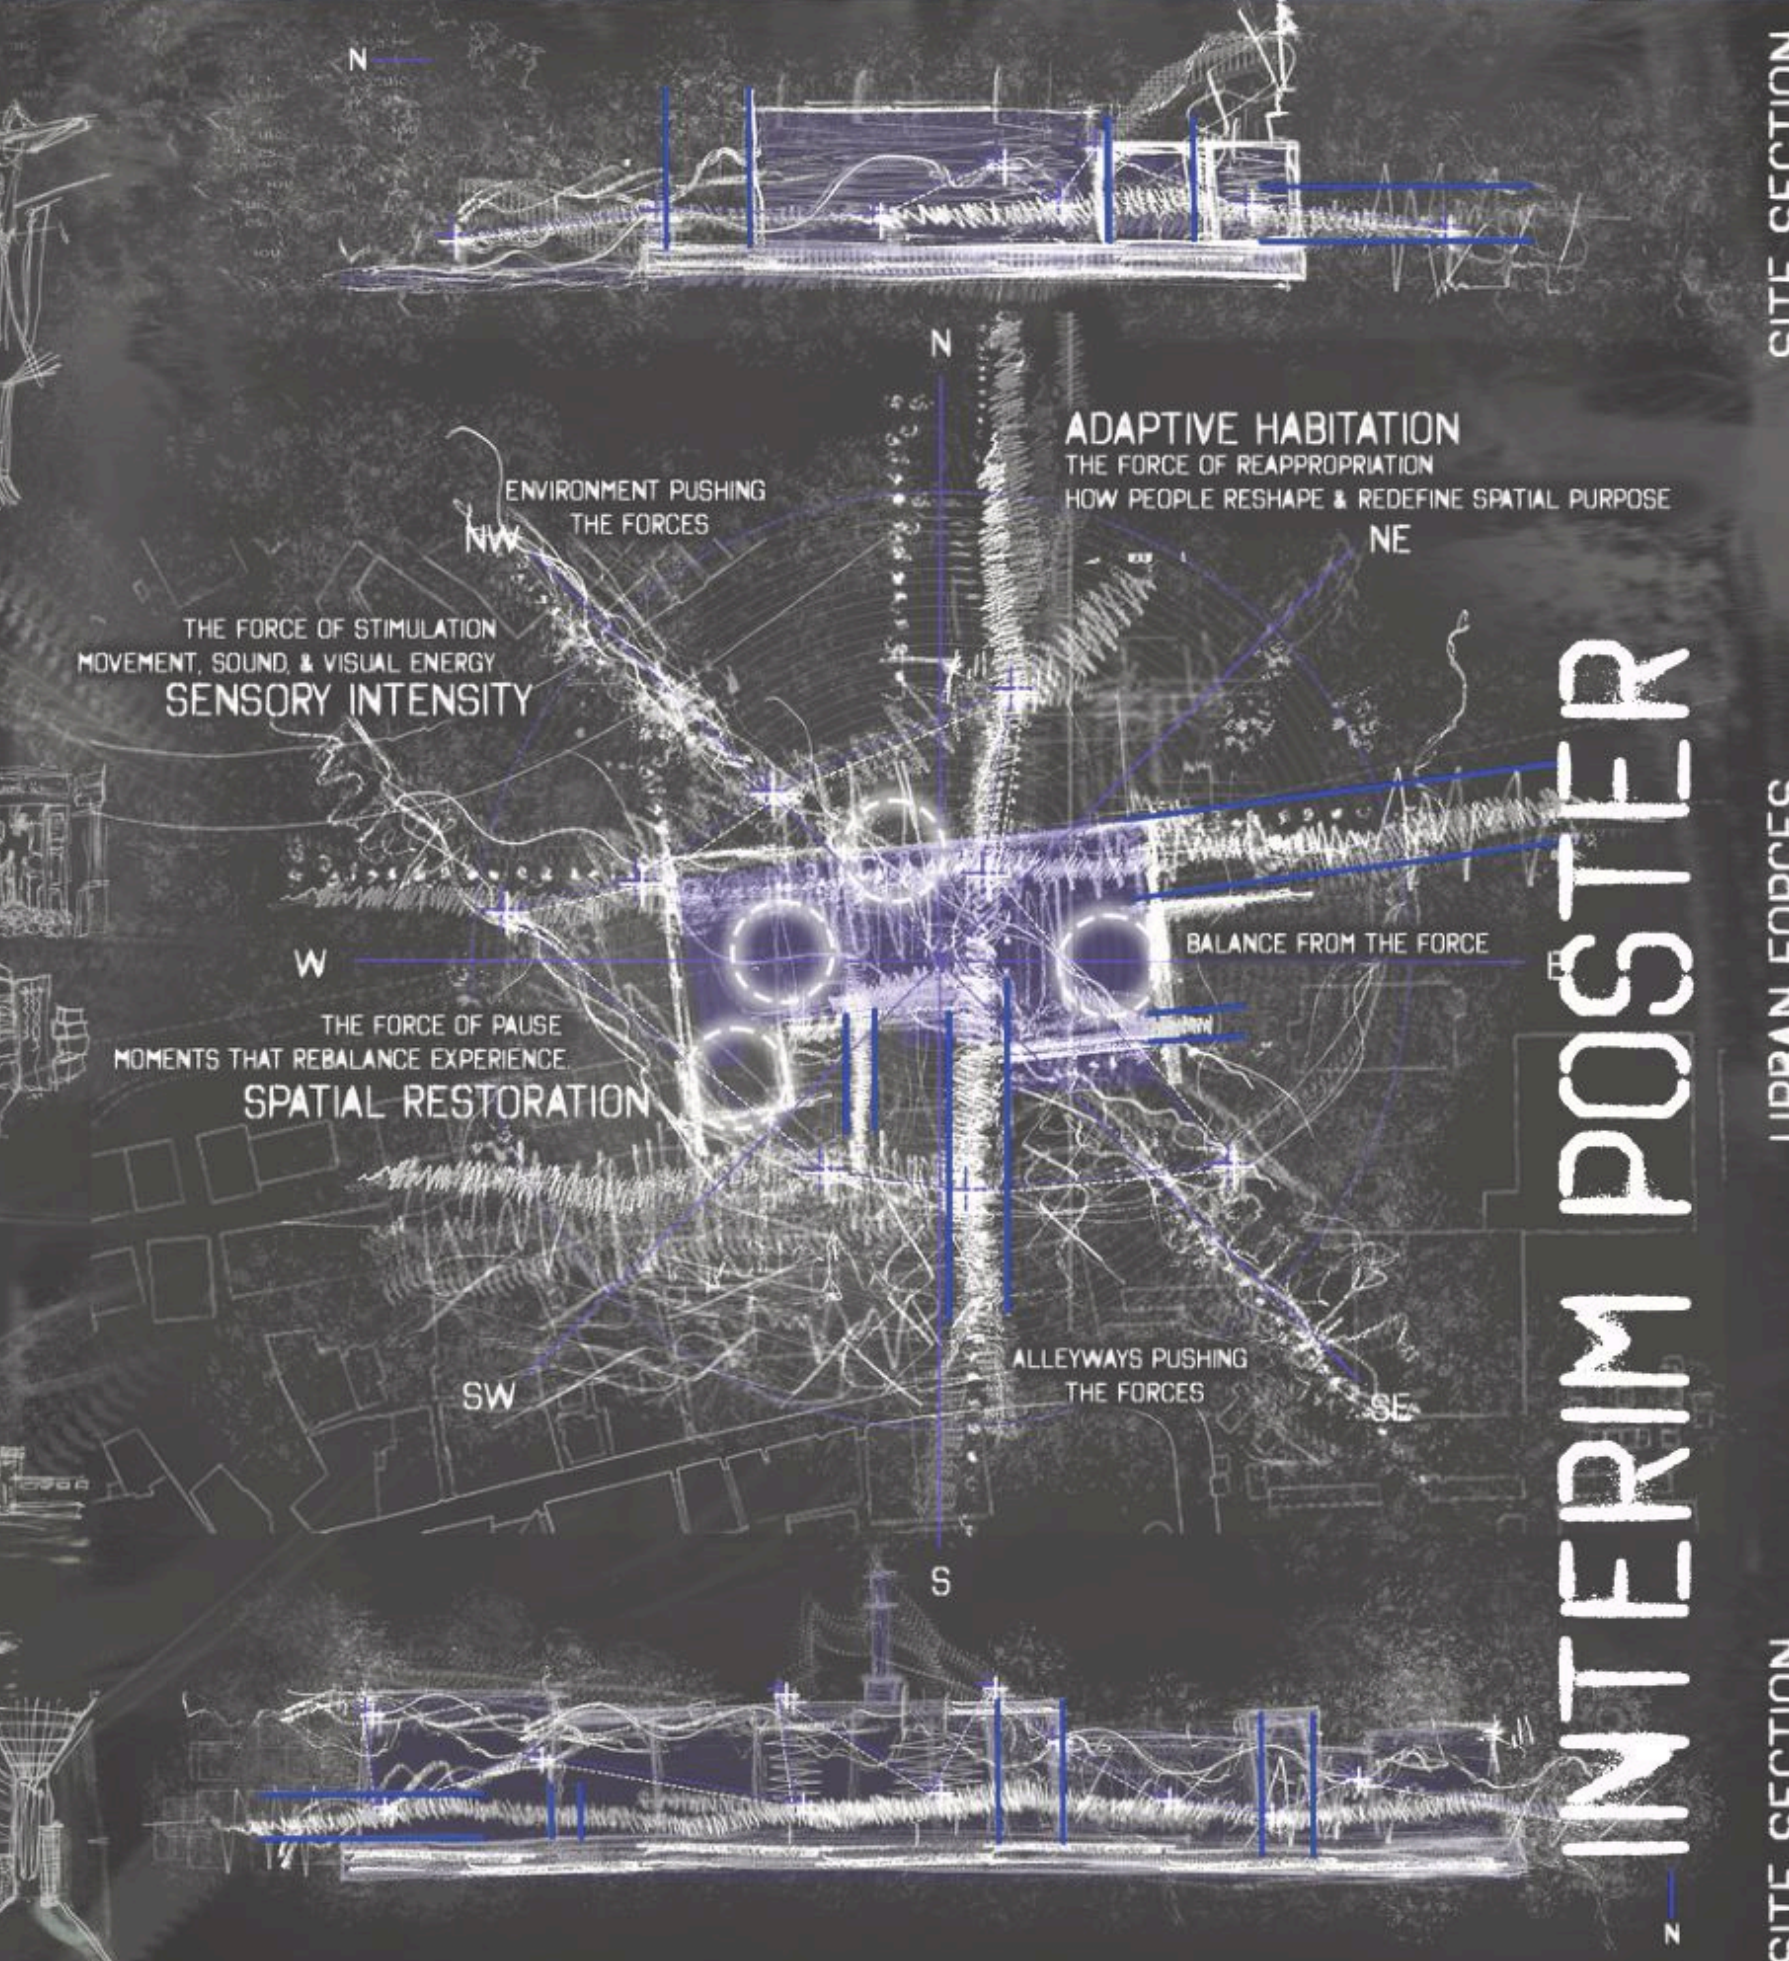

INTERIM POSTER

